

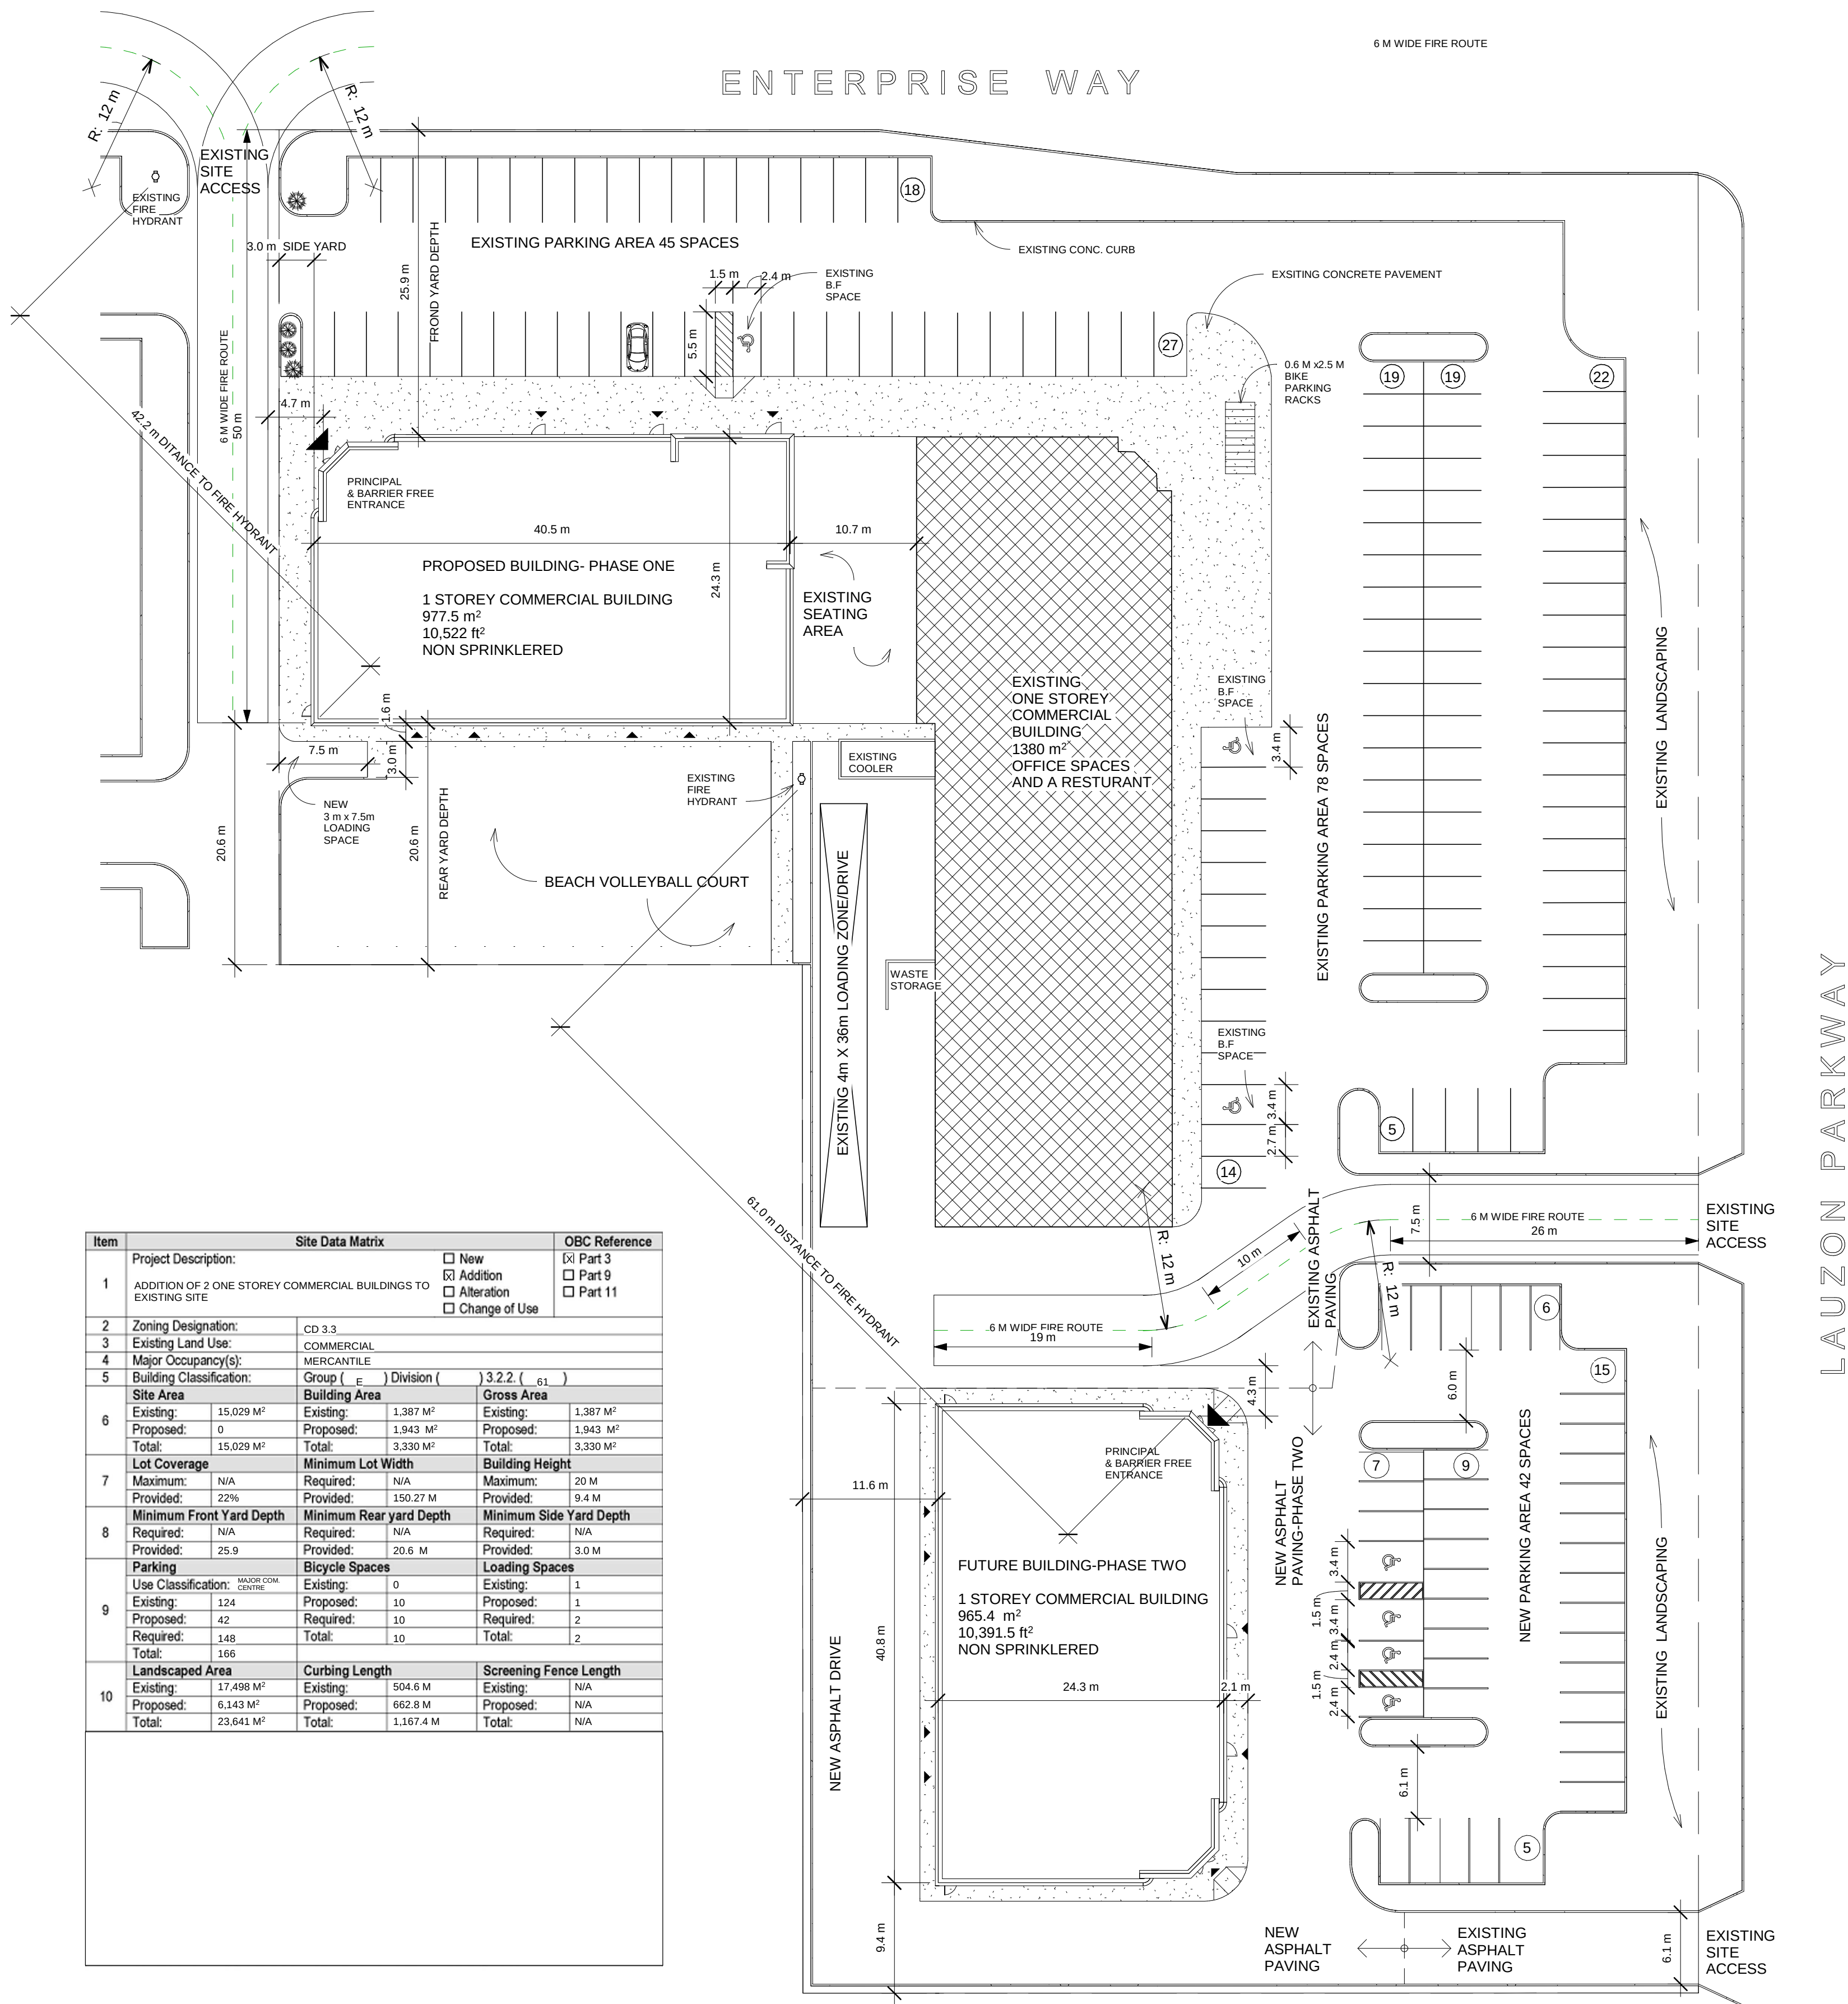


FIGURE 7.1
PARKING SPACE FOR PERSONS WITH DISABILITIES
TYPE A



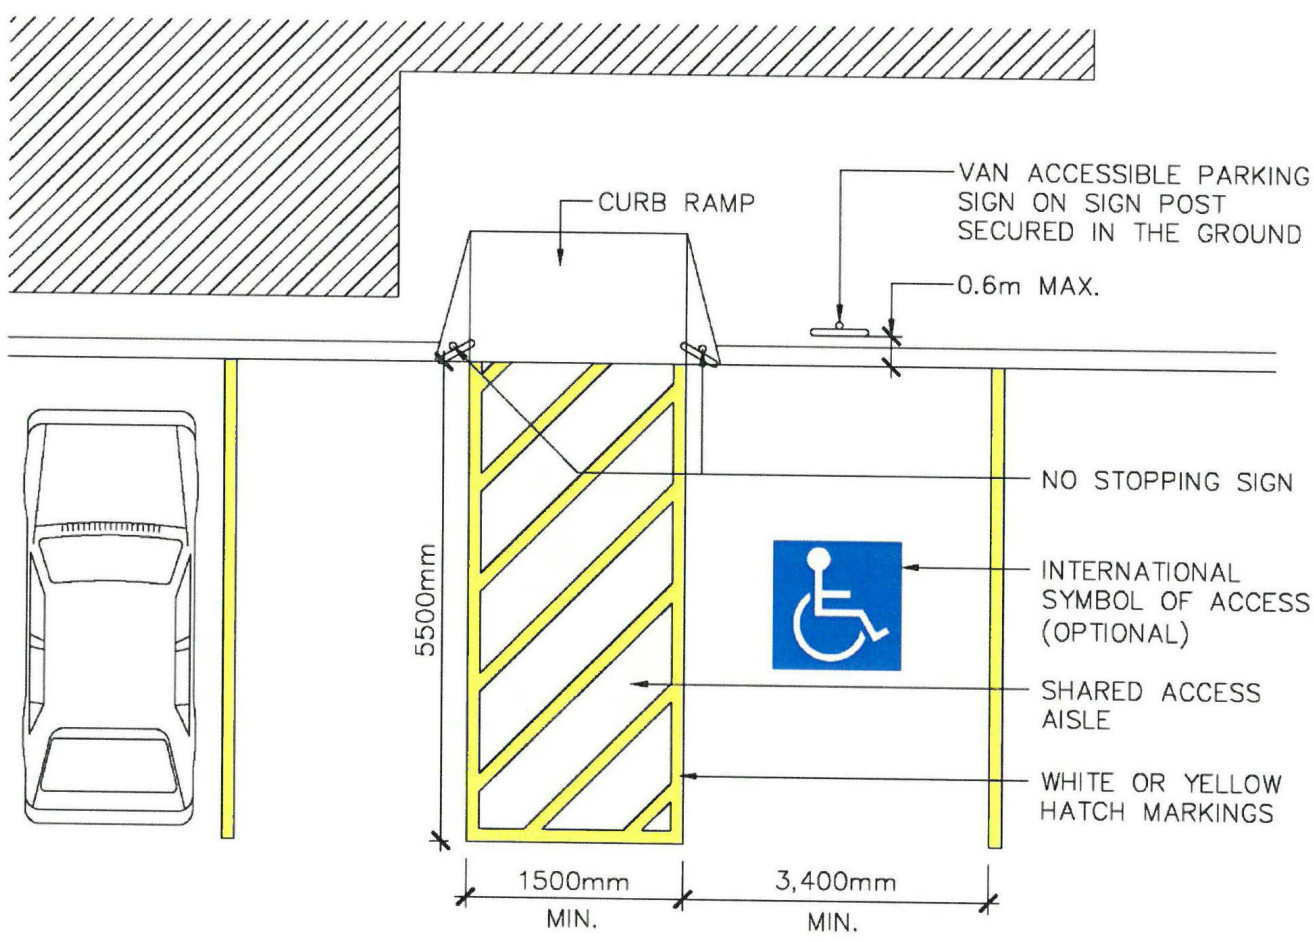


FIGURE 7.2
PARKING SPACE FOR PERSONS WITH DISABILITIES
TYPE B

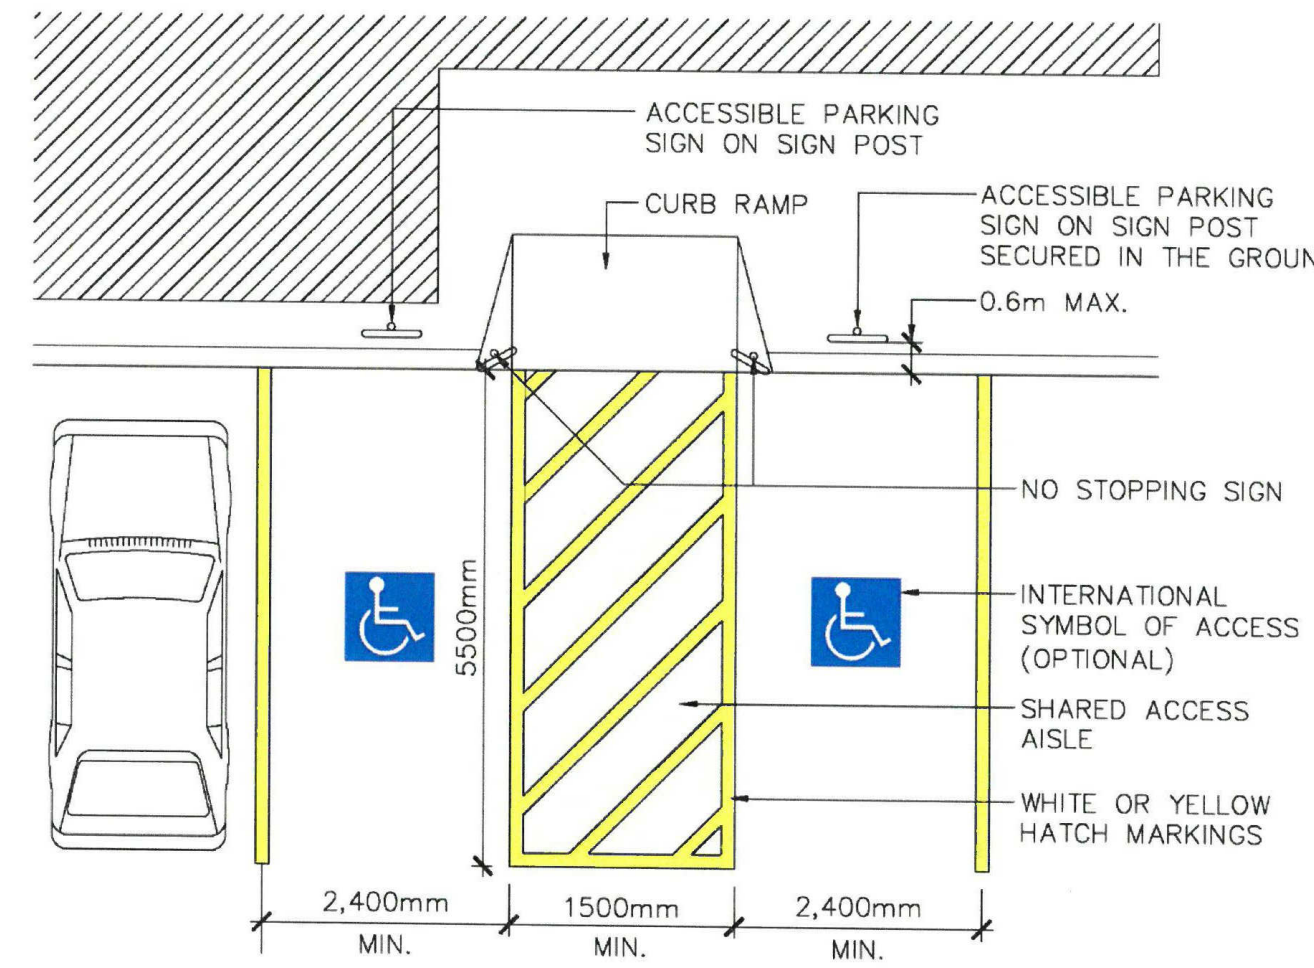

(SEE ALSO THE TRAFFIC AND PARKING BY-LAW)

FIGURE 7.3
ACCESSIBLE PARKING SIGN
HIGHWAY TRAFFIC ACT, REGULATION 581
PRESCRIBED SIGNS FOR PARKING SPACES UNDER THE HIGHWAY TRAFFIC ACT, REGULATION 581
PRESCRIBED SIGNS FOR PARKING SPACES DESIGNATED UNDER A
MUNICIPAL BY-LAW FOR THE USE OF PEOPLE WITH DISABILITIES

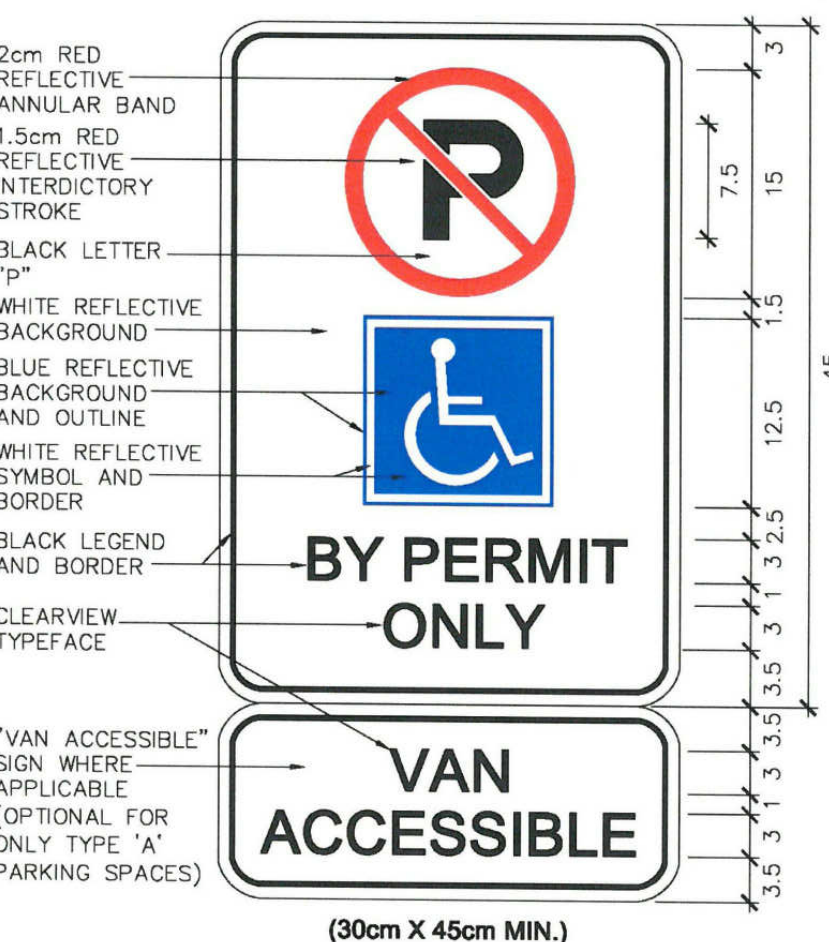

NOTE: SIGN ON A POST TO BE AT LEAST 1.5M ABOVE GRADE AND NOT MORE THAN 2.5M WHEN MEASURING FROM GRADE TO THE CENTRE OF THE SIGN.

FIGURE 7.4
INTERNATIONAL SYMBOL OF ACCESS
(OPTIONAL ON THE SURFACE OF THE PARKING SPACE)






Item		Site Data Matrix		OBC Reference	
1		Project Description:		☐ New ☒ Addition ☐ Alteration ☐ Change of Use	
2		Zoning Designation:		CD 3.3	
3		Existing Land Use:		COMMERCIAL	
4		Major Occupancy(s):		MERCANTILE	
5		Building Classification:		Group (E) Division () 3.2.2 (61)	
6		Site Area		Building Area	
		Existing: 15,029 M ²		Existing: 1,387 M ²	
		Proposed: 0		Proposed: 1,943 M ²	
		Total: 15,029 M ²		Total: 3,330 M ²	
7		Lot Coverage		Building Height	
		Maximum: 22%		Maximum: 20 M	
		Provided: 150.27 M		Provided: 9.4 M	
8		Minimum Front Yard Depth		Minimum Side Yard Depth	
		Required: N/A		Required: N/A	
		Provided: 25.9		Provided: 3.0 M	
9		Parking		Loading Spaces	
		Use Classification: MAJOR COMM. CENTRE		Existing: 0	
		Existing: 124		Proposed: 1	
		Proposed: 42		Required: 2	
		Required: 148		Total: 2	
		Total: 166			
10		Landscaped Area		Screening Fence Length	
		Existing: 17,498 M ²		Existing: N/A	
		Proposed: 6,143 M ²		Proposed: N/A	
		Total: 23,641 M ²		Total: N/A	

2
A001
SITE MATRIX
1 : 4

1
A001
SITE PLAN
1 : 360

8			16		
7			15		
6			14		
5			13		
4			12		
3			11		
2			10		
1	07.26.20	SPA	9		
rev.	date	issued for	rev.	date	issued for

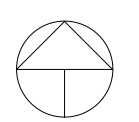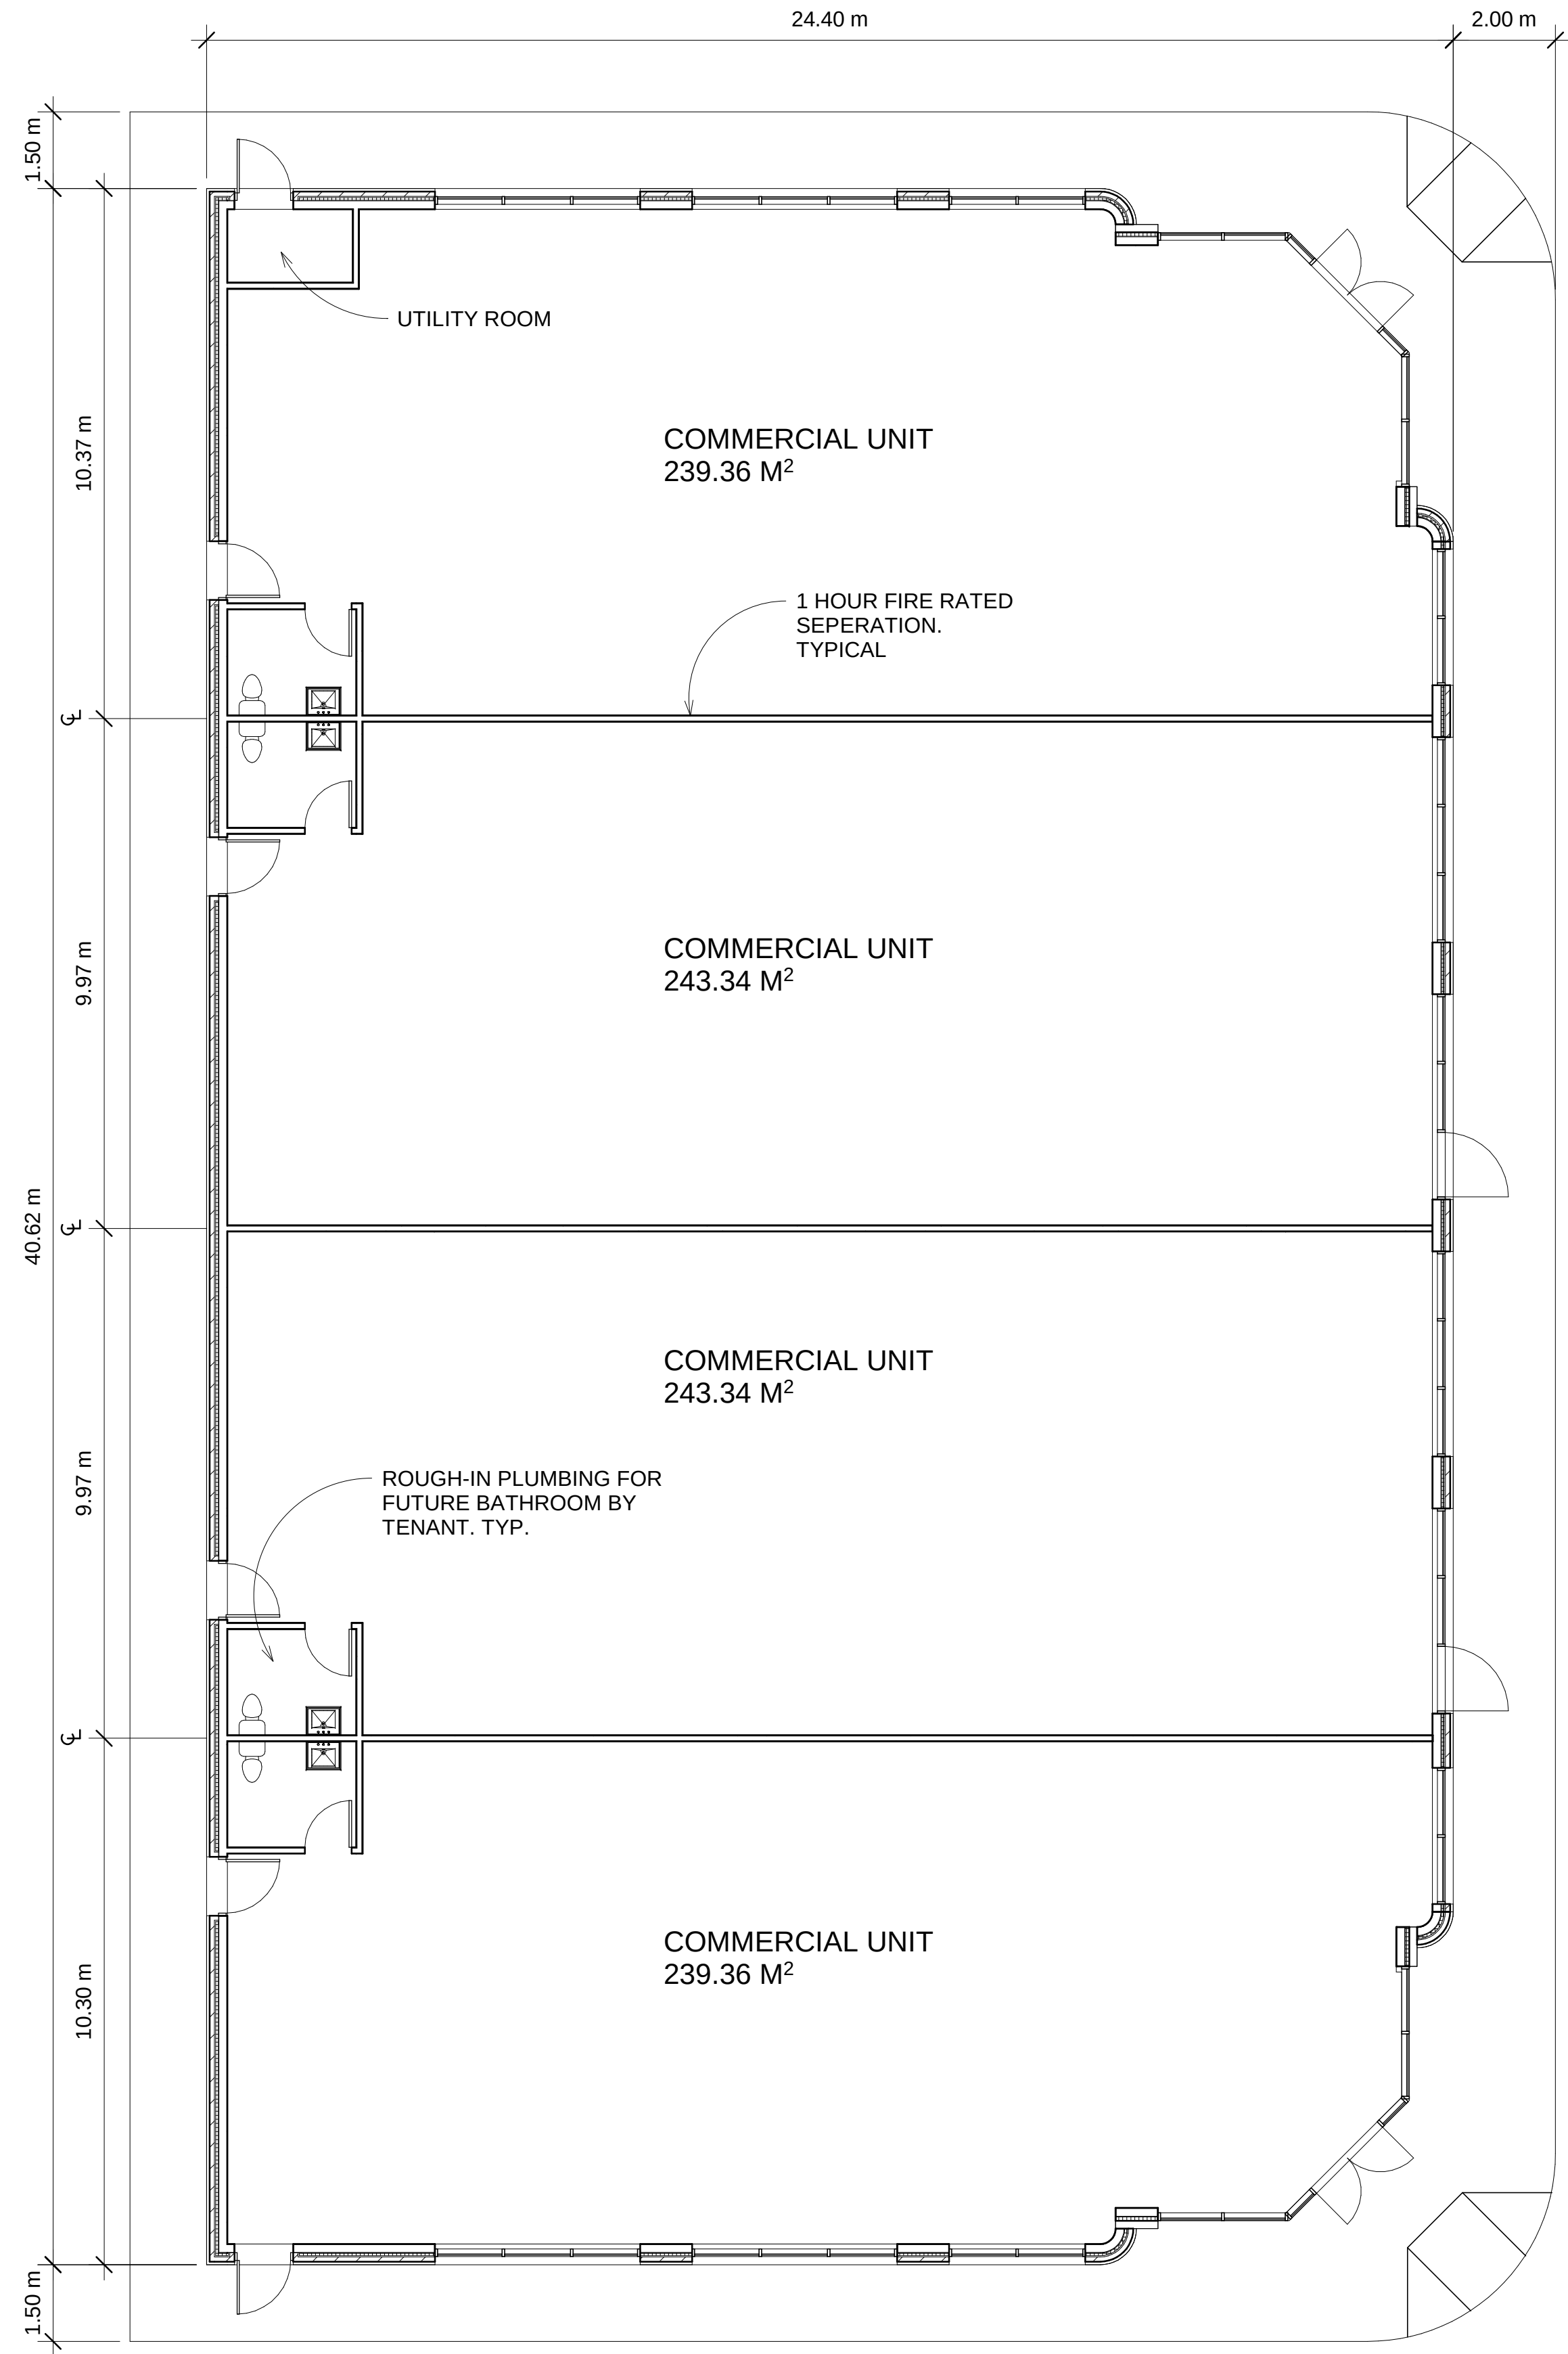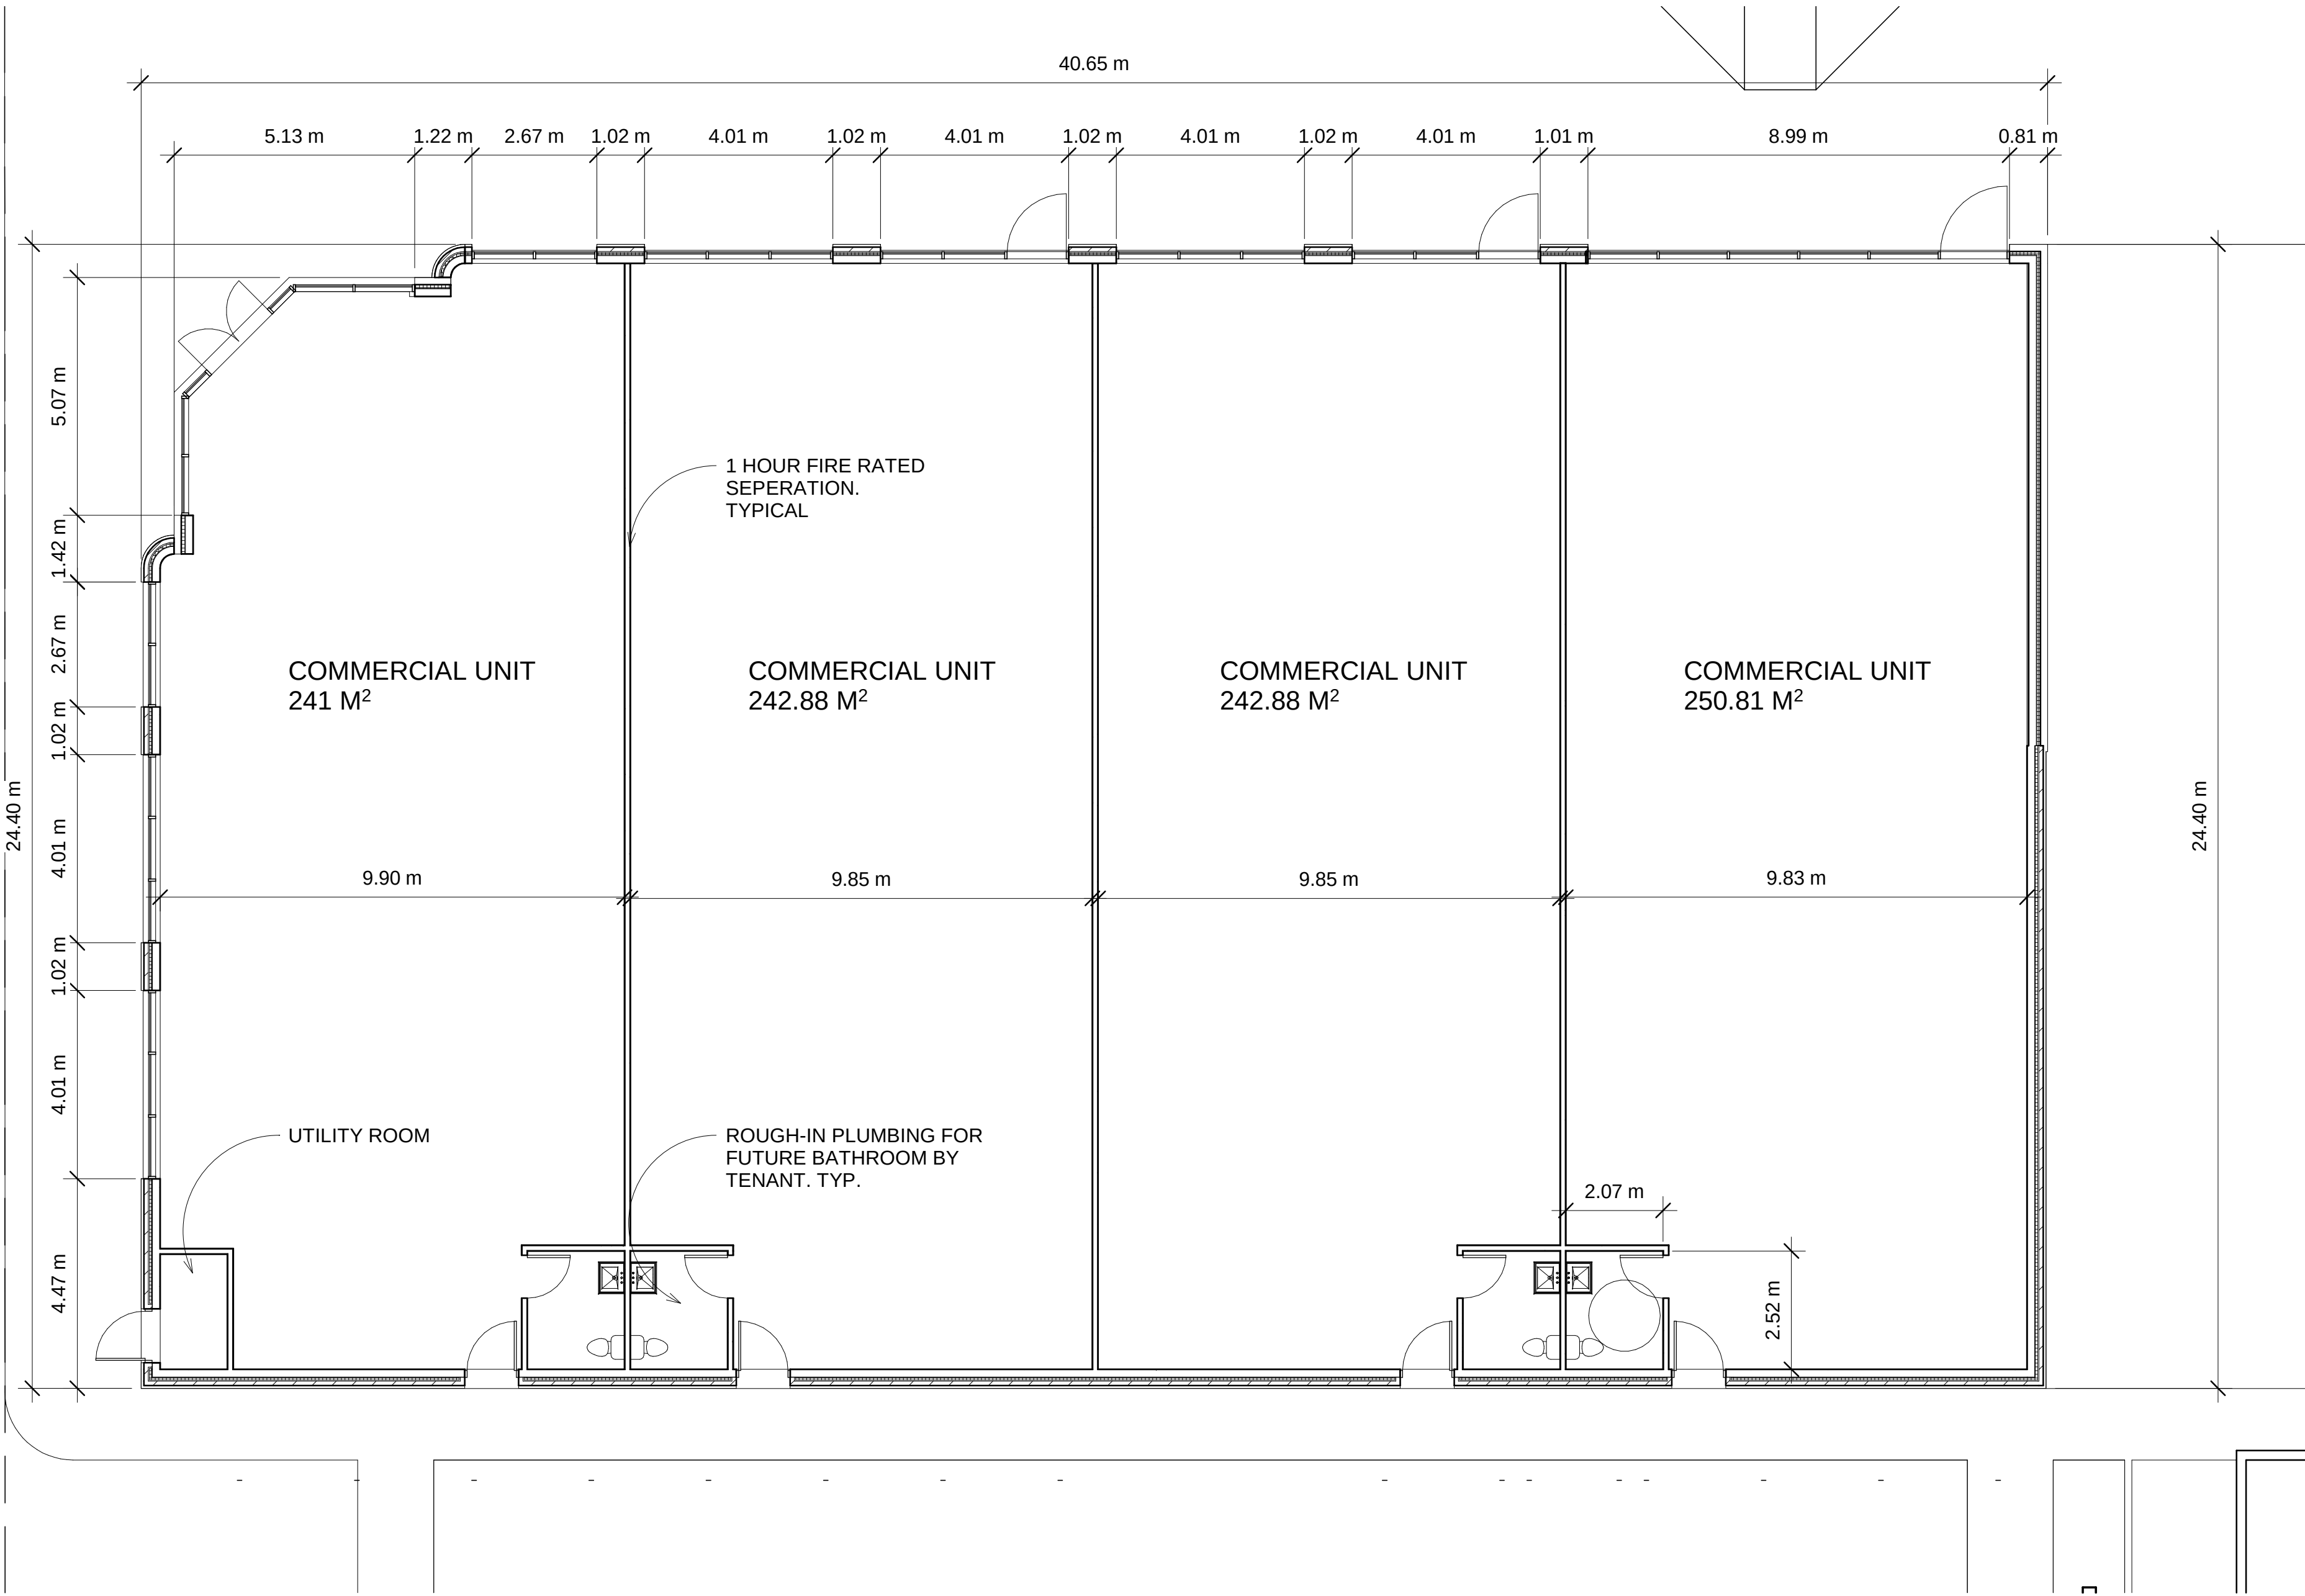

1
A201

GROUND FLOOR PLAN-PHASE ONE


1 : 100



3100 TEMPLE DR. SUITE 100, WINDSOR ON. 519-919-7490

ALL DRAWINGS, SPECIFICATIONS AND OTHER RELATED DOCUMENTS ARE THE COPYRIGHT PROPERTY OF THE CONSULTANT AND SHALL BE RETURNED UPON REQUEST. REPRODUCTION OF DRAWINGS AND RELATED DOCUMENTS, IN WHOLE OR IN PART, IS FORBIDDEN WITHOUT THE WRITTEN PERMISSION OF THE CONSULTANT. THE CONTRACTOR SHALL CHECK AND VERIFY ALL PERTINENT DIMENSIONS AND REPORT ANY DISCREPANCIES TO THE CONSULTANT BEFORE PROCEEDING WITH THE WORK. THIS DRAWING SHALL NOT BE USED FOR CONSTRUCTION UNLESS IT IS COUNTERSIGNED BY THE CONSULTANT. THIS DRAWING IS NOT TO BE SCALED. USE FIGURED DIMENSIONS ONLY.

ENTERPRISE PLAZA

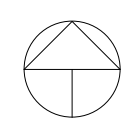

2
A201

GROUND FLOOR PLAN-PHASE TWO

1 : 100

8			16		
7			15		
6			14		
5			13		
4			12		
3			11		
2			10		
1	07.26.20	SPA	9		
rev.	date	issued for	rev.	date	issued for


project:
ENTERPRISE PLAZA

address: Enter address here


sheet name:
GROUND FLOOR PLAN-PHASE ONE & TWO

project no.:
20-0029

sheet no.:
A201

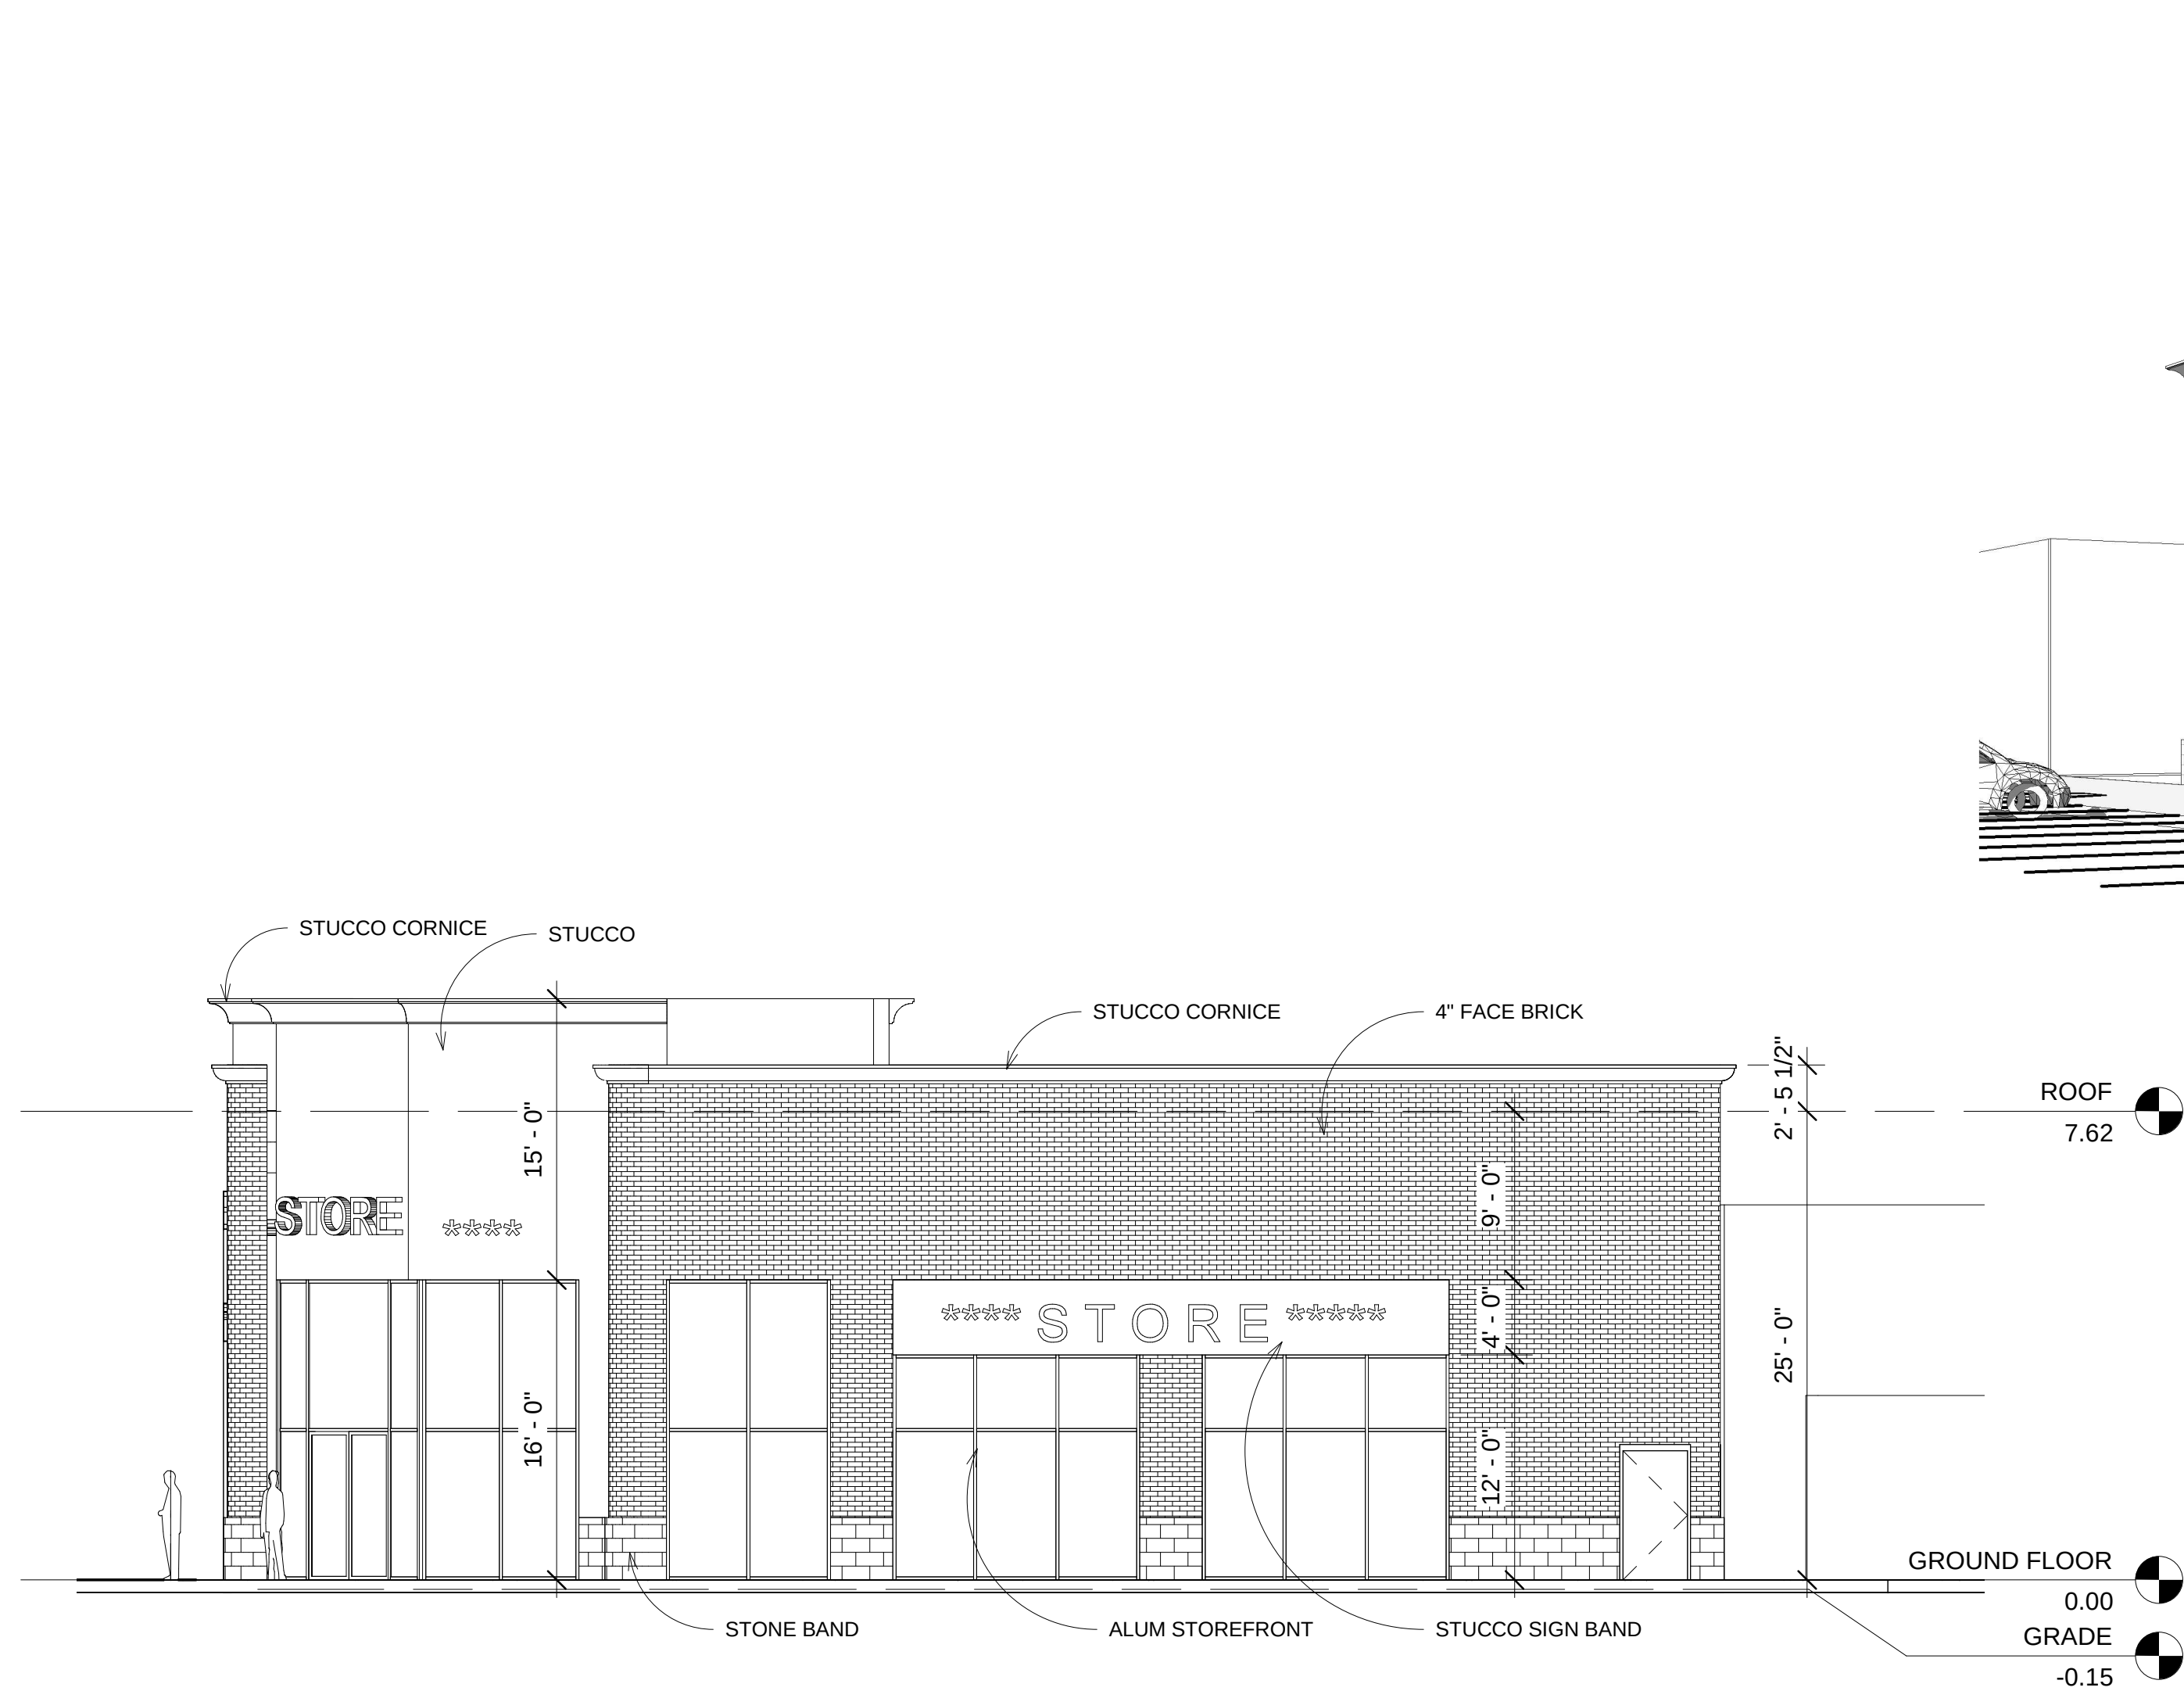


2 WEST ELEVATION-PHASE ONE
1 : 96

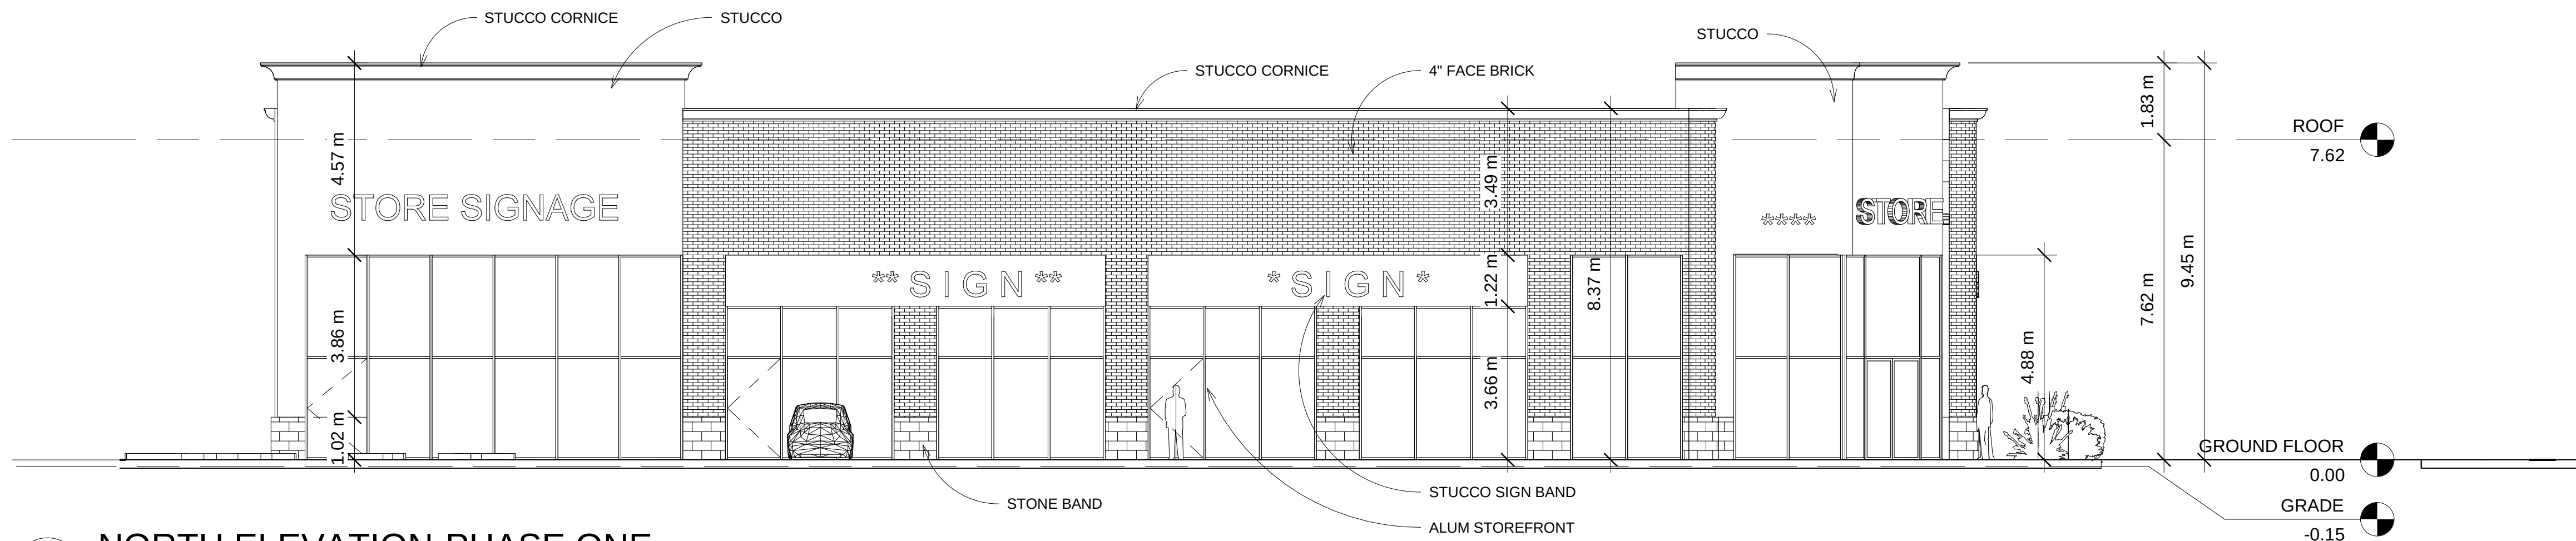


1 NORTH ELEVATION-PHASE ONE
1 : 100




3 EYE LEVEL-NORTHWEST VIEW-PHASE ONE
A401

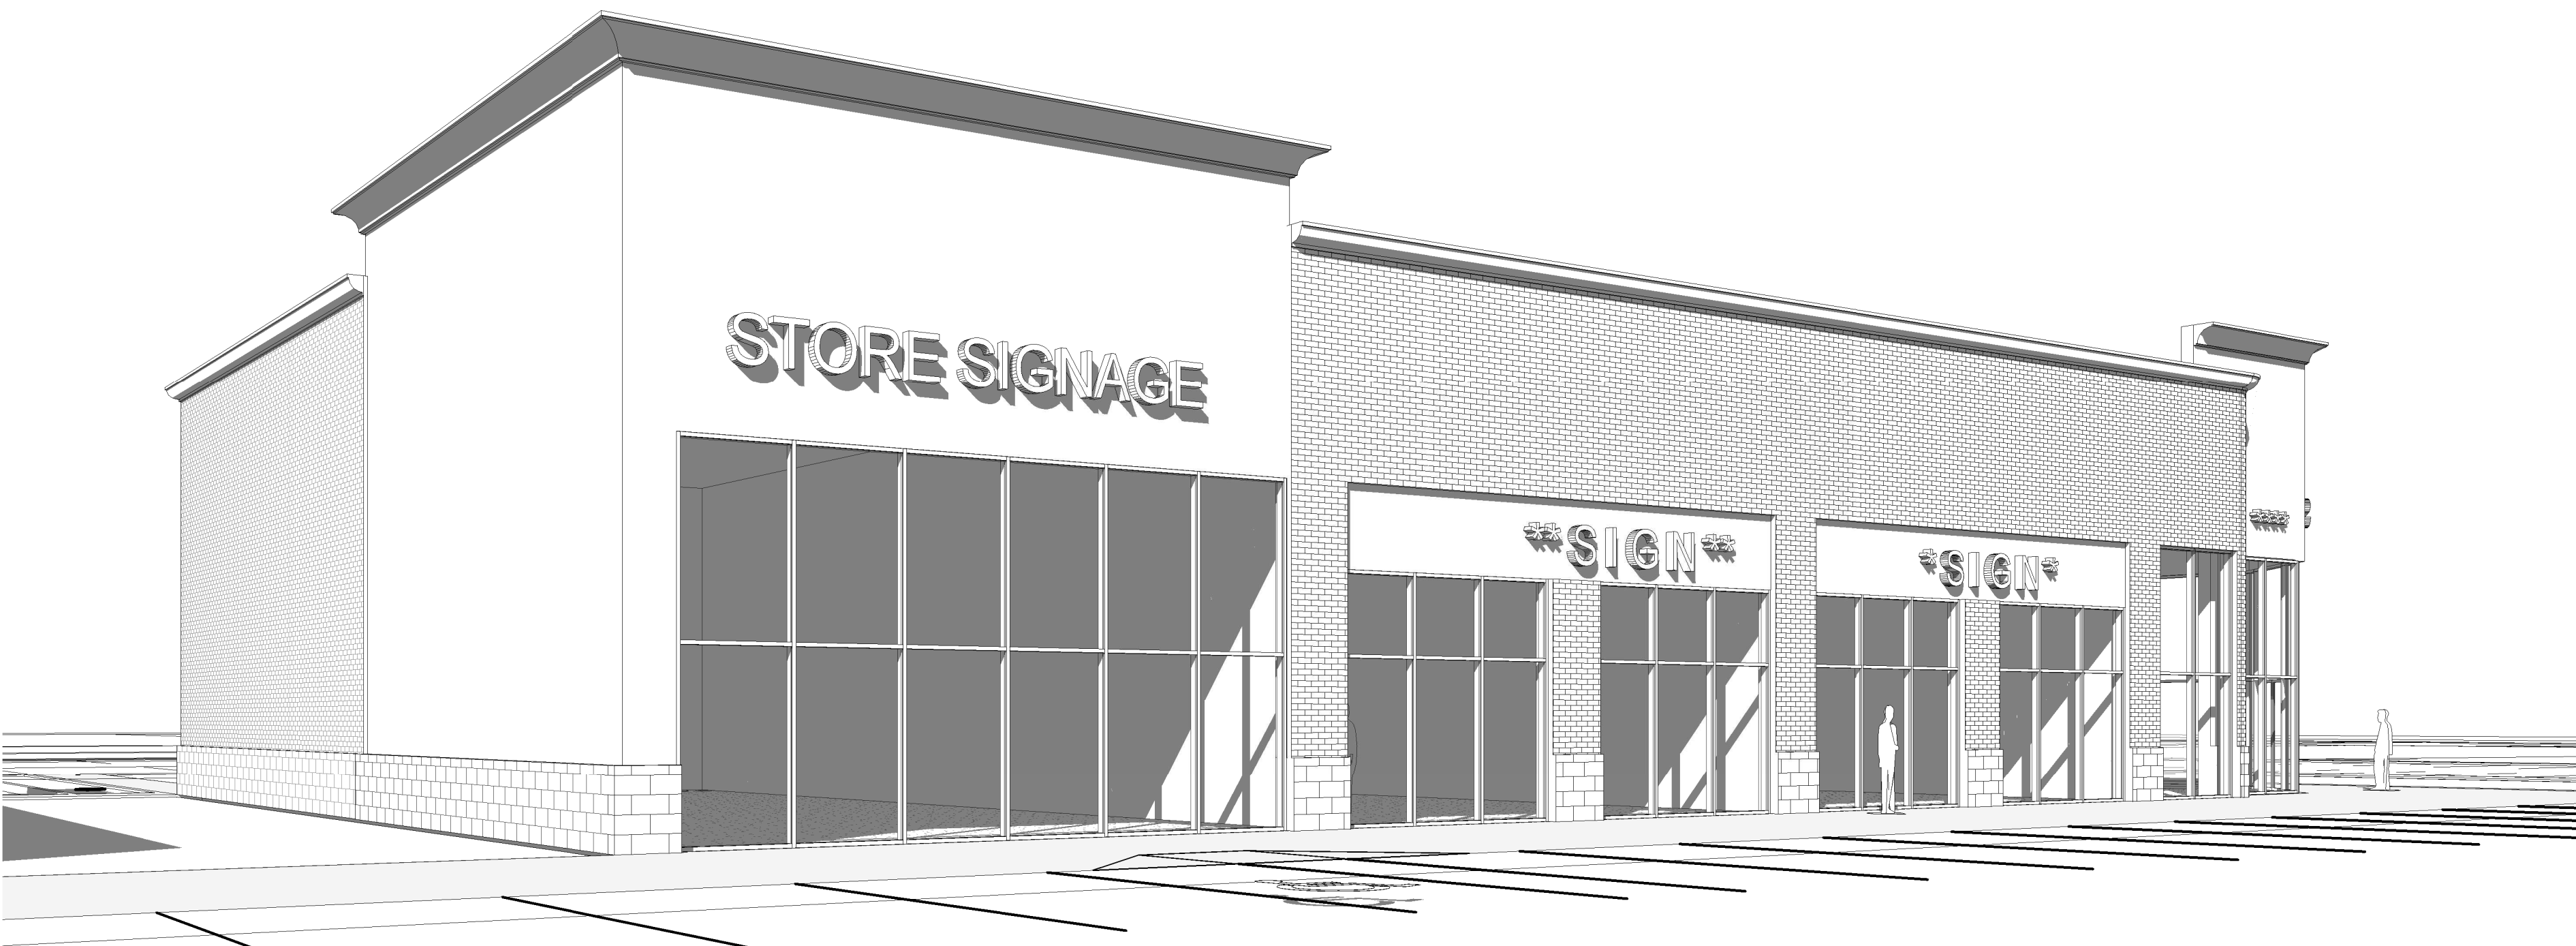

3
A402
EYEL LEVEL-NORTHEAST VIEW-PHASE ONE

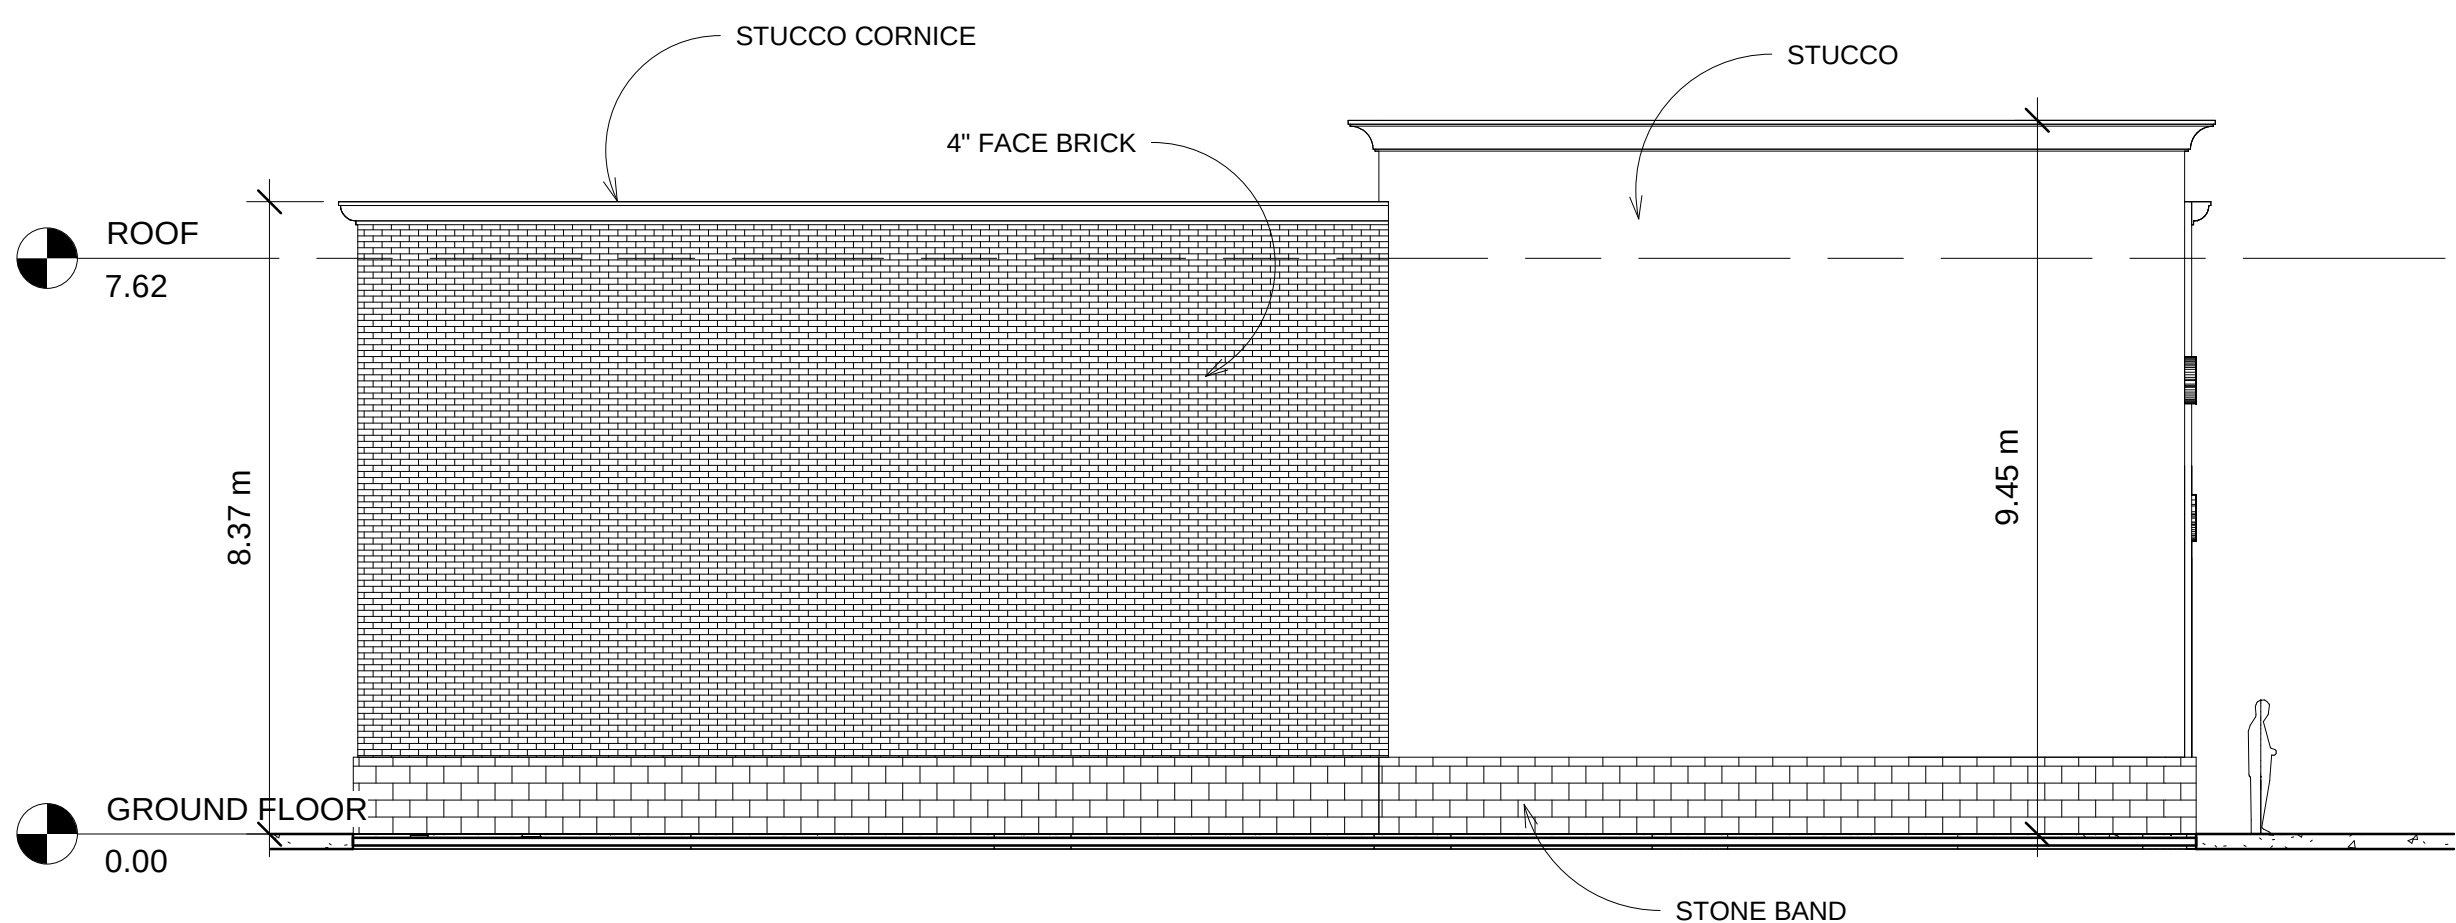


2
A402
EAST ELEVATION-PHASE ONE
1 : 100

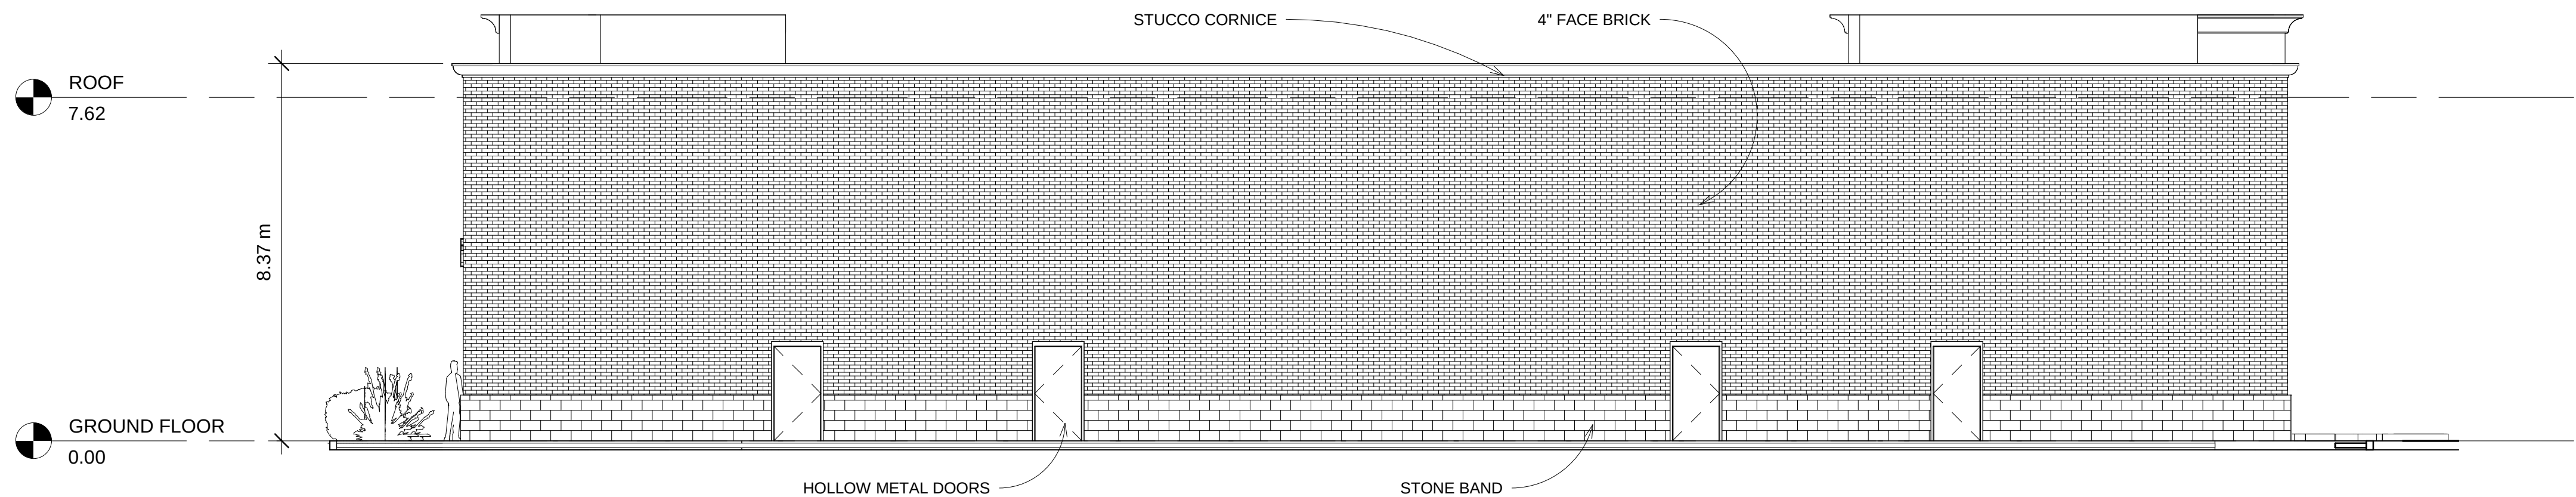


1
A402
SOUTH ELEVATION-PHASE ONE
1 : 100


8			16		
7			15		
6			14		
5			13		
4			12		
3			11		
2			10		
1	07.26.20	SPA	9		
rev.	date	issued for	rev.	date	issued for

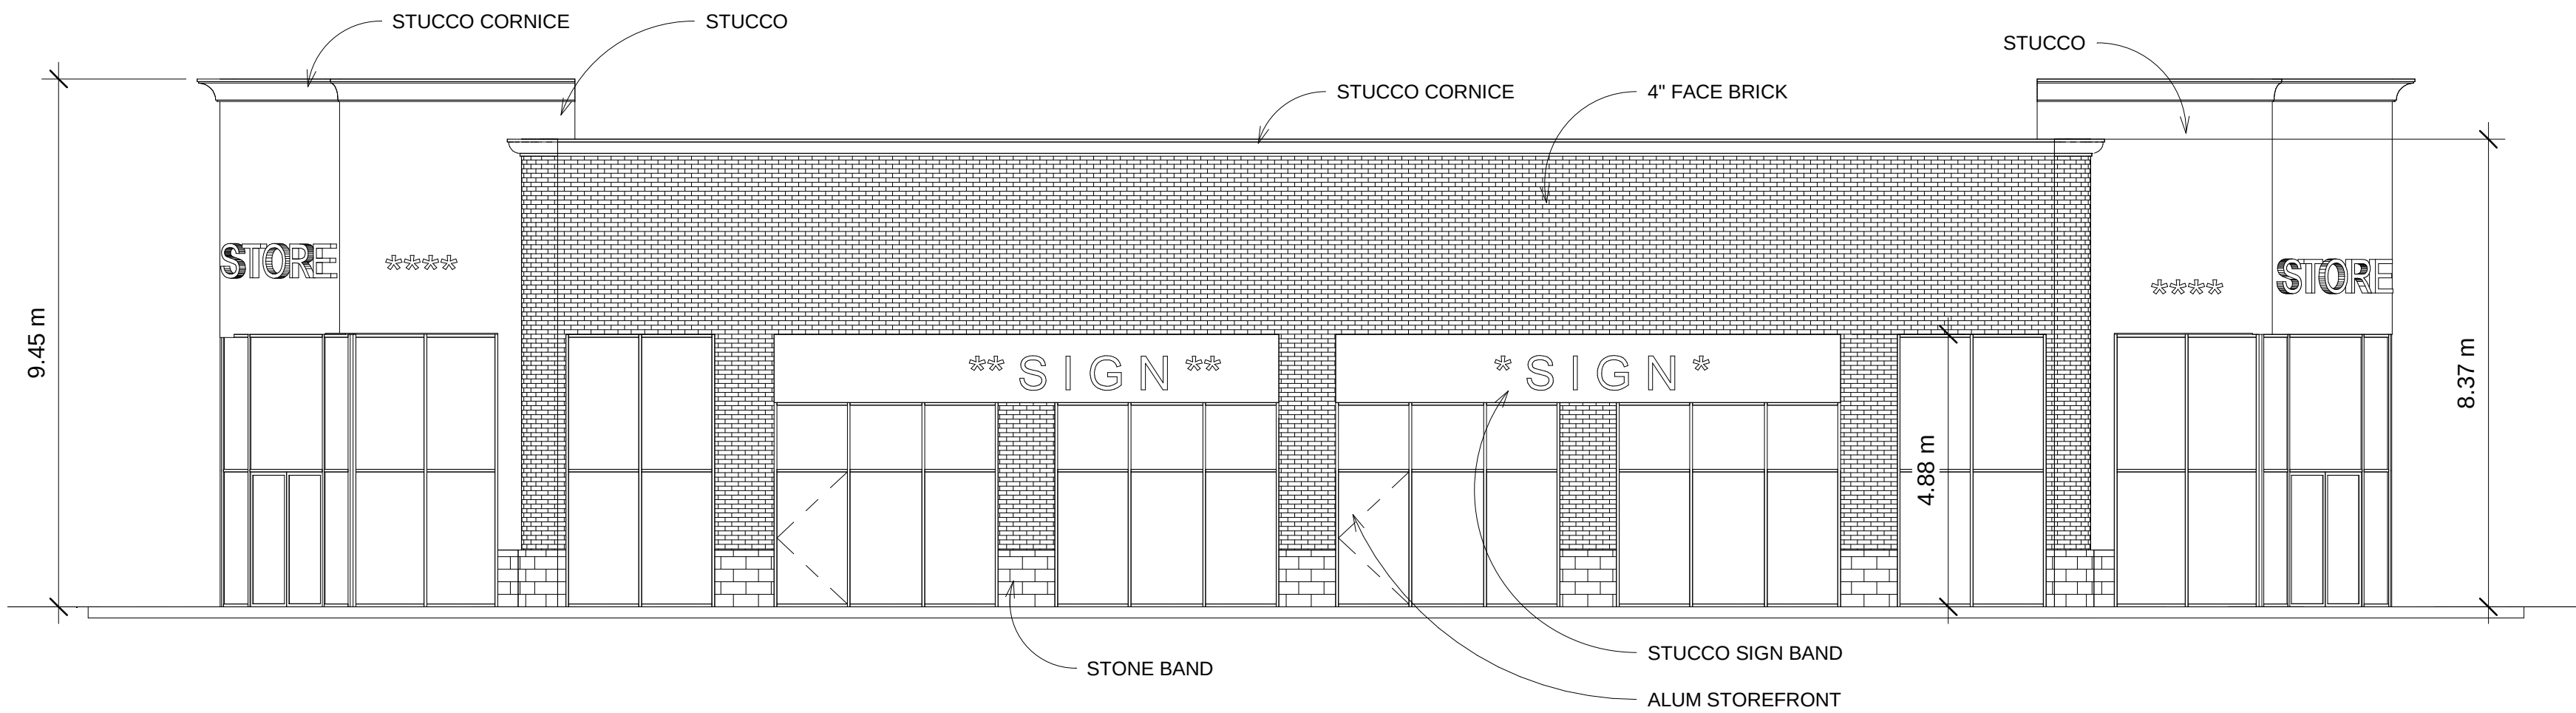


1 EAST ELEVATION-PHASE TWO
A403 1 : 100

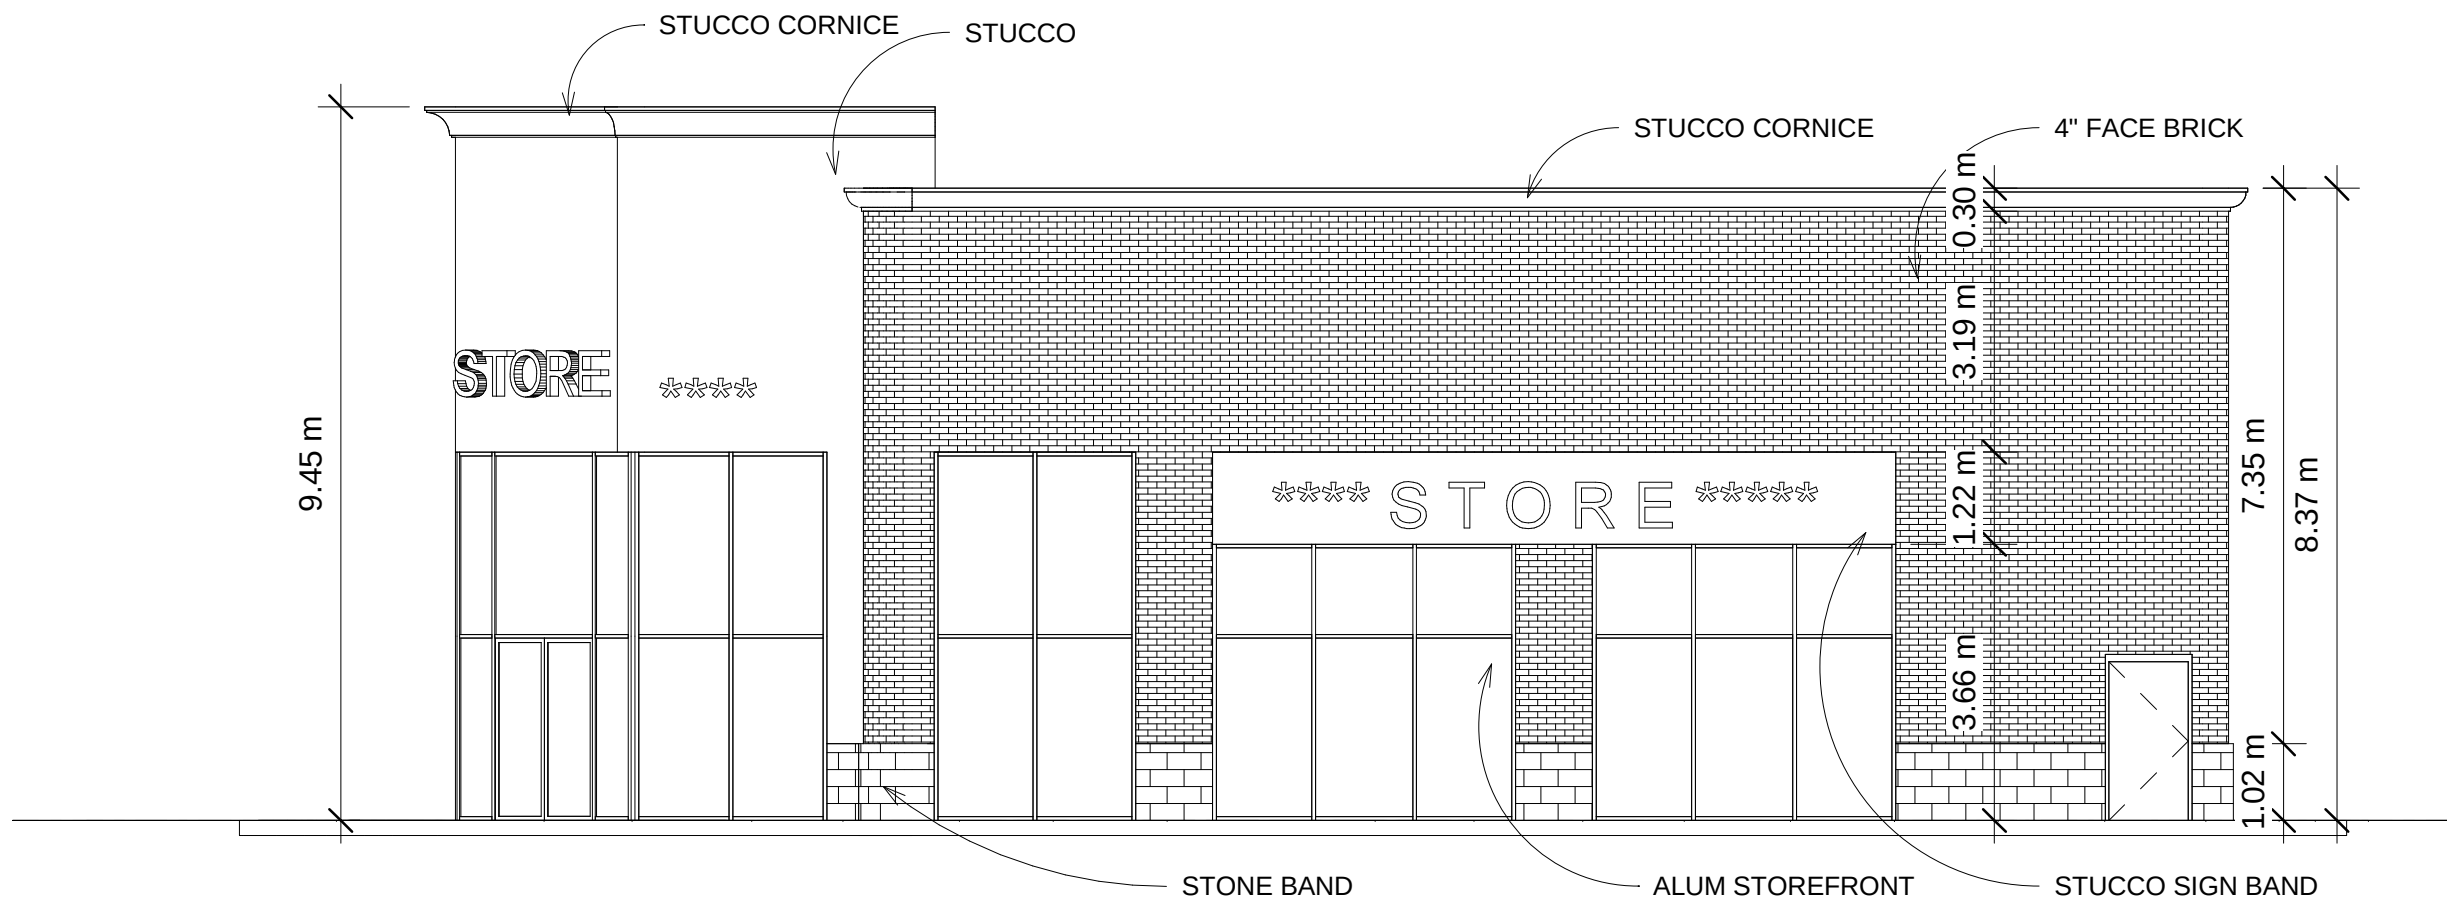

2 NORTH ELEVATION-PHASE TWO
A403 1 : 100

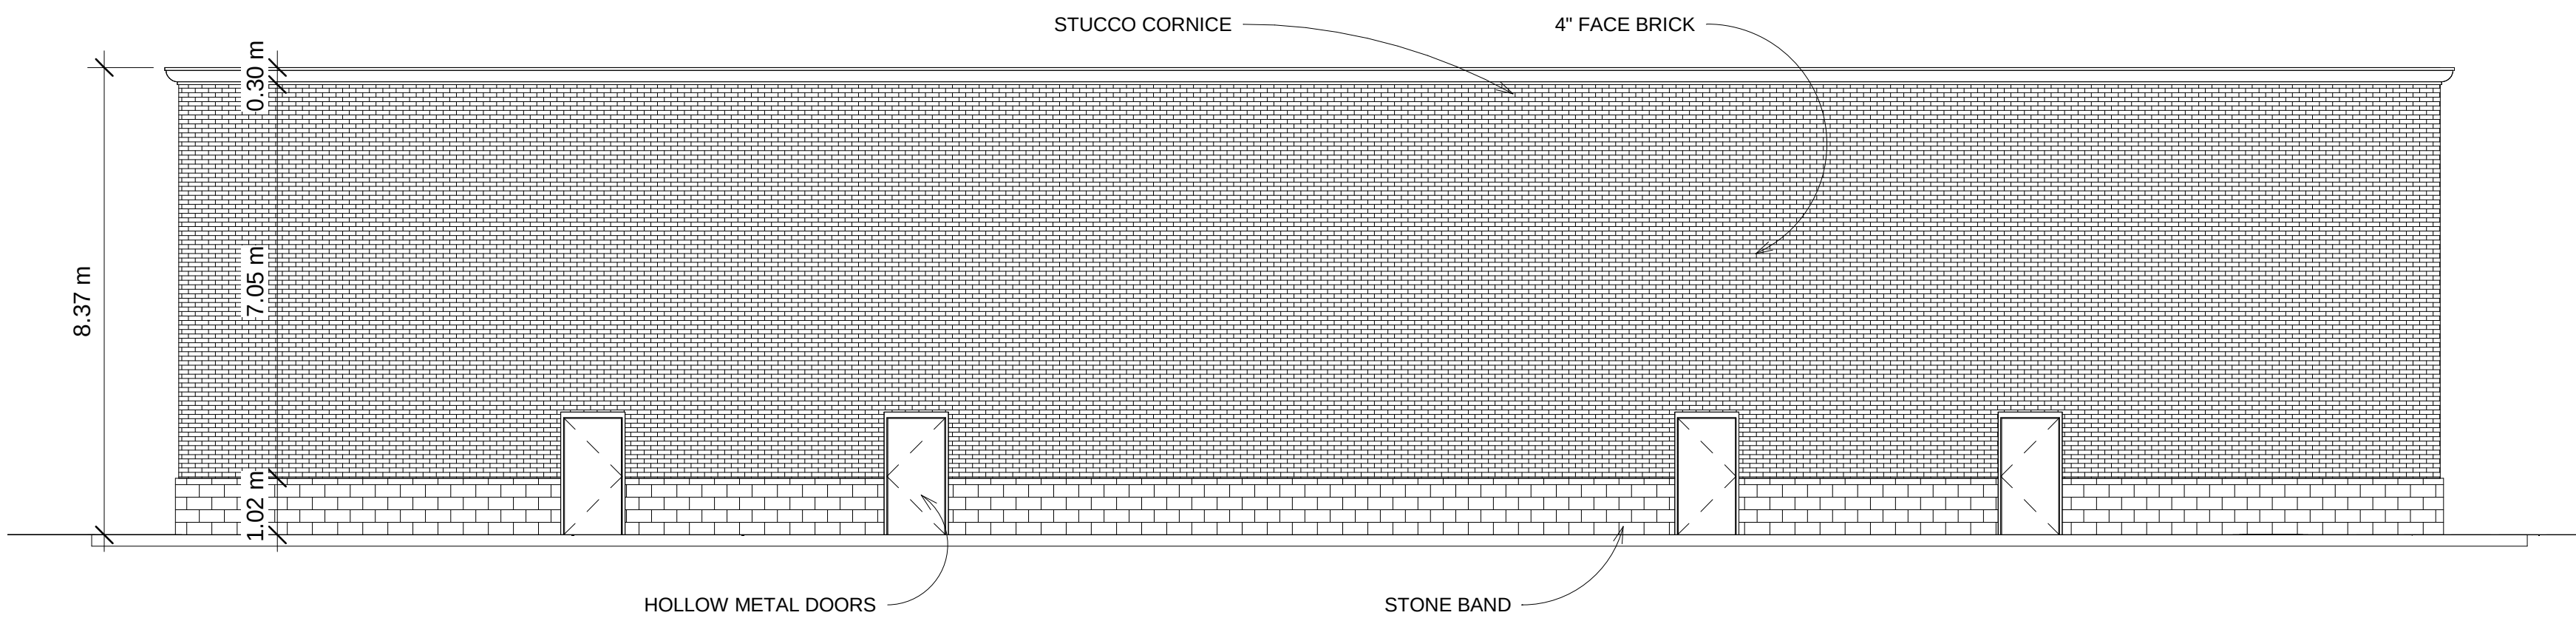


4 WEST ELEVATION-PHASE TWO
A403 1 : 100

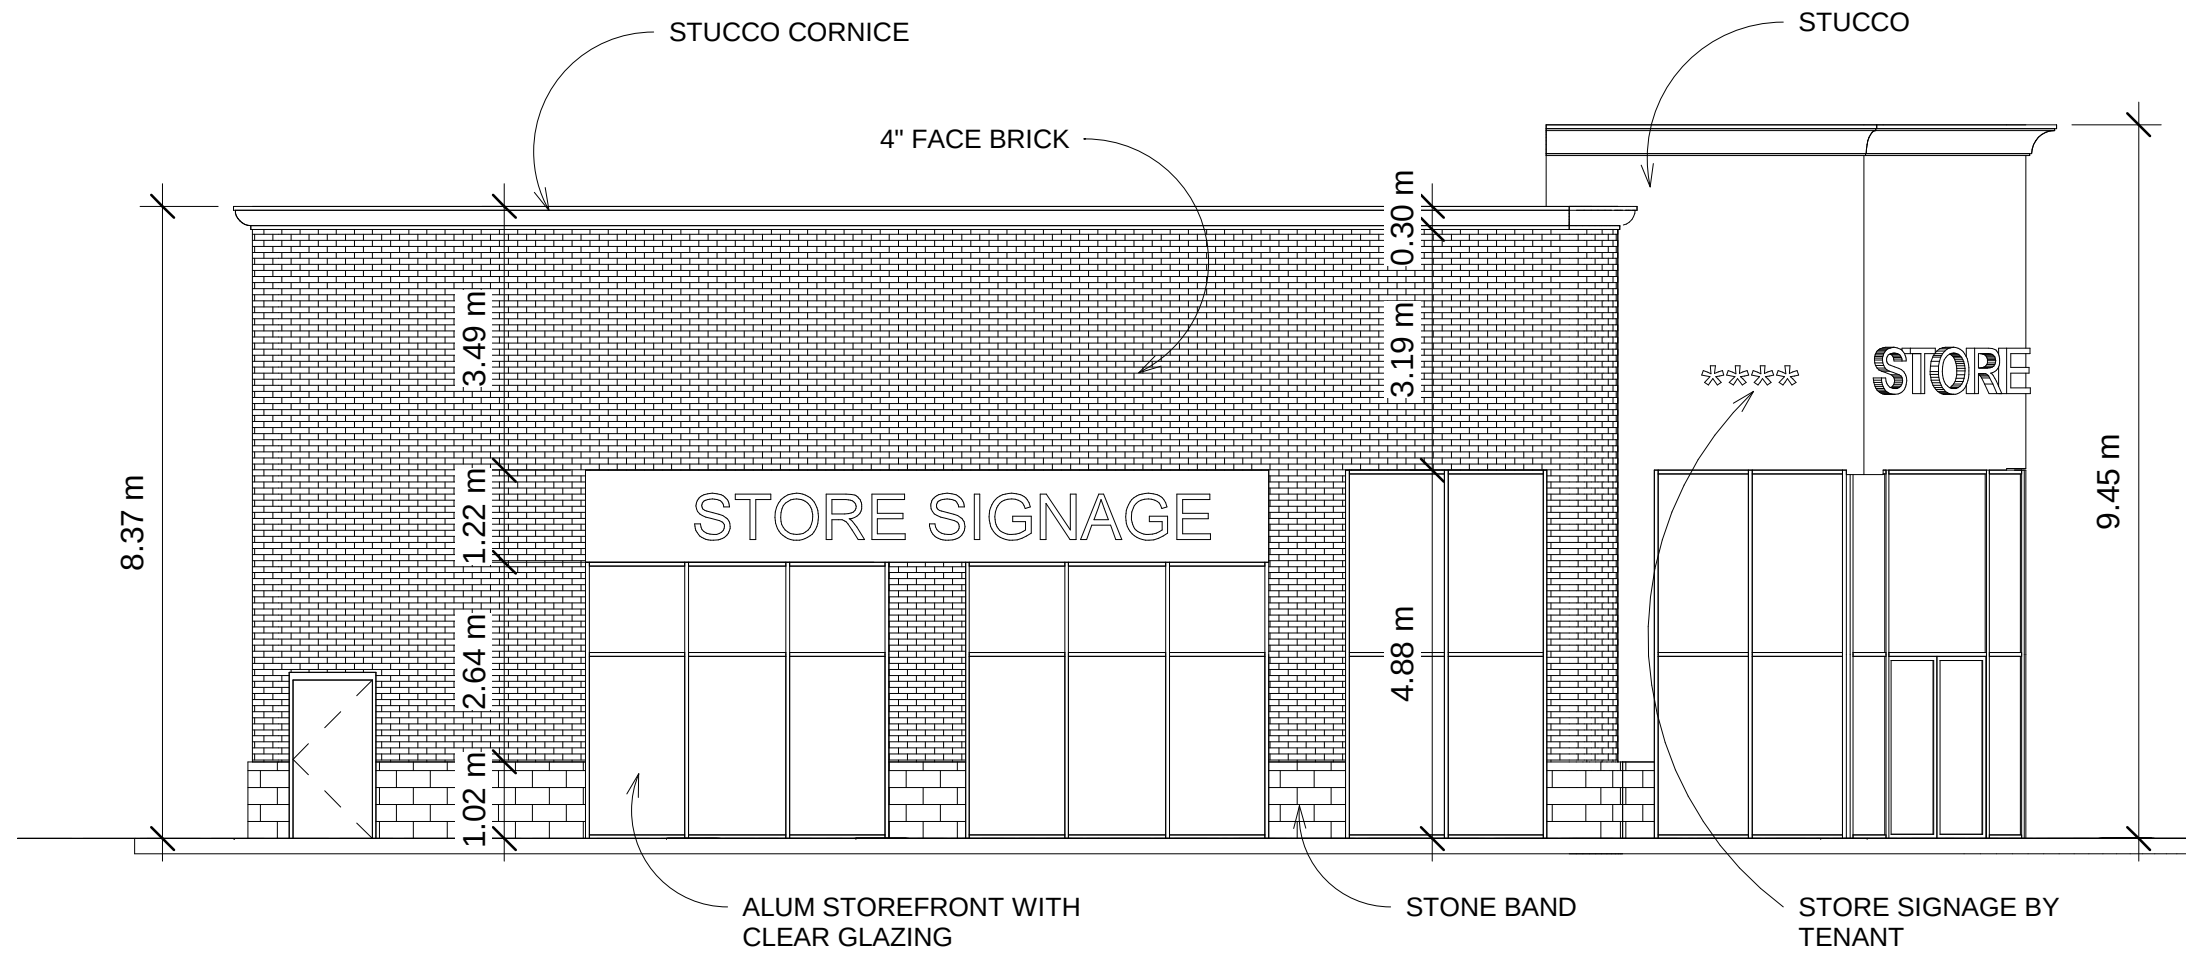

3 SOUTH ELEVATION-PHASE TWO
A403 1 : 100

8			16		
7			15		
6			14		
5			13		
4			12		
3			11		
2			10		
1	07.26.20	SPA	9		
rev.	date	issued for	rev.	date	issued for

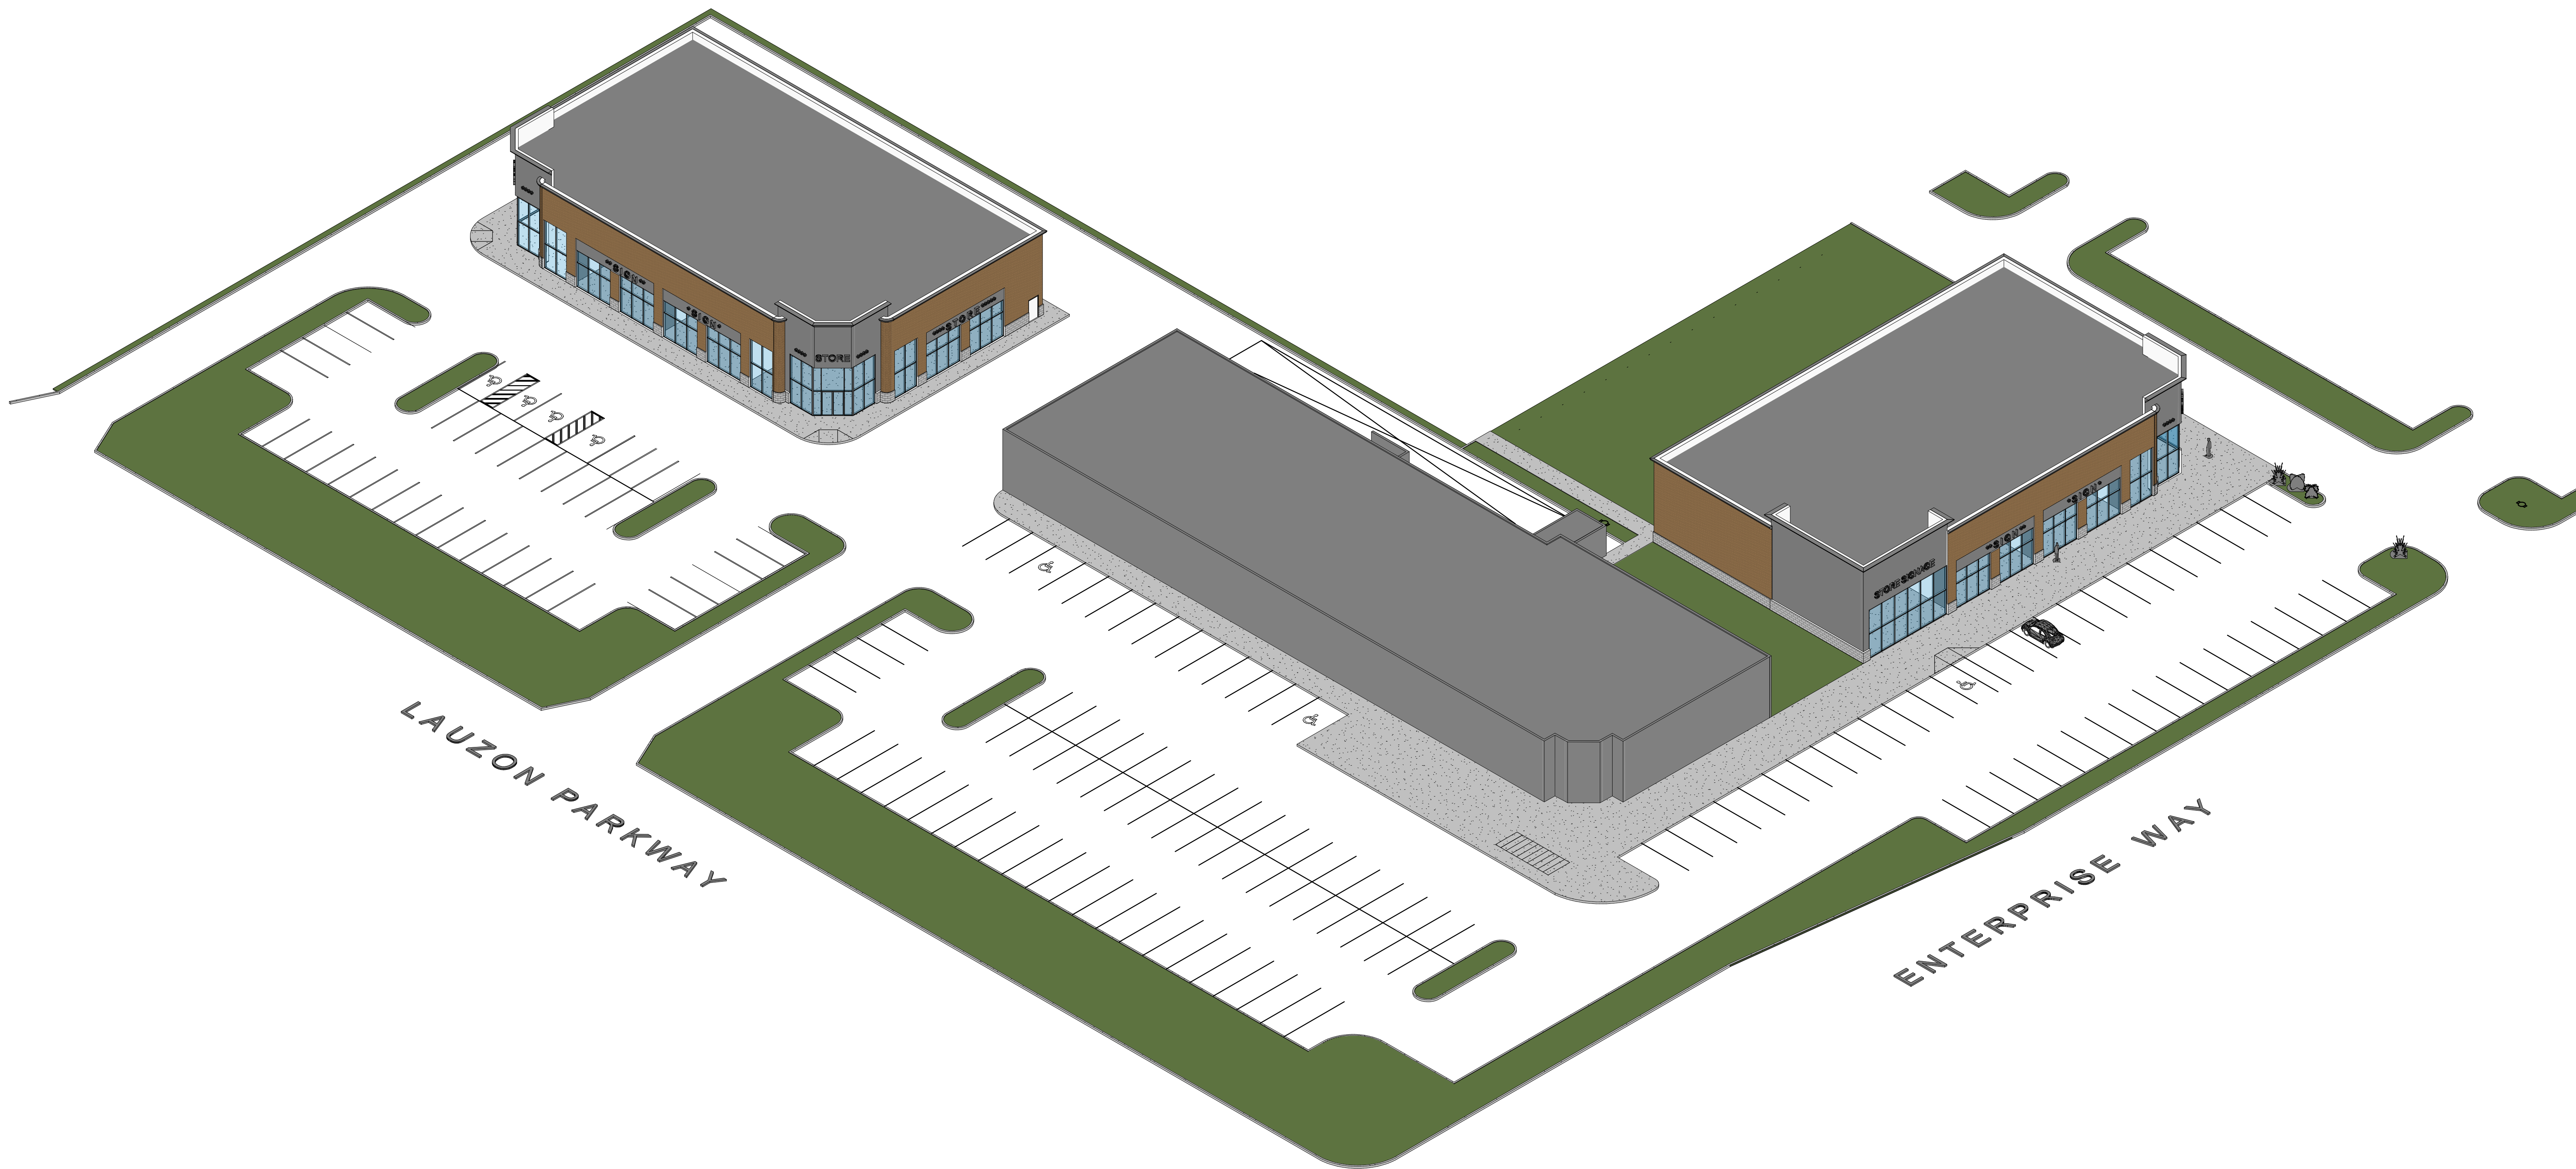

1 OVERALL AERIAL VIEW
A404

8			16		
7			15		
6			14		
5			13		
4			12		
3			11		
2			10		
1	07.26.20	SPA	9		
rev.	date	issued for	rev.	date	issued for