Item	Site Data Matrix						OBC Reference
1	Project Description: NEW TOWNHOUSES 2 AND 3 BEDROOMS UNITS ARE DIVIDED INTO 5 BUILDINGS AS FOLLOWING, BLD. (1): 10 UNITS BLD. (2): 7 UNITS BLD. (3): 10 UNITS BLD. (4): 7 UNITS BLD. (5): 8 UNITS			☒ New ☐ Addition ☐ Alteration ☐ Change of Use			☒ Part 3 ☐ Part 9 ☐ Part 11
2	Zoning Designation:	RESIDENTIAL DISTRICT (RD3.2), S20(1)448					
3	Existing Land Use:	VACATED					
4	Major Occupancy(s):	RESIDENTIAL OCCUPANCY					
5	Building Classification:	Group (c) Division ( ) 3.2.2. (46)* SEE NOTE BELOW					
6	**Site Area**		**Building Area**		**Gross Area**		
	Existing:	10,911 Sq.M.	Existing:	--	Existing:	--	
	Proposed:	--	Proposed:	3,557.2 SQ.M.	Proposed:	6,436 SQ.M.	
	Total:	10,911 Sq.M.	Total:	3,557.2 SQ.M.	Total:	6,436 SQ.M.	
7	**Lot Coverage**		**Minimum Lot Width**		**Building Height**		
	Maximum:	4,910 SQ.M. 45%	Required:	20 M.	Maximum:	18 M.	
	Provided:	3,557 SQ.M. 30.6%	Provided:	33.79 M.	Provided:	10.31 M.	
8	**Minimum Front Yard Depth**		**Minimum Rear yard Depth**		**Minimum Side Yard Depth**		
	Required:	6.0 M.	Required:	6.0 M.	Required:	6.0 M.	
	Provided:	6.0 M.	Provided:	6.0 M.	Provided:	6.0 M.	
9	**Parking**		**Bicycle Spaces**		**Loading Spaces**		
	Use Classification:		Existing:	N/A	Existing:	N/A	
	Existing:	N/A	Proposed:	4	Proposed:	N/A	
	Proposed:	43 + 1 B.F.	Required:	4	Required:	N/A	
	Required:	44	Total:	4	Total:	N/A	
	Total:	44					
10	**Landscaped Area**		**Curbing Length**		**Screening Fence Length**		
	Existing:	N/A	Existing:	N/A	Existing:	N/A	
	Proposed:	7,353.8 SQ.M.	Proposed:	630.20 M.	Proposed:	259.61 M.	
	Total:	7,353.8 SQ.M.	Total:	630.20 M.	Total:	259.61 M.	

(*) NOTE: BUILDING -1 IS FACING 2 STREETS BUILDINGS (2&3&4 AND 5) ARE FACING 1 STREET

Should archaeological deposits be found during construction activities, all work in the area must stop immediately and the City's Manager of Cultural Affairs and the Ontario Ministry of Tourism, Culture and Sport must be notified, and clearance given by the Ministry.

In the event that human remains are encountered during construction, all work in that area must be stopped immediately and the site secured. The local police or coroner must be contacted to determine whether or not the skeletal remains are human, and whether the remains constitute a part of a crime scene. The Ontario Ministry of Tourism, Culture and Sport and the Registrar of the Cemeteries Regulation Unit of the Ministry of Consumer Services must then be notified, and clearance be given by the Ministry of Tourism, Culture and Sport.

A building shall not be located beneath existing above ground electrical conductors. Where a building is to be constructed in proximity to above ground electrical conductors, horizontal clearances between buildings and conductors shall comply with Subsection 3.1.19. of the Ontario Building Code.

SITE MATRIX
SCALE: 1" = 20'-0"

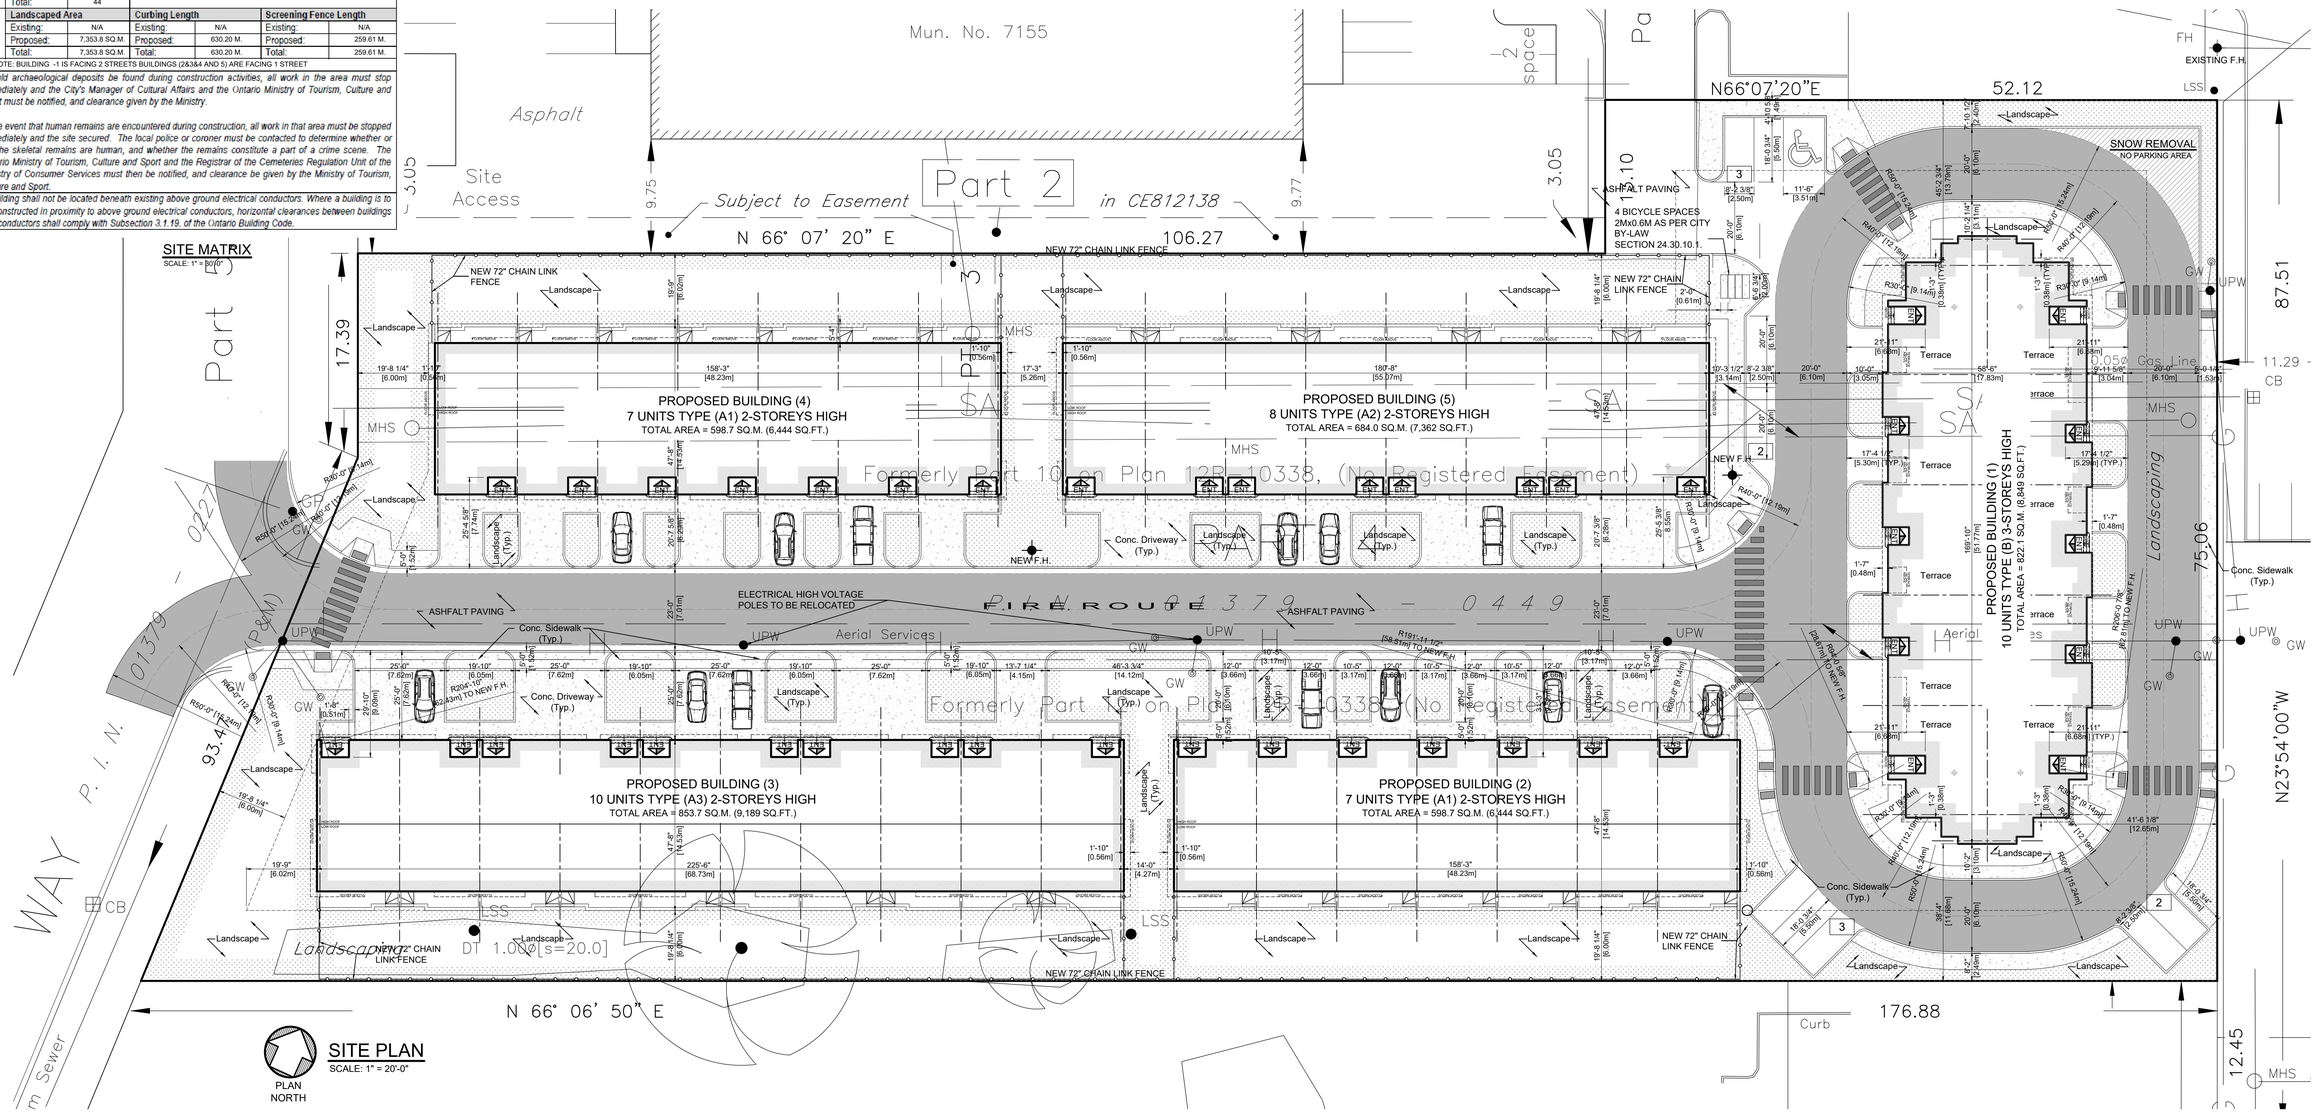

SITE PLAN
SCALE: 1" = 20'-0"

ALL DRAWINGS, SPECIFICATIONS AND OTHER RELATED DOCUMENTS ARE THE COPYRIGHT PROPERTY OF THE **CONSULTANT** AND SHALL BE RETURNED UPON REQUEST.

REPRODUCTION OF DRAWINGS AND RELATED DOCUMENTS, IN WHOLE OR IN PART, IS FORBIDDEN WITHOUT THE WRITTEN PERMISSION OF THE **CONSULTANT.**

THE CONTRACTOR SHALL CHECK AND VERIFY ALL PERTINENT DIMENSIONS AND REPORT ANY DISCREPANCIES TO THE **CONSULTANT** BEFORE PROCEEDING WITH THE WORK.

THIS DRAWING SHALL NOT BE USED FOR CONSTRUCTION UNLESS IT IS COUNTERSIGNED BY THE **CONSULTANT.**

THIS DRAWING IS **NOT** TO BE SCALED.
USE FIGURED DIMENSIONS ONLY.

HANNA, GHOBRIAL AND ASSOCIATES LTD.
engineering
architecture
3100 Temple Drive, Suite 100
Windsor, ON N8W 5J6
(519) 945-7373 FAX.-5636

Rev.:	Date:	Issued For:	Rev.:	Date:	Issued For:
9			18		
8			17		
7			16		
6			15		
5			14		
4			13		
3			12		
2			11		
1	JAN 18-2023	REZONING	10		

Date:	OCTOBER 2021
Scale:	AS SHOWN
Drawn By:	
Checked By:	

Project:
PROPOSED NEW ENTERPRISE TOWNHOUSE BUILDINGS
3385 FOREST GLADE DRIVE WINDSOR, ONTARIO

Project No.: 21-0431

Sheet Title: SITE PLAN

Sheet No.: A-00

Plot Scale:
Updated:
File Name: