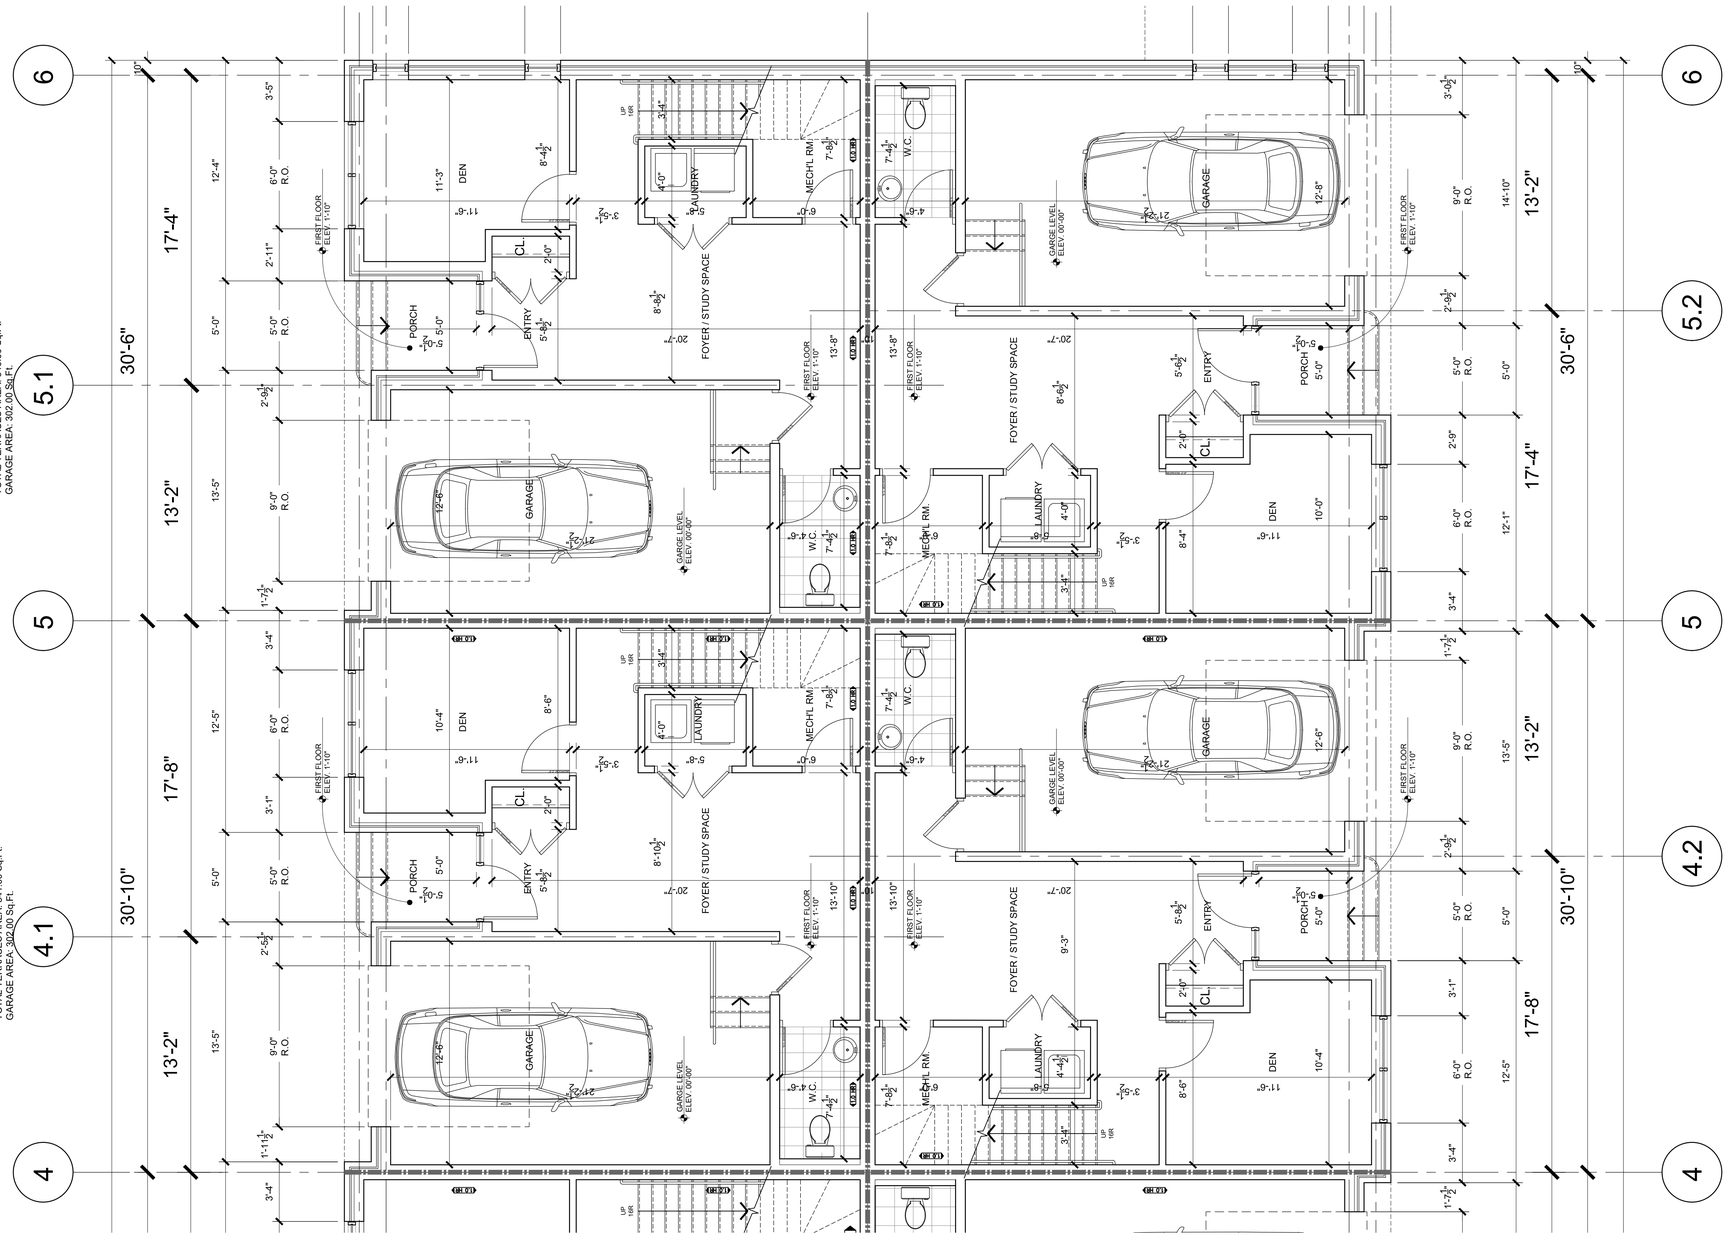

HANNA, GHOBRIAL AND ASSOCIATES LTD.
engineering
architecture
3100 Temple Drive, Suite 100
Windsor, ON N8W 5J6
(519) 945-7373 FAX.-5636

ALL DRAWINGS, SPECIFICATIONS AND OTHER RELATED DOCUMENTS ARE THE COPYRIGHT PROPERTY OF THE **CONSULTANT** AND SHALL BE RETURNED UPON REQUEST.

REPRODUCTION OF DRAWINGS AND RELATED DOCUMENTS, IN WHOLE OR IN PART, IS FORBIDDEN WITHOUT THE WRITTEN PERMISSION OF THE **CONSULTANT.**

THE CONTRACTOR SHALL CHECK AND VERIFY ALL PERTINENT DIMENSIONS AND REPORT ANY DISCREPANCIES TO THE **CONSULTANT** BEFORE PROCEEDING WITH THE WORK.

THIS DRAWING SHALL NOT BE USED FOR CONSTRUCTION UNLESS IT IS COUNTERSIGNED BY THE **CONSULTANT.**

THIS DRAWING IS **NOT** TO BE SCALED.
USE FIGURED DIMENSIONS ONLY.

Rev.:	Date:	Issued For:	Rev.:	Date:	Issued For:
9			18		
8			17		
7			16		
6			15		
5			14		
4			13		
3			12		
2			11		
1			10		

Date:	OCTOBER 2021
Scale:	AS SHOWN
Drawn By:	
Checked By:	

Project:
PROPOSED NEW
ENTERPRISE TOWNHOUSE BUILDINGS
3385 FOREST GLADE DRIVE WINDSOR ONTARIO

Project No.: 21-0431

FIRST FLOOR PLAN (CLUSTER-B)

A-201- B1

Pltd Scale:
Updated:
File Name: