Item	Site Data Matrix						OBC Reference
1	Project Description: NEW BUILDING ADDED TO AN EXISTING SHOPPING CENTER 1 STOREY, LCBO.				☒ New ☐ Addition ☐ Alteration ☐ Change of Use		☒ Part 3 ☐ Part 9 ☐ Part 11
2	Zoning Designation:		CH-8), SHOPPING CENTER-RETAIL STORE				
3	Existing Land Use:		PARKING LOT				
4	Major Occupancy(s):		MERCANTILE OCCUPANCY				
5	Building Classification:		Group (E) Division ( ) 3.2.2. (59)				
6	**Site Area**		**Building Area**		**Gross Area**		
	Existing:	50,707.3 m² / 545,908.8 ft²	Existing:	17,138.6 m² / 184,479.40 ft²	Existing:	17,138.6 m² / 184,479.40 ft²	
	Proposed:	--	Proposed:	570 m² / 6,135 ft²	Proposed:	6,135 m² / 570 ft²	
	Total:	50,707.3 m² / 545,808.8 ft²	Total:	17,708 m² / 190,613.40 ft²	Total:	17,708 m² / 190,613.40 ft²	
7	**Lot Coverage**		**Minimum Lot Width**		**Building Height**		
	Maximum:	25,353.6 m² / 272,904.4 ft² 50%	Required:	--	Maximum:	7.5m (24-6")	
	Provided:	17,708 m² / 190,613.4 ft² 34.9%	Provided:	173.7m (569'-8")	Provided:	6.3m (20'-8")	
8	**Minimum Front Yard Depth**		**Minimum Rear yard Depth**		**Minimum Side Yard Depth**		
	Required:	0.0m (0'-0")	Required:	0.0m (0'-0")	Required:	11.6m (38'-1)	
	Provided:	0.6m (1'-11.5")	Provided:	147.9m (485.26')	Provided:	111.8m (366.68')	
9	**Parking**		**Bicycle Spaces**		**Loading Spaces**		
	Use Classification:		Existing:	N/A	Existing:	2	
	Existing:	823	Proposed:	2	Proposed:	1	
	Proposed:	756	Required:	N/A	Required:	N/A	
	Required:	23 (1 CAR/ 25 m²)	Total:	2	Total:	3	
	Total:	756					
10	**Landscaped Area**		**Curbing Length**		**Screening Fence Length**		
	Existing:	33,568.67 m² / 361,330.2 ft²	Existing:	To remain (707 m+new) 1,148.3 m / 3,767.4'	Existing:	N/A	
	Proposed:	32,998.67 m² / 355,430.2 ft²	Proposed:	new 116.6 m / 382.6'	Proposed:	9.15 m / 30'-0"	
	Total:	32,998.67 m² / 355,430.2 ft²	Total:	1,264.9 m / 4,150.0'	Total:	9.15 m / 30'-0"	

Should archaeological deposits be found during construction activities, all work in the area must stop immediately and the City's Manager of Cultural Affairs and the Ontario Ministry of Tourism, Culture and Sport must be notified, and clearance given by the Ministry.

In the event that human remains are encountered during construction, all work in that area must be stopped immediately and the site secured. The local police or coroner must be contacted to determine whether or not the skeletal remains are human, and whether the remains constitute a part of a crime scene. The Ontario Ministry of Tourism, Culture and Sport and the Registrar of the Cemeteries Regulation Unit of the Ministry of Consumer Services must then be notified, and clearance be given by the Ministry of Tourism, Culture and Sport.

A building shall not be located beneath existing above ground electrical conductors. Where a building is to be constructed in proximity to above ground electrical conductors, horizontal clearances between buildings and conductors shall comply with Subsection 3.1.19. of the Ontario Building Code.

SITE STATISTICS

PARKING	EXISTING PARKING	AREA (SQ.M.)	ZONING FORMULA	REQUIRED	PROVIDED/ PROPOSED
BRICK STUCCO BUILDING					
BRICK & STUCCO BUILDING					
BRICK & FRAME BUILDING					
TOTAL		6,381.63	1 CAR PER/ 30 m²	212.7	219
WALMART		10,757.00	1 CAR PER/ 30 m²	358.6	494
LCBO		570.00	1 CAR PER/ 25 m²	22.8	43
TOTAL	823 CARS			595 CARS	756 CARS INCL. 16 B.F. PARKING [6 TYPE 'A', 6 TYPE 'B', AND 4 SINGLE STANDARD]

NOTE:

ALL SURVEY INFO. BY
BRIAN COAD OF VERHAEGEN STUBBERFIELD
WORK ORDER: 4-24532-X01
PLAN FILE No: J- 402

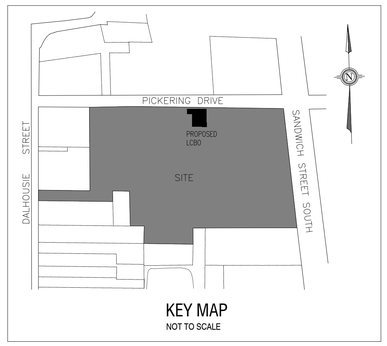

KEY MAP
NOT TO SCALE

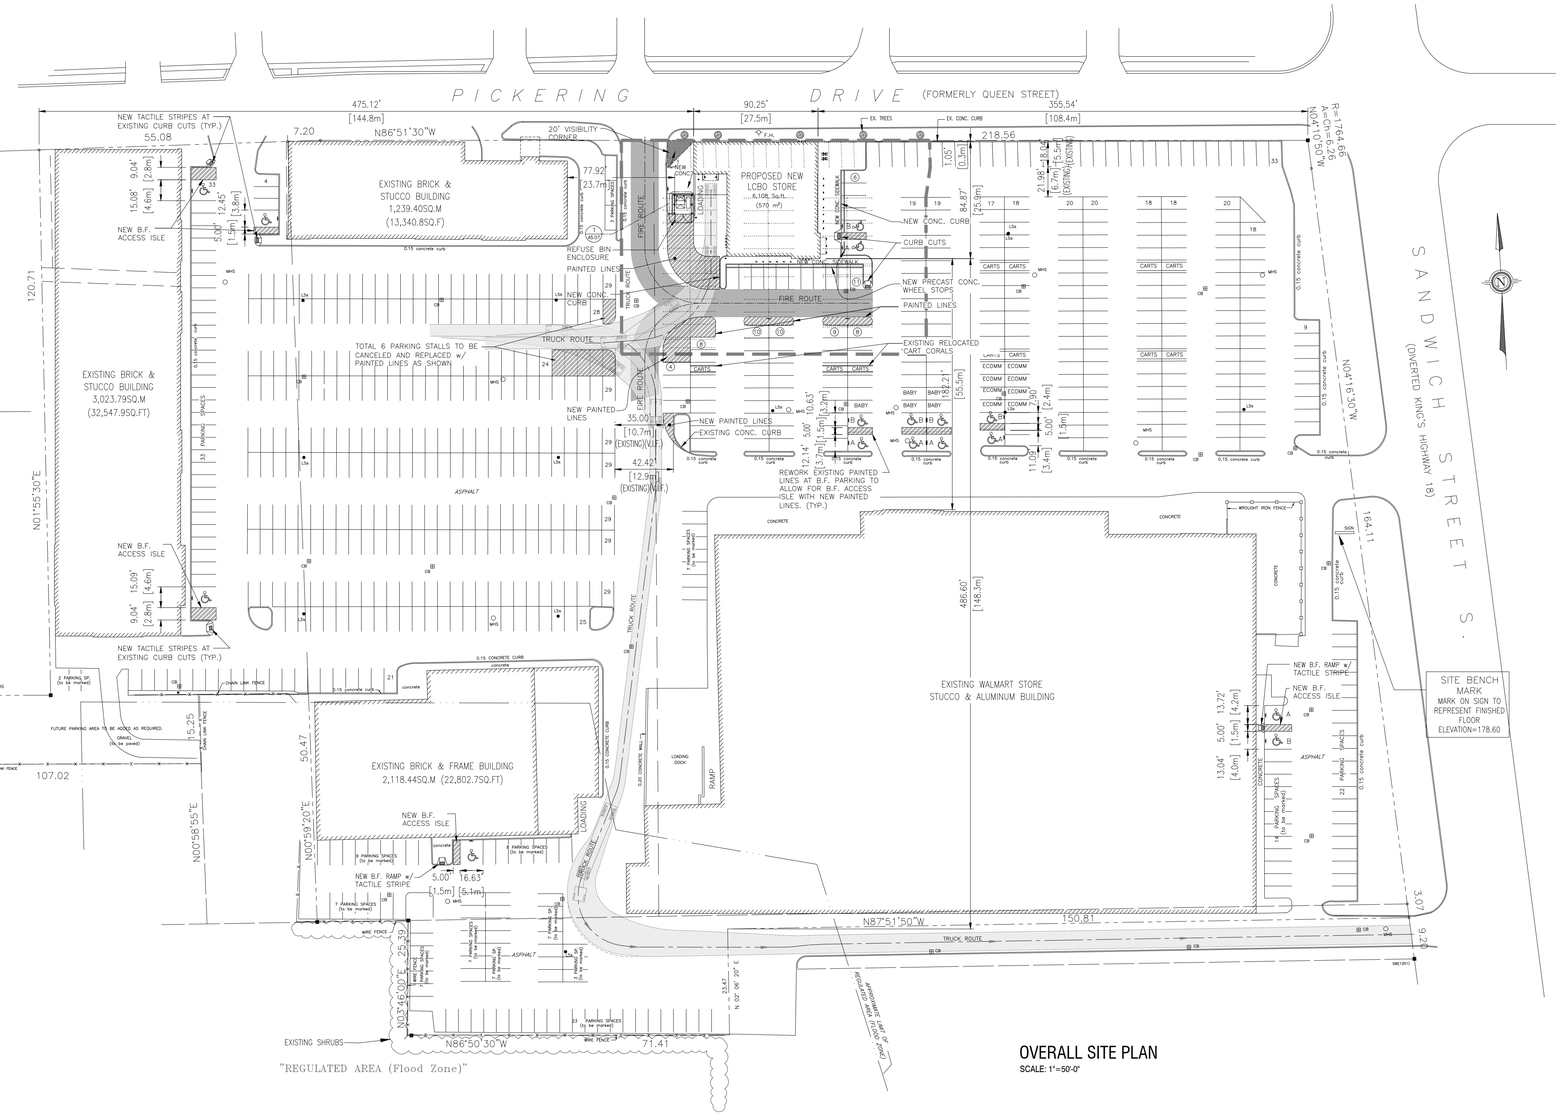

OVERALL SITE PLAN
SCALE: 1"=50'-0"

HANNA, GHOBRIAL AND ASSOCIATES LTD.
engineering
architecture
3100 Temple Drive, Suite 100
Windsor, ON N8W 5J6
(519) 945-7373 FAX.-5636

This drawing shall not be used for construction unless it is countersigned by the CONSULTANT.

ALL DRAWINGS, SPECIFICATIONS AND OTHER RELATED DOCUMENTS ARE THE COPYRIGHT PROPERTY OF THE **CONSULTANT** AND SHALL BE RETURNED UPON REQUEST.
REPRODUCTION OF DRAWINGS AND RELATED DOCUMENTS, IN WHOLE OR IN PART, IS FORBIDDEN WITHOUT THE WRITTEN PERMISSION OF THE **CONSULTANT.**
THE CONTRACTOR SHALL CHECK AND VERIFY ALL PERTINENT DIMENSIONS AND REPORT ANY DISCREPANCIES TO THE **CONSULTANT** BEFORE PROCEEDING WITH THE WORK.
THIS DRAWING SHALL NOT BE USED FOR CONSTRUCTION UNLESS IT IS COUNTERSIGNED BY THE **CONSULTANT.**
THIS DRAWING IS **NOT** TO BE SCALED.
USE FIGURED DIMENSIONS ONLY.

No.	Date: YY/MM/DD	Issued For:
20		
19		
18		
17		
16		
15		
14		
13		
12	2023/11/16	REV. PER LCBO[2] & WMRT[3]
11	2023/11/14	SPA- REV. MEZZ. FIRE RATING
10	2023/10/19	BUILDING PERMIT
9	2023/09/28	LCBO REVIEW
8	2023/09/26	SPA- REV. TRUCK ROUTE
7	2023/09/12	REVIEW BY WALMART
6	2023/09/06	SITE PLAN APPLICATION
5	2023/08/15	PHOTOMETRIC ANALYSIS
4	2023/08/03	CLIENT REVIEW
3	2023/07/31	PRE-SUBMITTAL APPLIC.
2	2023/07/26	CLIENT REVIEW
1	2023/06/21	SITE PLAN APPLICATION

Date:	JUNE 2023
Drawn By:	H.R.
Checked By:	E.B.K.

Client:
Joseph B. Mikhail
Mikhail Holdings Ltd.
100 Ouellette Ave., Suite 700
Windsor, ON. N9A 6T3

Project Title:

LCBO

NEW
LCBO STORE

Address: 400 SANDWICH STREET
AMHERSTBURG, ONTARIO N9V 3L4

Project No.:
22-0445

Sheet Title:
OVERALL SITE PLAN

Sheet No.:
SP-1

FILE LOCATION: Y:\22-0445 New LCBO Amherstburg_400 Sandwich Street_Joe Mikhail\Construction Documents_LP-1 Site Plans & Details.dwg