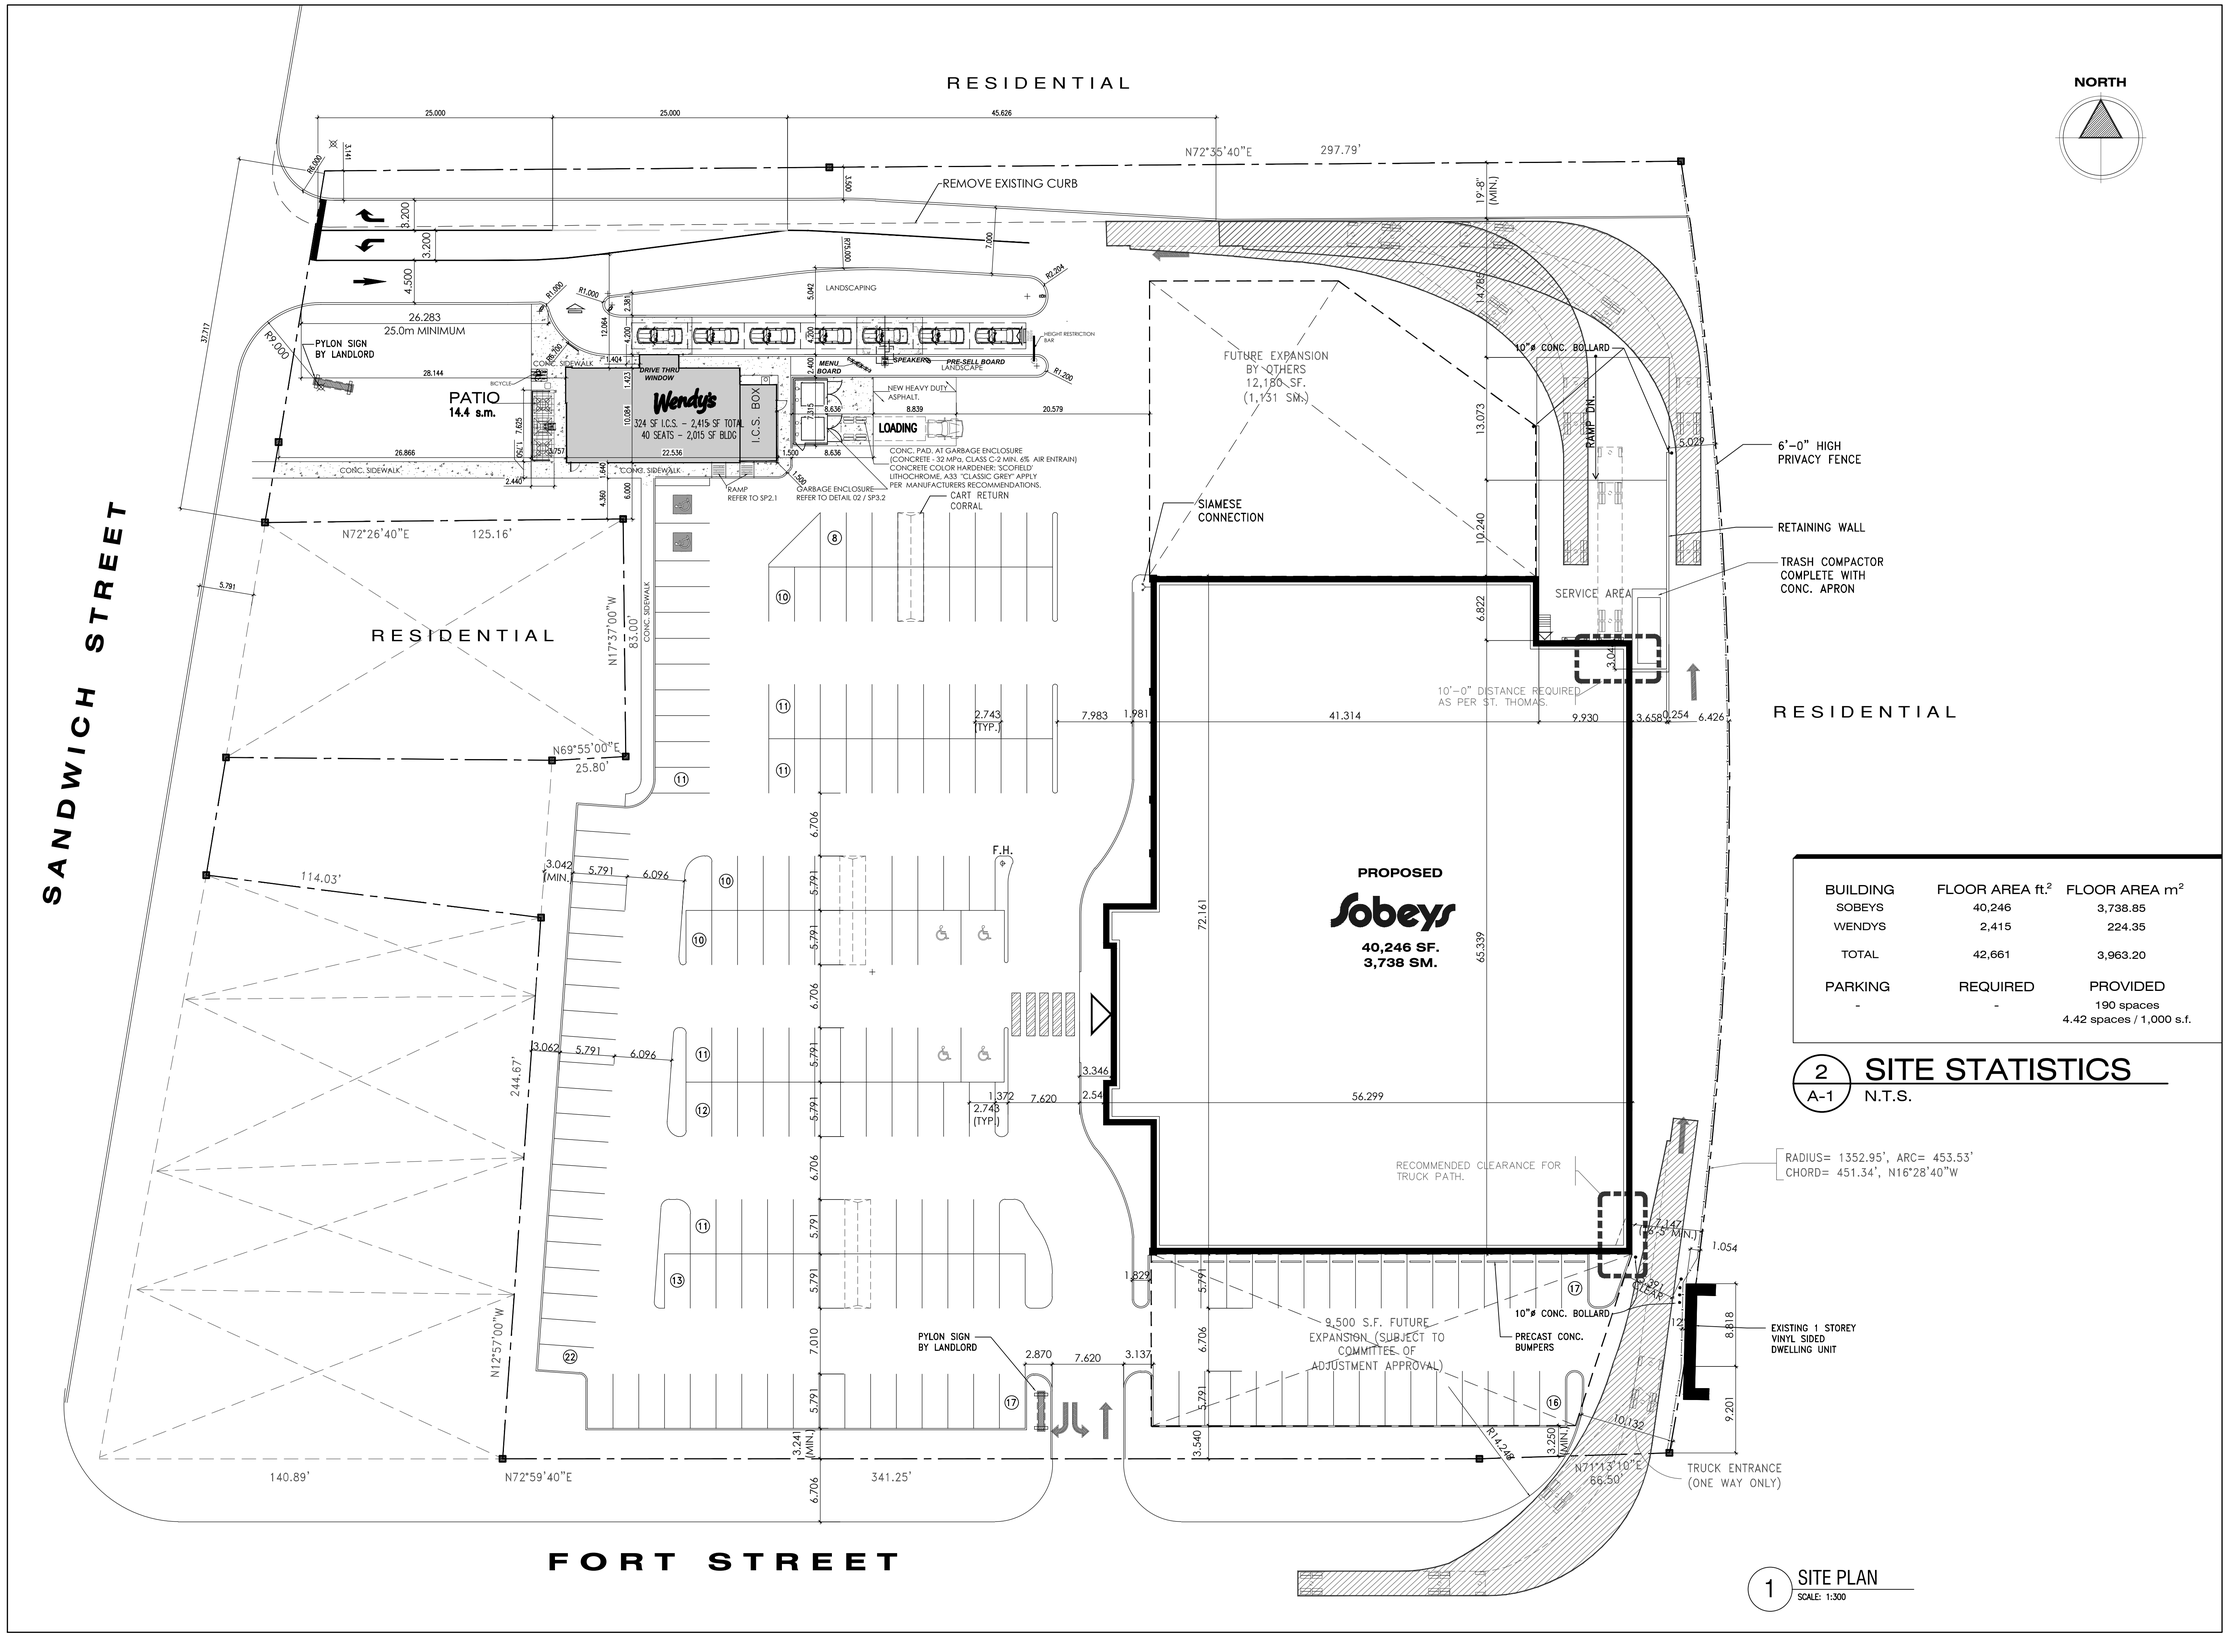

1 SITE PLAN
SCALE: 1:300

BUILDING	FLOOR AREA ft.^{2}	FLOOR AREA m^2
SOBEYS	40,246	3,738.85
WENDYS	2,415	224.35
TOTAL	42,661	3,963.20
PARKING	REQUIRED	PROVIDED
-	-	190 spaces 4.42 spaces / 1,000 s.f.

2 A-1 SITE STATISTICS
N.T.S.

SITE NUMBER:	06610
BASE MODEL:	SMART 40 - SQE
ASSET TYPE:	FRANCHISEE
CLASSIFICATION:	NEW
OWNER:	WENDYS
BASE VERSION:	2017
UPGRADE CLASSIFICATION:	FRAN NEW FLAG
PROJECT YEAR:	2018
FURNITURE PACKAGE:	2017
DESIGN BULLETINS:	-

1. THIS DRAWING IS THE PROPERTY OF THE ARCHITECT AND MAY NOT BE USED IN WHOLE OR IN PART FOR ANY PROJECT OTHER THAN THAT DESIGNATED HEREIN.
2. DO NOT SCALE DRAWINGS.
3. CONTRACTOR TO VERIFY JOB SITE AND DRAWING DIMENSIONS AND CONDITIONS. REPORT ANY AND ALL DISCREPANCIES TO THE ARCHITECT PRIOR TO CONTSTRUCTION.
4. ALL WORK MUST CONFORM TO THE LATEST LOCAL BUILDING CODE, LOCAL BY-LAWS AND NFPA 96.
5. THESE DRAWINGS ARE PROTECTED BY COPYRIGHT
© NAYLOR ARCHITECT INC.

ISSUED:

TO	DATE	DESCRIPTION
CLIENT	June 18/18	FOR REVIEW
CITY	June 01/18	BUILDING PERMIT
CITY	Mar 28/19	SITE PLAN - BUILDING PERMIT
G.C.	May 17/19	FOR TENDER

Wendy's
STORE #06610

SEAL: ONTARIO ASSOCIATION OF ARCHITECTS
CHRISTOPHER J. NAYLOR
LICENCE 4938

NAYLOR ARCHITECT INC.
2800 JOHN STREET UNIT 22
MARKHAM, ONTARIO
L3R 0E2
TEL: 905.470.2463
FAX: 905.470.7713
E-MAIL: INFO@NAYLORARCHITECT.COM

PROJECT TYPE: NEW BUILD

WENDY'S RESTAURANT STORE #06610

83 SANDWICH STREET S
AMHERSTBURG, ONTARIO

DRAWN: J.O.	DATE: MARCH. 2019
CHECKED BY: CN	
SCALE: AS NOTED	PROJECT NO.: 18162
SHEET TITLE: SITE PLAN	
REVISION NO.:	SHEET NO.: SP1.1