

**83 SANDWICH STREET BUILDING
ADDITION**

AMHERSTBURG, ONTARIO

PROJECT NUMBER: 17-0339

PROJECT TEAM

OWNER:

MIKHAIL HOLDINGS LIMITED
100 Ouellette Avenue
Windsor, Ont
Tel: (519) 944-2929

ARCHITECT:

HGA, Engineering
3100 Temple Drive, Suite 100
Windsor, ON N8W 5J6
Tel: 519-945-7373
Fax: 519-945-5636

CIVIL ENGINEER

Haddad Morgan & Associates LTD.
24 Shepherd St., E
Windsor, ONN8X 2J8
Tel: 519-973-1177

STRUCTURAL ENGINEER

HGA, Engineering
3100 Temple Drive, Suite 100
Windsor, ON N8W 5J6
Tel: 519-945-7373
Fax: 519-945-5636

MECHANICAL & ELECTRICAL ENGINEER

Field Craft Engineering Limited.
72 Sandwich St., N.
Amherstburg, ON N9V 2T7
Tel: 519-726-6400
Fax: 519-726-5028


GENERAL NOTES

1. ALL CONSTRUCTION WORK SHALL COMPLY WITH CODES CURRENTLY IN EFFECT IN THE CITY OF AMHERSTBURG
2. THE GENERAL CONTRACTOR IS RESPONSIBLE FOR SITE INSPECTION PRIOR TO BEGINNING OF WORK AND IS RESPONSIBLE TO FIELD VERIFY ALL DIMENSIONS AND EXISTING CONDITIONS. NOTIFY THE ARCHITECT OF ANY DISCREPANCIES.
3. DO NOT SCALE DRAWINGS. NUMERICAL DIMENSIONS SHOWN ON PLANS SHALL TAKE PRECEDENCE.
4. DOCUMENTATION: THE CONTRACTOR SHALL KEEP A RECORD OF ALL CHANGES TO THE CONTRACT DOCUMENTS. THE GENERAL CONTRACTOR SHALL NEATLY AND CORRECTLY ENTER IN COLOR PENCIL ANY CHANGES ON THE DRAWINGS AFFECTED AND SHALL KEEP THE DRAWINGS AVAILABLE FOR INSPECTION. AT THE COMPLETION OF THE JOB AND BEFORE FINAL APPROVAL, THE GENERAL CONTRACTOR SHALL CERTIFY TO THE ACCURACY OF ALL APPROVED CHANGES AND CONFIRM IN WRITING THAT ALL WORK IS COMPLETED ACCORDING TO THE CONTRACT DOCUMENTS. THIS SET OF RECORDED CHANGES SHALL BE DELIVERED TO THE ARCHITECT AND SHALL BE CONSIDERED 'AS-BUILT' DRAWINGS.
5. AT THE COMPLETION OF THE GENERAL CONTRACTOR'S AND EACH SUBCONTRACTOR'S DAILY WORK, THEY SHALL BE RESPONSIBLE FOR THE CLEAN-UP AND REMOVAL OF ALL RUBBISH AND CONSTRUCTION DEBRIS. GENERAL CONTRACTOR SHALL BE RESPONSIBLE FOR THE LEGAL DISPOSAL OF ALL SUCH RUBBISH AND CONSTRUCTION DEBRIS.
6. NO SUBSTITUTIONS OF SPECIFIED MATERIALS OR EQUIPMENT WILL BE ACCEPTED UNLESS QUOTED IN THE PROPOSAL OR SUBSEQUENTLY APPROVED BY THE ARCHITECT.
7. PLANS THAT DO NOT INDICATE THAT THEY HAVE BEEN APPROVED FOR CONSTRUCTION ARE INCOMPLETE AND ARE NOT TO BE USED FOR CONSTRUCTION.

ABBREVIATIONS

ACT	ACOUSTIC CEILING TILE	DBL	DOUBLE	MECH	MECHANICAL
ADD	ADDENDUM	DN	DOWN	MFR	MANUFACTURER
AFF	ABOVE FINISH FLOOR	DTL	DETAIL	MIN	MINIMUM
ALUM	ALUMINUM	DWG	DRAWING	MISC	MISCELLANEOUS
ANOD	ANODIZED	EF	EXHAUST FAN	MTL	METAL
APPROX	APPROXIMATE	EJ	EXHAUST JOINT	MRT	MOISTURE RESISTANT
ARCH	ARCHITECTURAL	EFS	EXTERIOR INSULATION FINISH SYSTEM	N/A	NOT APPLICABLE
&	AND	EJ	EXPANSION JOINT	NIC	NOT IN CONTRACT
@	AT	ELEV	ELEVATION	NO	NUMBER
L	ANGLE	ELEC	ELECTRICAL	NTS	NOT TO SCALE
BD	BOARD	ENCL	ENCLOSURE	OPP	OPPOSITE
BFF	BELOW FINISH FLOOR	EQUIP	EQUIPMENT	PLUMB	PLUMBING
BLK	BLOCK, BLOCKING	EXIST	EXISTING	QTY	QUANTITY
BLDG	BUILDING	FIN	FINISH	PC	PRE-CAST
BOS	BOTTOM OF STEEL	FL	FLOOR	RC	RAIN CONDUCTOR
BULL	BULLETIN	FT	FOOT	REQ	REQUIRED
CFT	CUBIC FOOT	FV	FIELD VERIFY	SCHED	SCHEDULE
C I P	CAST IN PLACE	GA	GAUGE	SF	SQUARE FOOT
CJ	CONTROL JOINT	GALV	GALVANIZED	STD	STANDARD
CL	CENTERLINE	H C	HOLLOW CORE	STL	STEEL
CLG	CEILING	INFO	INFORMATION	T	TREAD
CO	CLEAN OUT	INSUL	INSULATION	T&G	TONGUE AND GROOVE
COL	COLUMN	LAV	LAVATORY	TEMP	TEMPORARY
CONC	CONCRETE	L.W.	LIGHT WEIGHT	TRD	TRIM
CONT	CONTINUOUS	MATL	MATERIAL	W/	WITH
CONST	CONSTRUCTION	MAX	MAXIMUM	W/O	WITHOUT
				WD	WOOD

GRAPHIC SYMBOLS

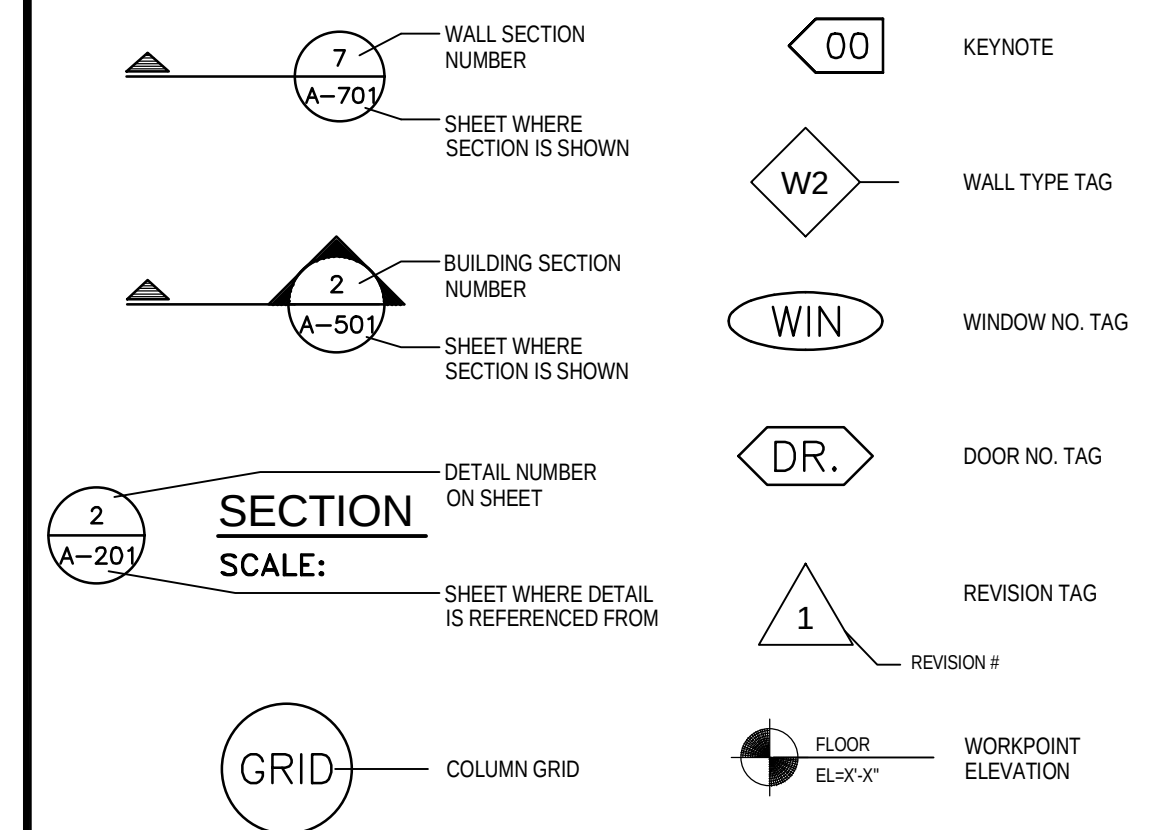


INDEX OF DRAWINGS

[illegible]

83 SANDWICH STREET
AMHERSTBURG, ONT.
O.B.C. (2012-Reg. 232/12) DATA MATRIX - PART 3 & 9 MODEL

ITEM	ONTARIO BUILDING CODE DATA MATRIX PARTS 3 & 9				ONTARIO BUILDING CODE 2006 REFERENCE			
1.	PROJECT DESCRIPTION	☐ NEW ☐ ADDITION ☐ CHANGE OF USE ☐ ALTERATION	☒ DIVISION B3	☐ DIVISION B9				
2.	MAJOR OCCUPANCY(S)	MERCANTILE (E)			B3.1.2.1.(1)			
3.	BUILDING AREA sq.ft./ (sq.m.)	EXISTING (SOBEYS): 3,738sqm (40,248 sq.ft.)	NEW BUILDING EXPANSION 866sqm (9,310 sq.ft.)	TOTAL : 4,584sqm (49,542 sq.ft.)	A1.1.3.2			
4.	BUILDING HEIGHT (NUMBER OF STORIES)	1 STORY			3.2.1.1			
5.	HEIGHT OF BUILDING (m)	4.92m (16'-2") HEIGHT TO TOP OF PARAPET (AT ENTRANCE ONLY) 6.09m (20'-0")			3.2.1.1.(1)			A1.1.2.4
6.	NUMBER OF STREETS / ACCESS ROUTES	TWO			B3.2.2.10			
7.	BUILDING CLASSIFICATION	MERCANTILE (E)			B 3.2.2.59			
8.	FIREWALL REQUIRED REQ'D FRM	☒ YES ☐ 2 HR. ☐ NO ☒ 4 HR.	☐ NO ☒ 4 HR.		B 3.2.2.59, 3.1.10.2(1)			
9.	SPRINKLER SYSTEM REQUIRED	☐ ENTIRE BUILDING ☐ BASEMENT ONLY ☐ IN LIEU OF ROOF RATING ☒ NOT REQUIRED	☐ GARBAGE ROOM & CHUTE ☐ TENANT STORAGE ROOMS		B3.2.2.59			B9.10.18.2
10.	STANDPIPE REQUIRED	☐ YES ☒ NO	☒ NO		B3.2.2.59			
11.	FIRE ALARM REQUIRED	☐ YES ☒ NO	☒ NO		B3.2.8.1			
12.	WATER SERVICE / SUPPLY IS ADEQUATE	☒ YES ☐ NO	☐ NO		B3.2.4.1			B9.10.18.2
13.	HIGH BUILDING	☐ YES ☒ NO	☒ NO		B3.2.6			
14.	PERMITTED CONSTRUCTION ACTUAL CONSTRUCTION	☐ COMBUSTIBLE ☐ COMBUSTIBLE	☐ NON-COMBUSTIBLE ☐ NON-COMBUSTIBLE	☒ BOTH ☒ BOTH	B3.2.2.59			
15.	MEZZANINE(S) AREA (sq.m.)	N/A						
16.	OCCUPANT LOAD BASED ON BARRIER FREE DESIGN	☒ BASED ON DESIGN: 41 OCCUPANTS (9 OCCUPANTS EACH UNIT (STORE) + 5 FOR UNIT 5) ☐ YES ☐ NO (EXPLAIN)			B3.1.17.2			B9.9.1.3
17.	HAZARDOUS SUBSTANCES	☐ YES ☒ NO	☒ NO (EXPLAIN)		B3.8			B9.5.2
18.	REQUIRED FIRE RESISTANCE RATING (FRR) - HORIZONTAL ASSEMBLIES AND SUPPORTS	FRR OF HORIZONTAL ASSEMBLIES			B3.3.1.2.(1) & B3.3.1.19(1)			
19.		.1 FLOORS	N/A		B3.2.2.59			B9.10.8
20.		.2 ROOF	NOT REQUIRED		B3.2.2.59			
21.		.3 MEZZANINE	N/A		-			
22.		FRR OF SUPPORTING ASSEMBLIES						
23.		.4 FLOOR SUPPORTS	N/A		B3.2.2.59			
24.		.5 ROOF SUPPORTS	NOT REQUIRED		B3.2.2.59			
25.		.6 MEZZANINE SUPPORTS	N/A		-			
26.	SPATIAL SEPARATION - GROUP "E"							
27.	WALLS BETWEEN RETAIL SPACES (1 HOUR)				B3.3.1.1			

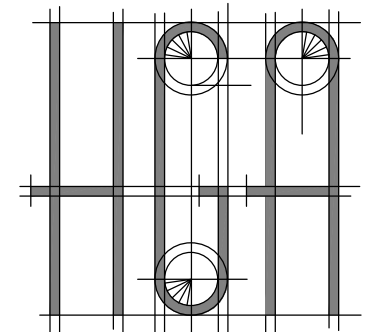



HANNA, GHOBRIAL
AND ASSOCIATES LTD.
engineering
3100 Temple Drive
Windsor, ON N8W 5J6
(519) 945-7373 FAX..5636



12		
11		
10		
9		
8		
7		
6		
5		
4		
3		
2	22/03/31	REV. PER CITY COMMENTS
1	22/02/08	FOR PERMIT
No.	Date: YY/MM/DD	Issued For:
Date:		
Drawn By:		
Checked By:		
Project Title:		

Drawing No.:


G-0

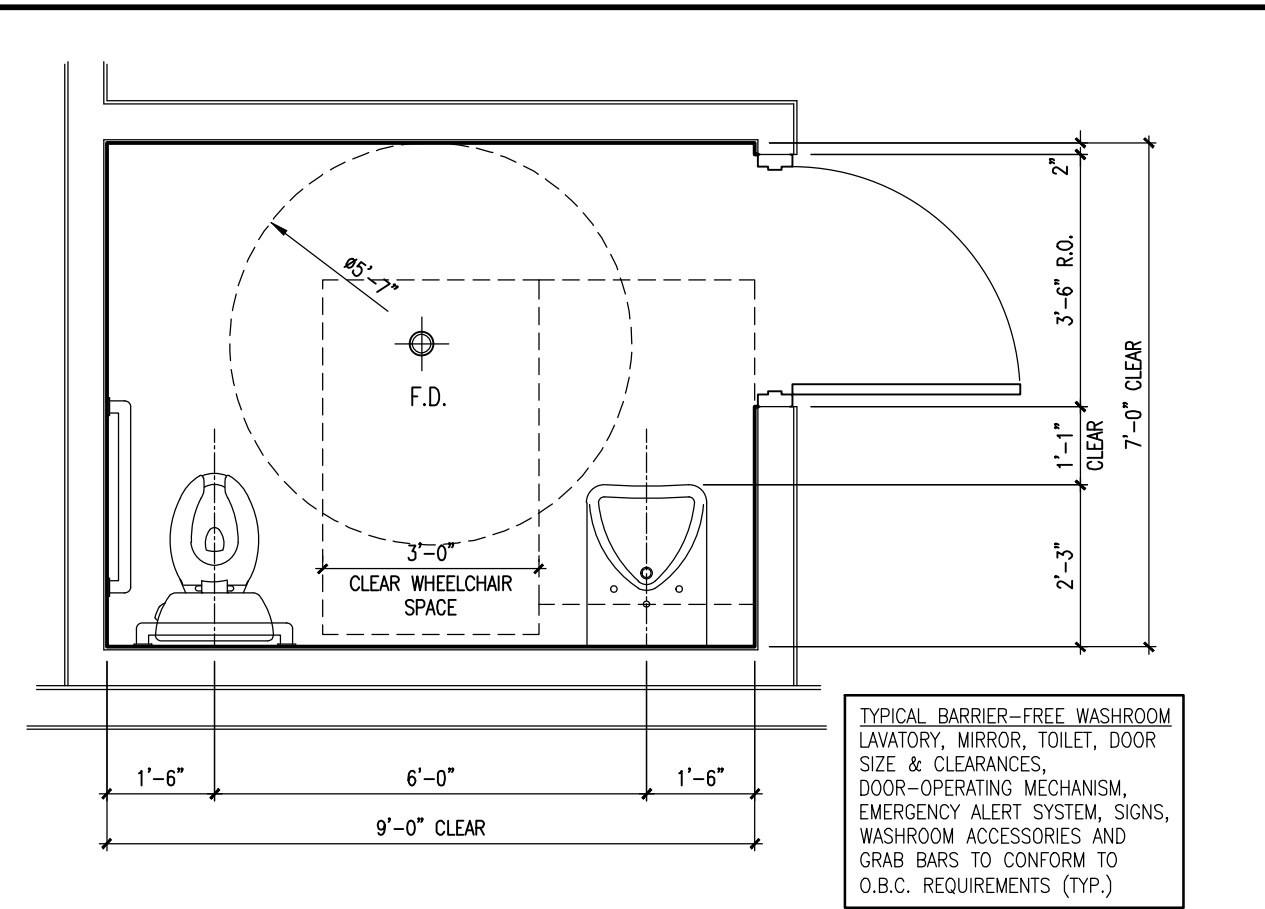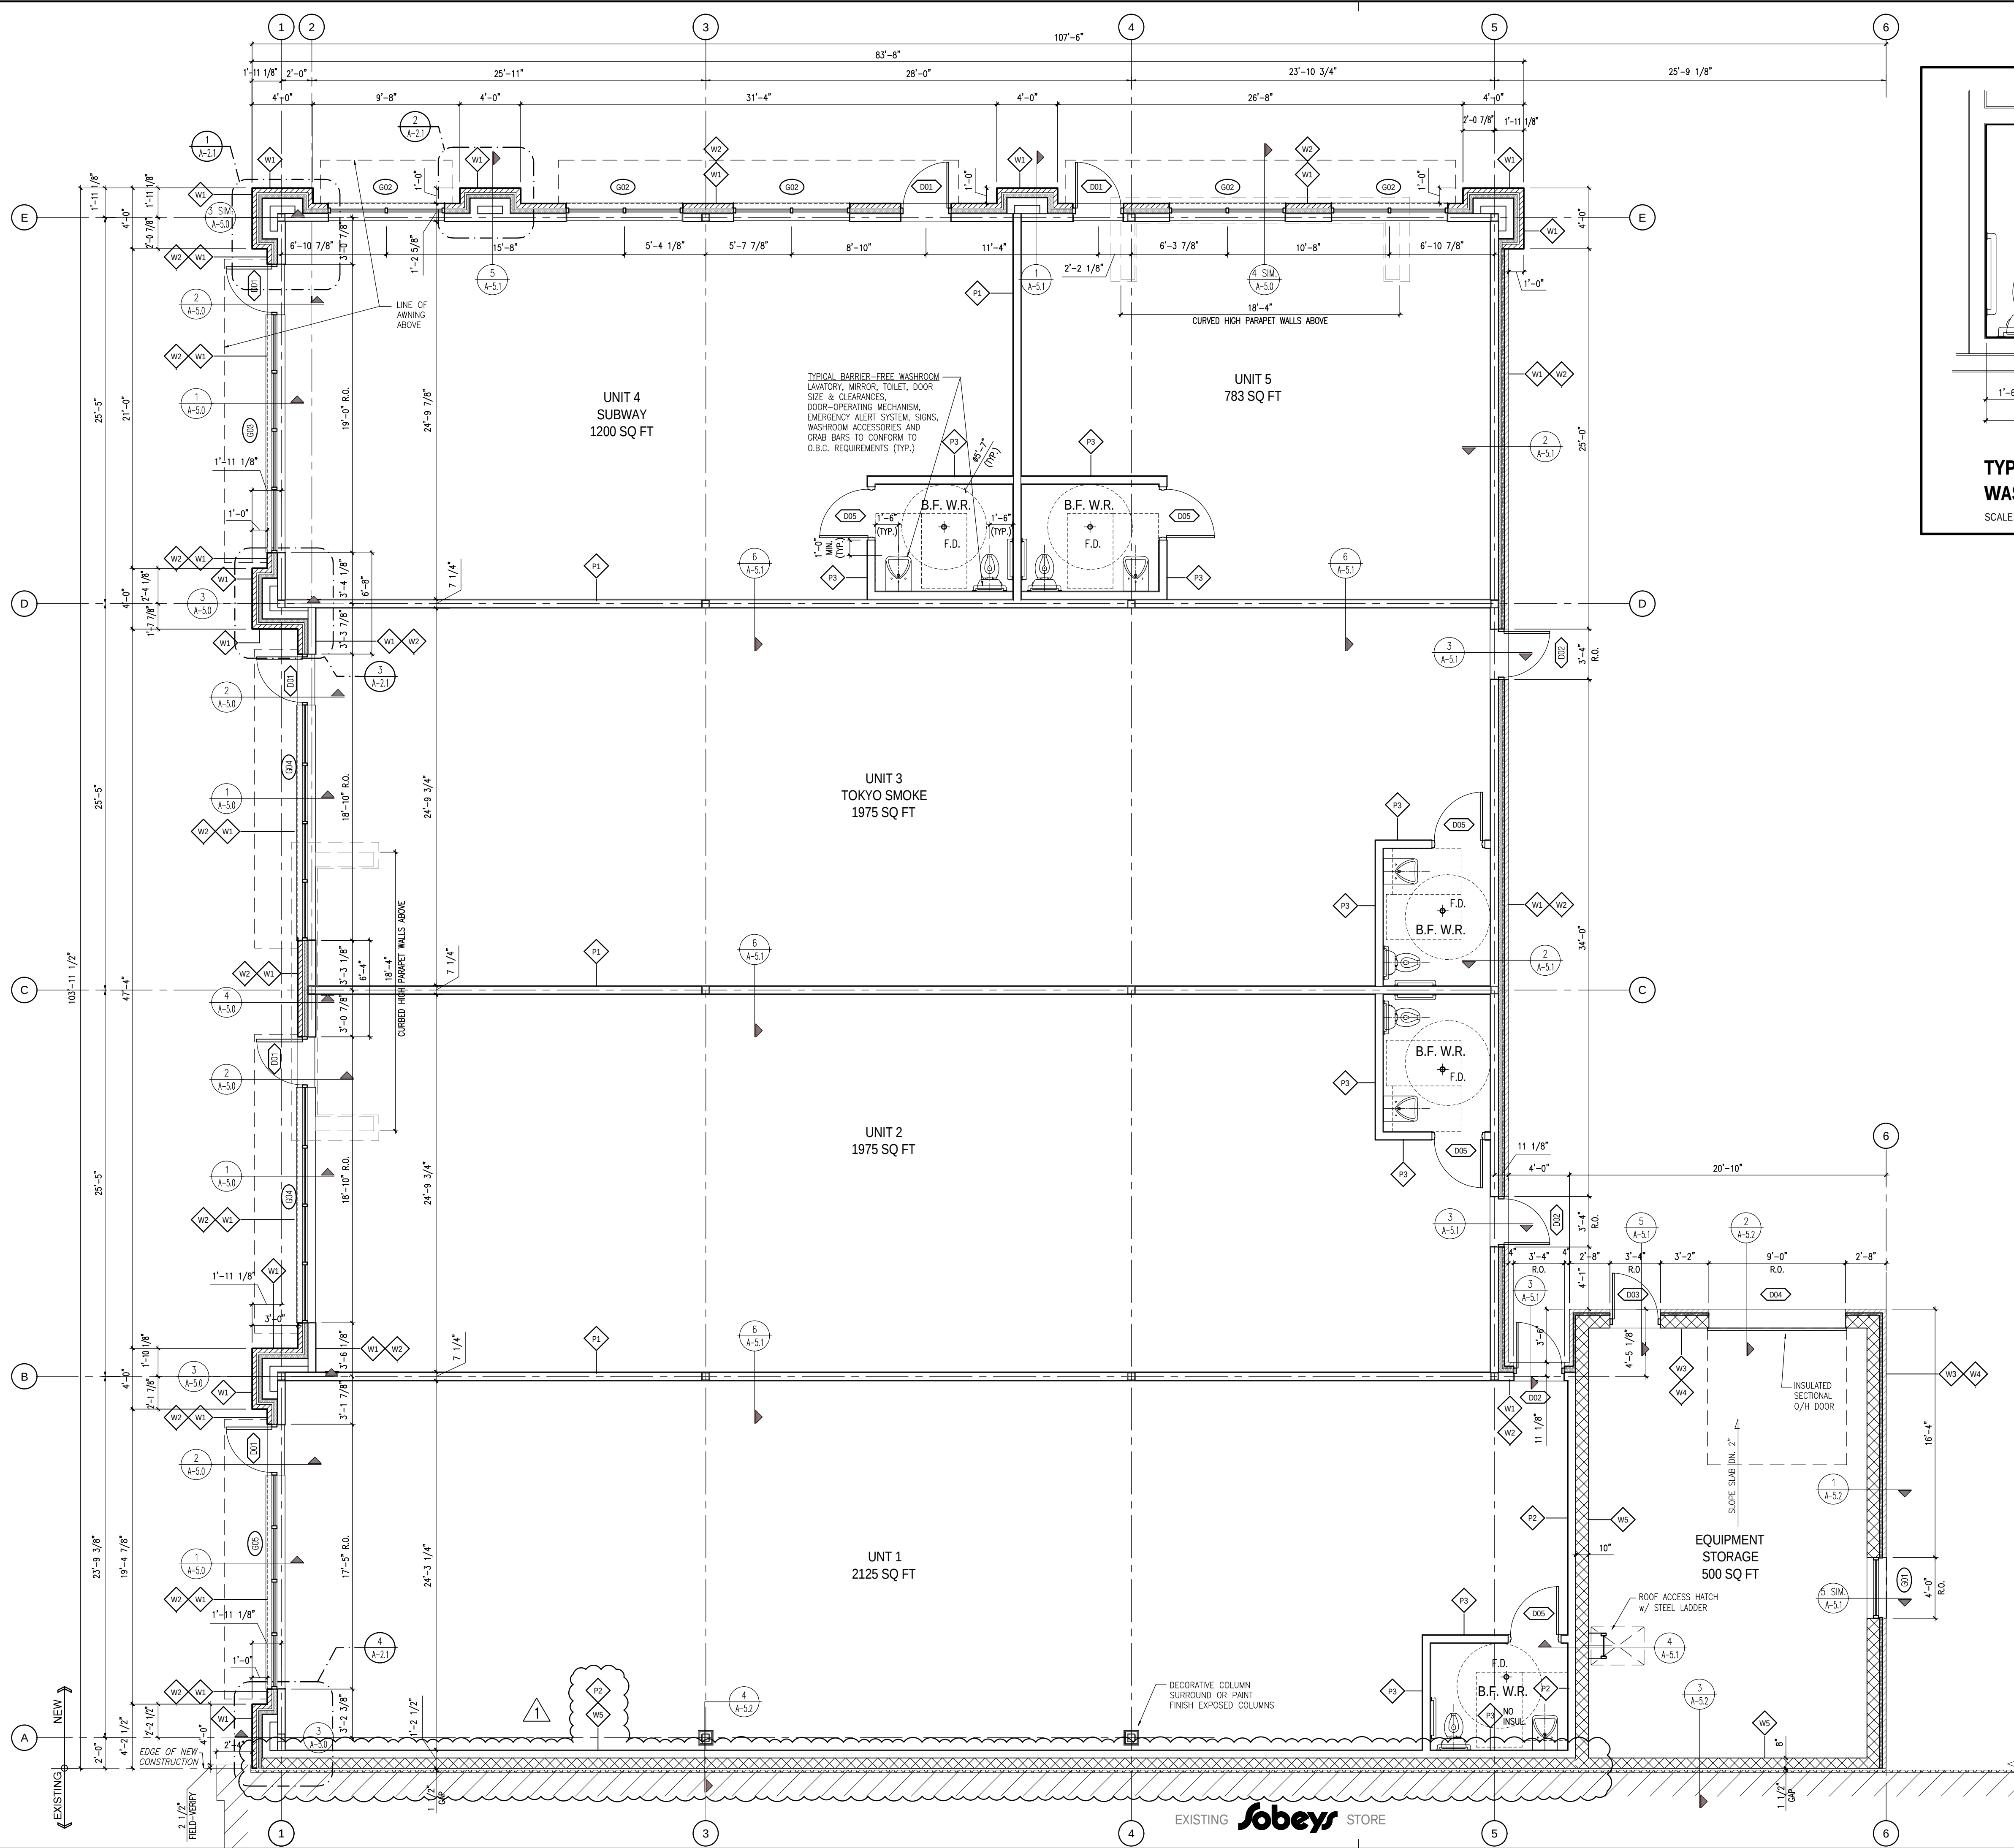

TYP. ENLARGED BARRIER-FREE (UNIVERSAL) WASHROOM LAYOUT

SCALE: 3/8" = 1'-0"

GROUND FLOOR PLAN SCALE: 3/16" = 1'-0"

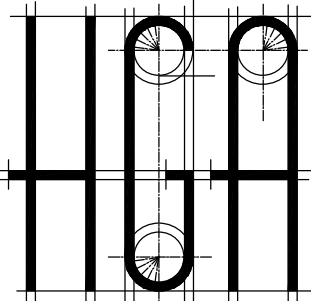

HANNA, GHOBRIAL AND ASSOCIATES LTD. engineering architecture 3100 Temple Drive Windsor, ON N8W 5J6 (519) 945-7373 FAX: 5636



This drawing shall not be used for construction unless it is countersigned by the CONSULTANT.

NOTE: ENGINEERED SHOP DRAWINGS, FOR ANY MANUFACTURED COMPONENT FORMING PART OF THE BUILDING (i.e. ENGINEERED ROOF TRUSSES, ENGINEERED FLOOR JOISTS, TIMERS, ETC.) MUST BE SUBMITTED TO HANNA, GHOBRIAL & ASSOCIATES, LTD. FOR REVIEW AND APPROVAL. IF ENGINEERED SHOP DRAWINGS ARE NOT SUBMITTED AND APPROVED, HANNA, GHOBRIAL & ASSOCIATES, LTD. WILL NOT BE RESPONSIBLE FOR ANY ASSOCIATED COSTS OR DAMAGES.










ALL DRAWINGS, SPECIFICATIONS AND OTHER RELATED DOCUMENTS ARE THE COPYRIGHT PROPERTY OF THE CONSULTANT AND SHALL BE RETURNED UPON REQUEST. REPRODUCTION OF DRAWINGS AND RELATED DOCUMENTS, IN WHOLE OR IN PART, IS FORBIDDEN WITHOUT THE WRITTEN PERMISSION OF THE CONSULTANT.

THE CONTRACTOR SHALL CHECK AND VERIFY ALL PERTINENT DIMENSIONS AND REPORT ANY DISCREPANCIES TO THE CONSULTANT BEFORE PROCEEDING WITH THE WORK.

THIS DRAWING SHALL NOT BE USED FOR CONSTRUCTION UNLESS IT IS COUNTERSIGNED BY THE CONSULTANT.

THIS DRAWING IS NOT TO BE SCALED. USE FIGURED DIMENSIONS ONLY.

12		
11		
10		
9		
8		
7		
6		
5		
4	22/03/31	REV. PER CITY COMMENTS
3	22/02/08	FOR PERMIT
2	22/01/31	ARCH&STRU REVISION
1	21/08/13	CLIENT REVIEW
No. Date:		Issued For:
Date:		OCTOBER 2021
Drawn By:		R.J./R.Z./H.R.
Checked By:		R.J.
Project Title:		
83 SANDWICH STREET BUILDING ADDITION		
AMHERSTBURG, ONTARIO		
Project No.:		21-0427
Sheet Title:		
FLOOR PLAN		
Sheet No.:		A-2.0

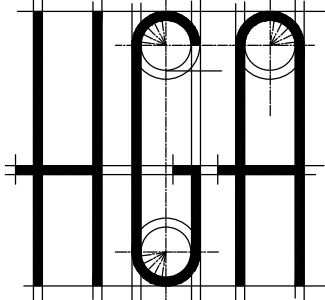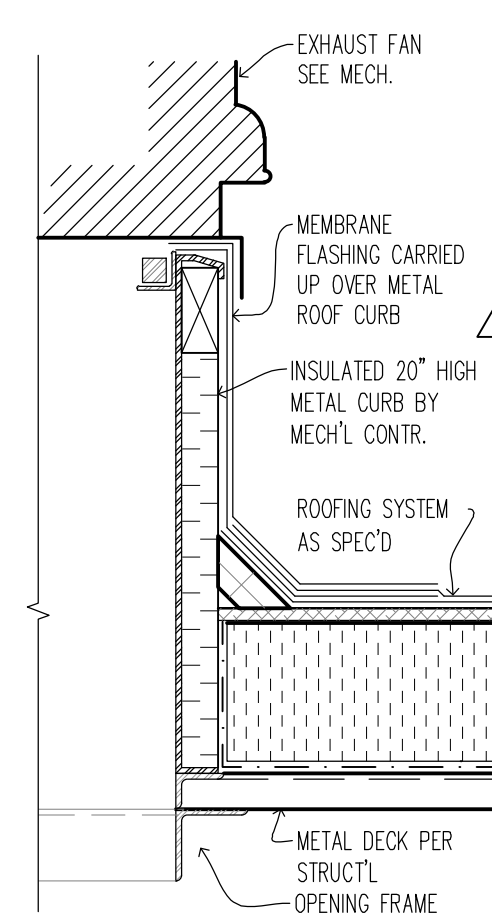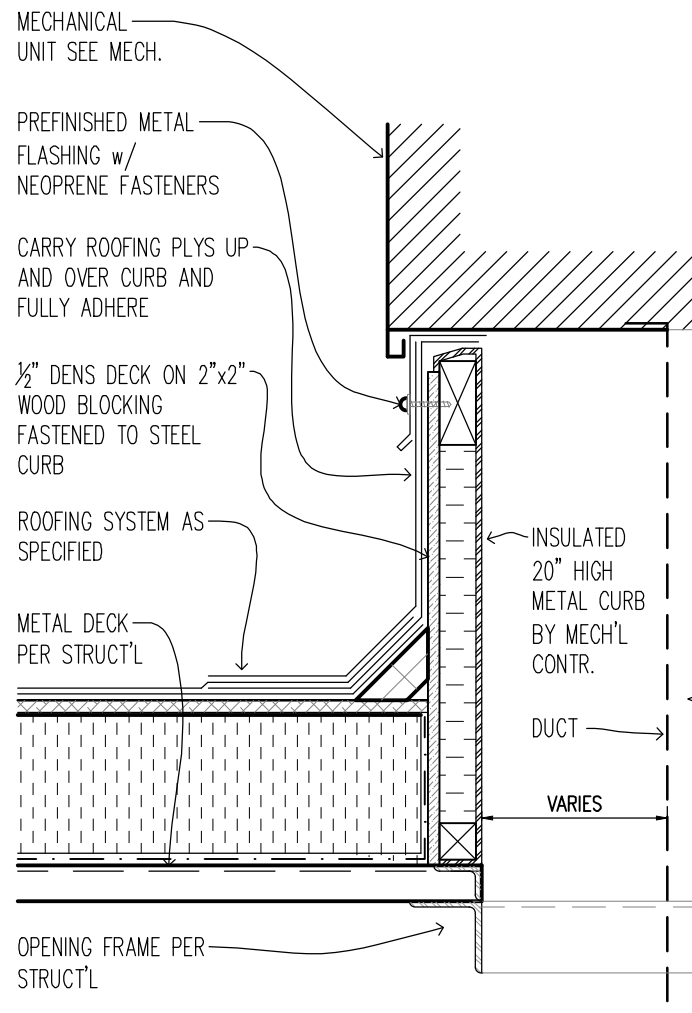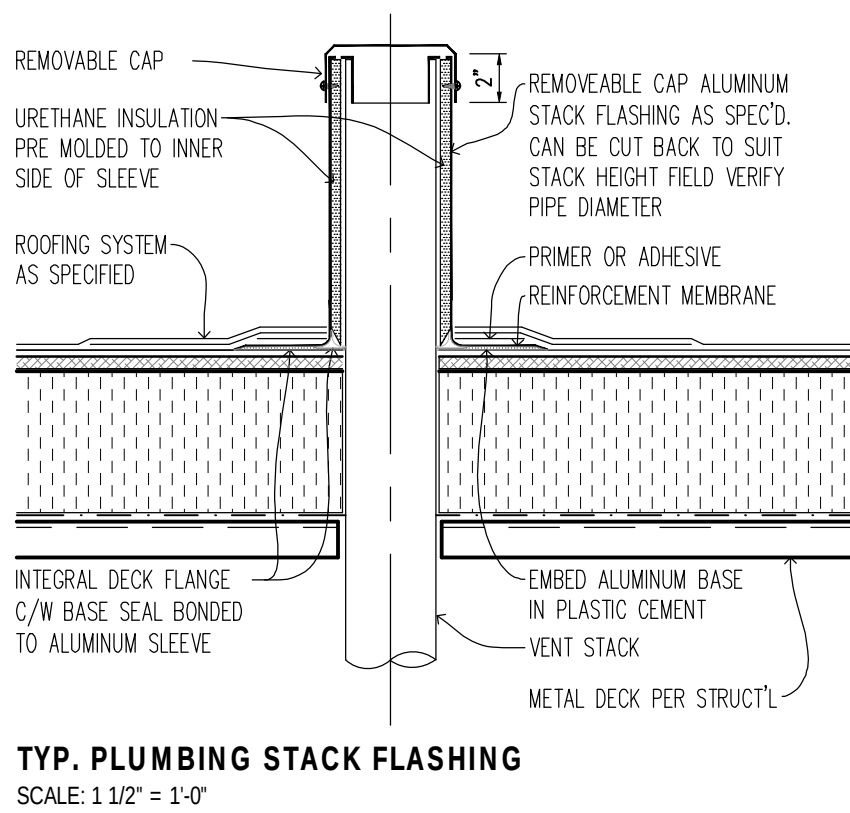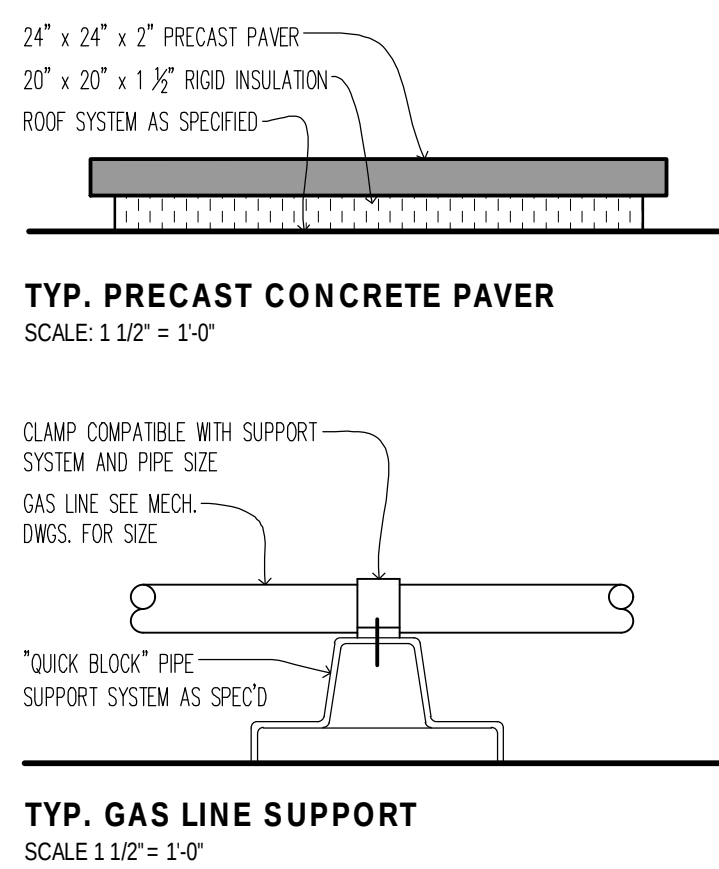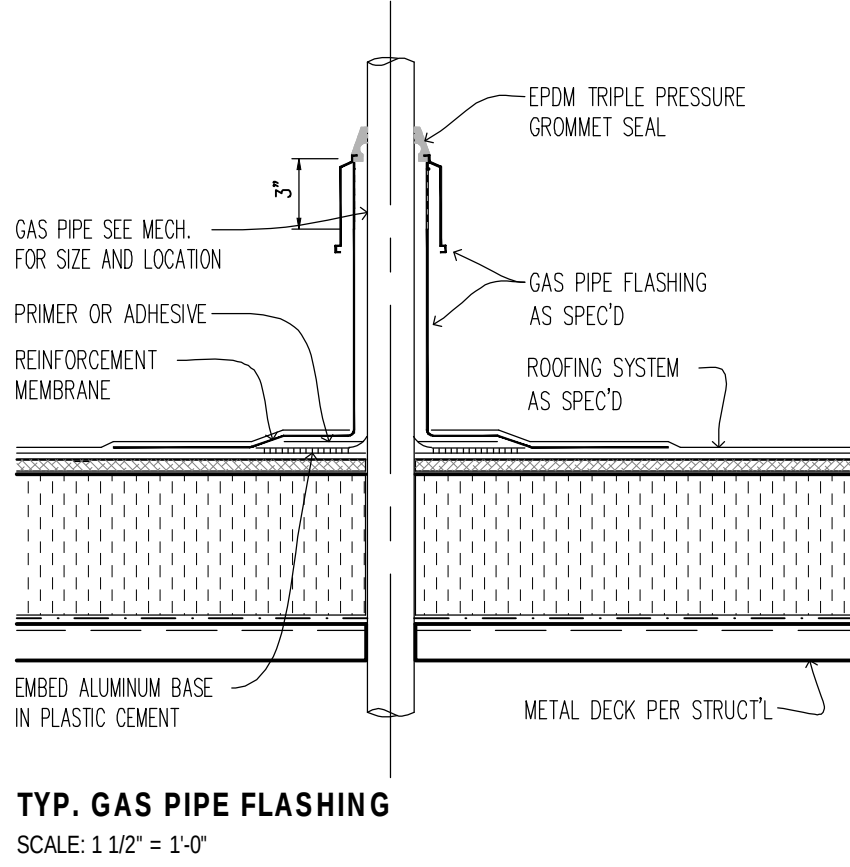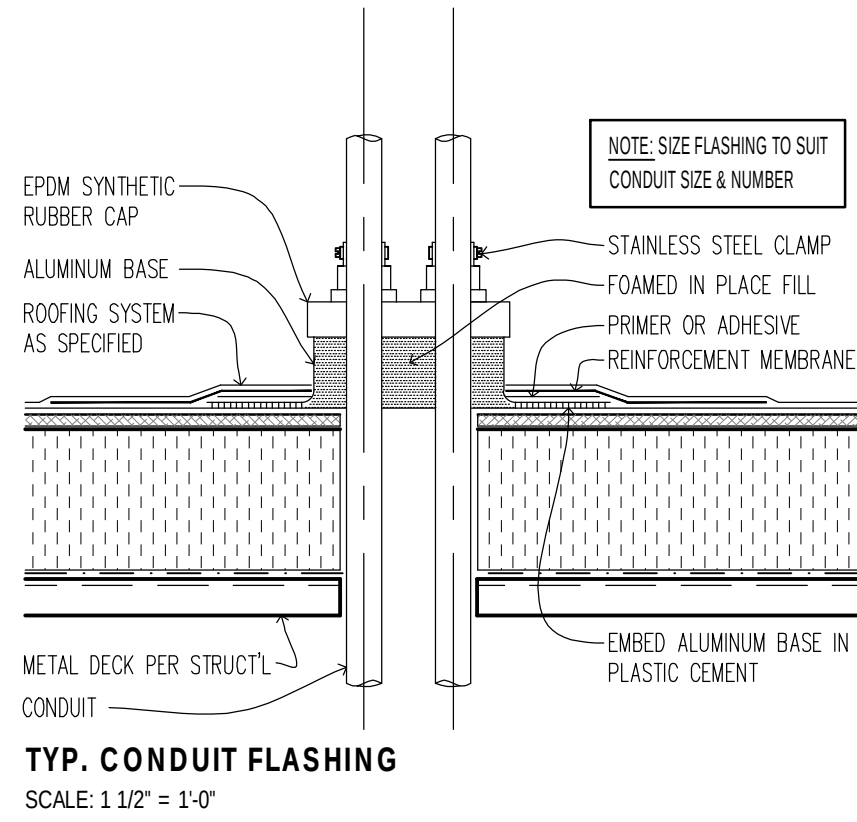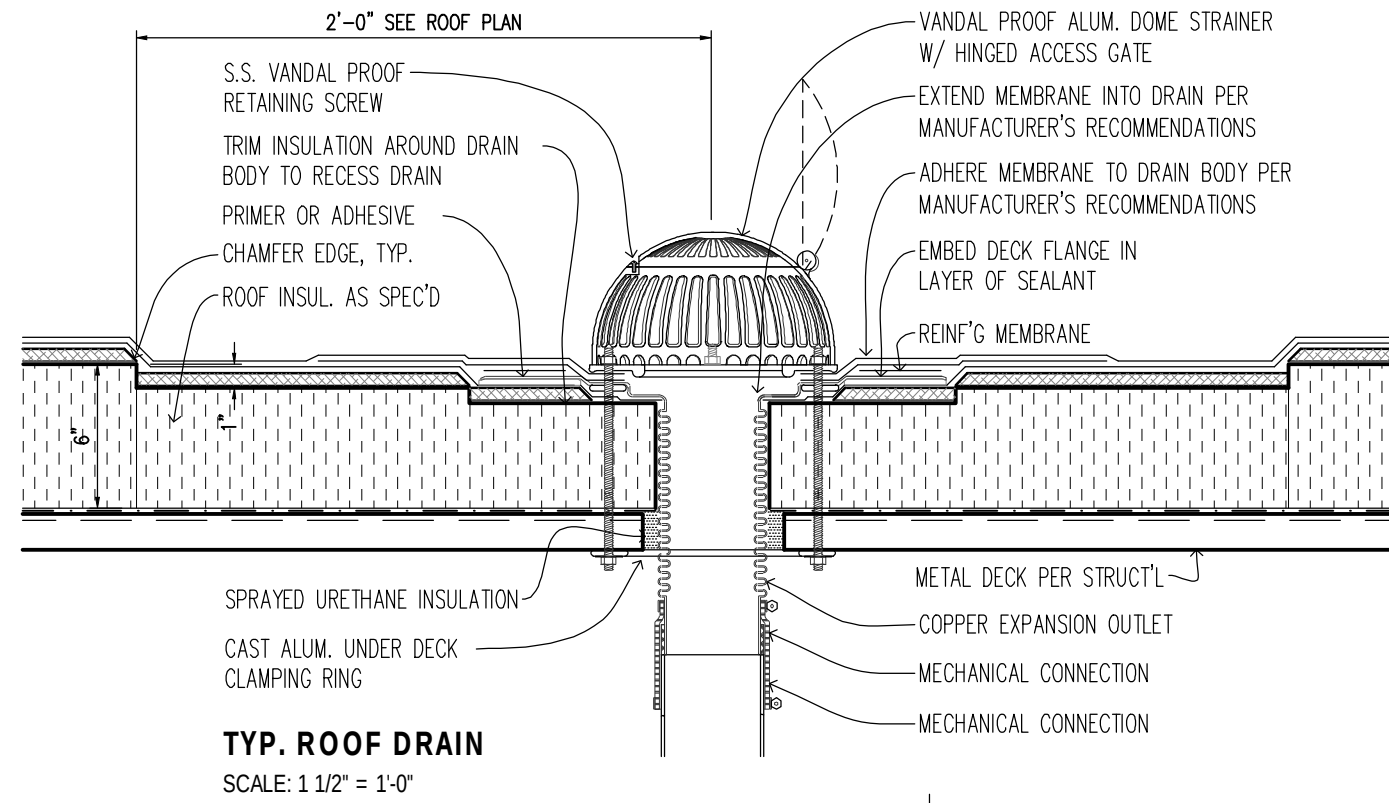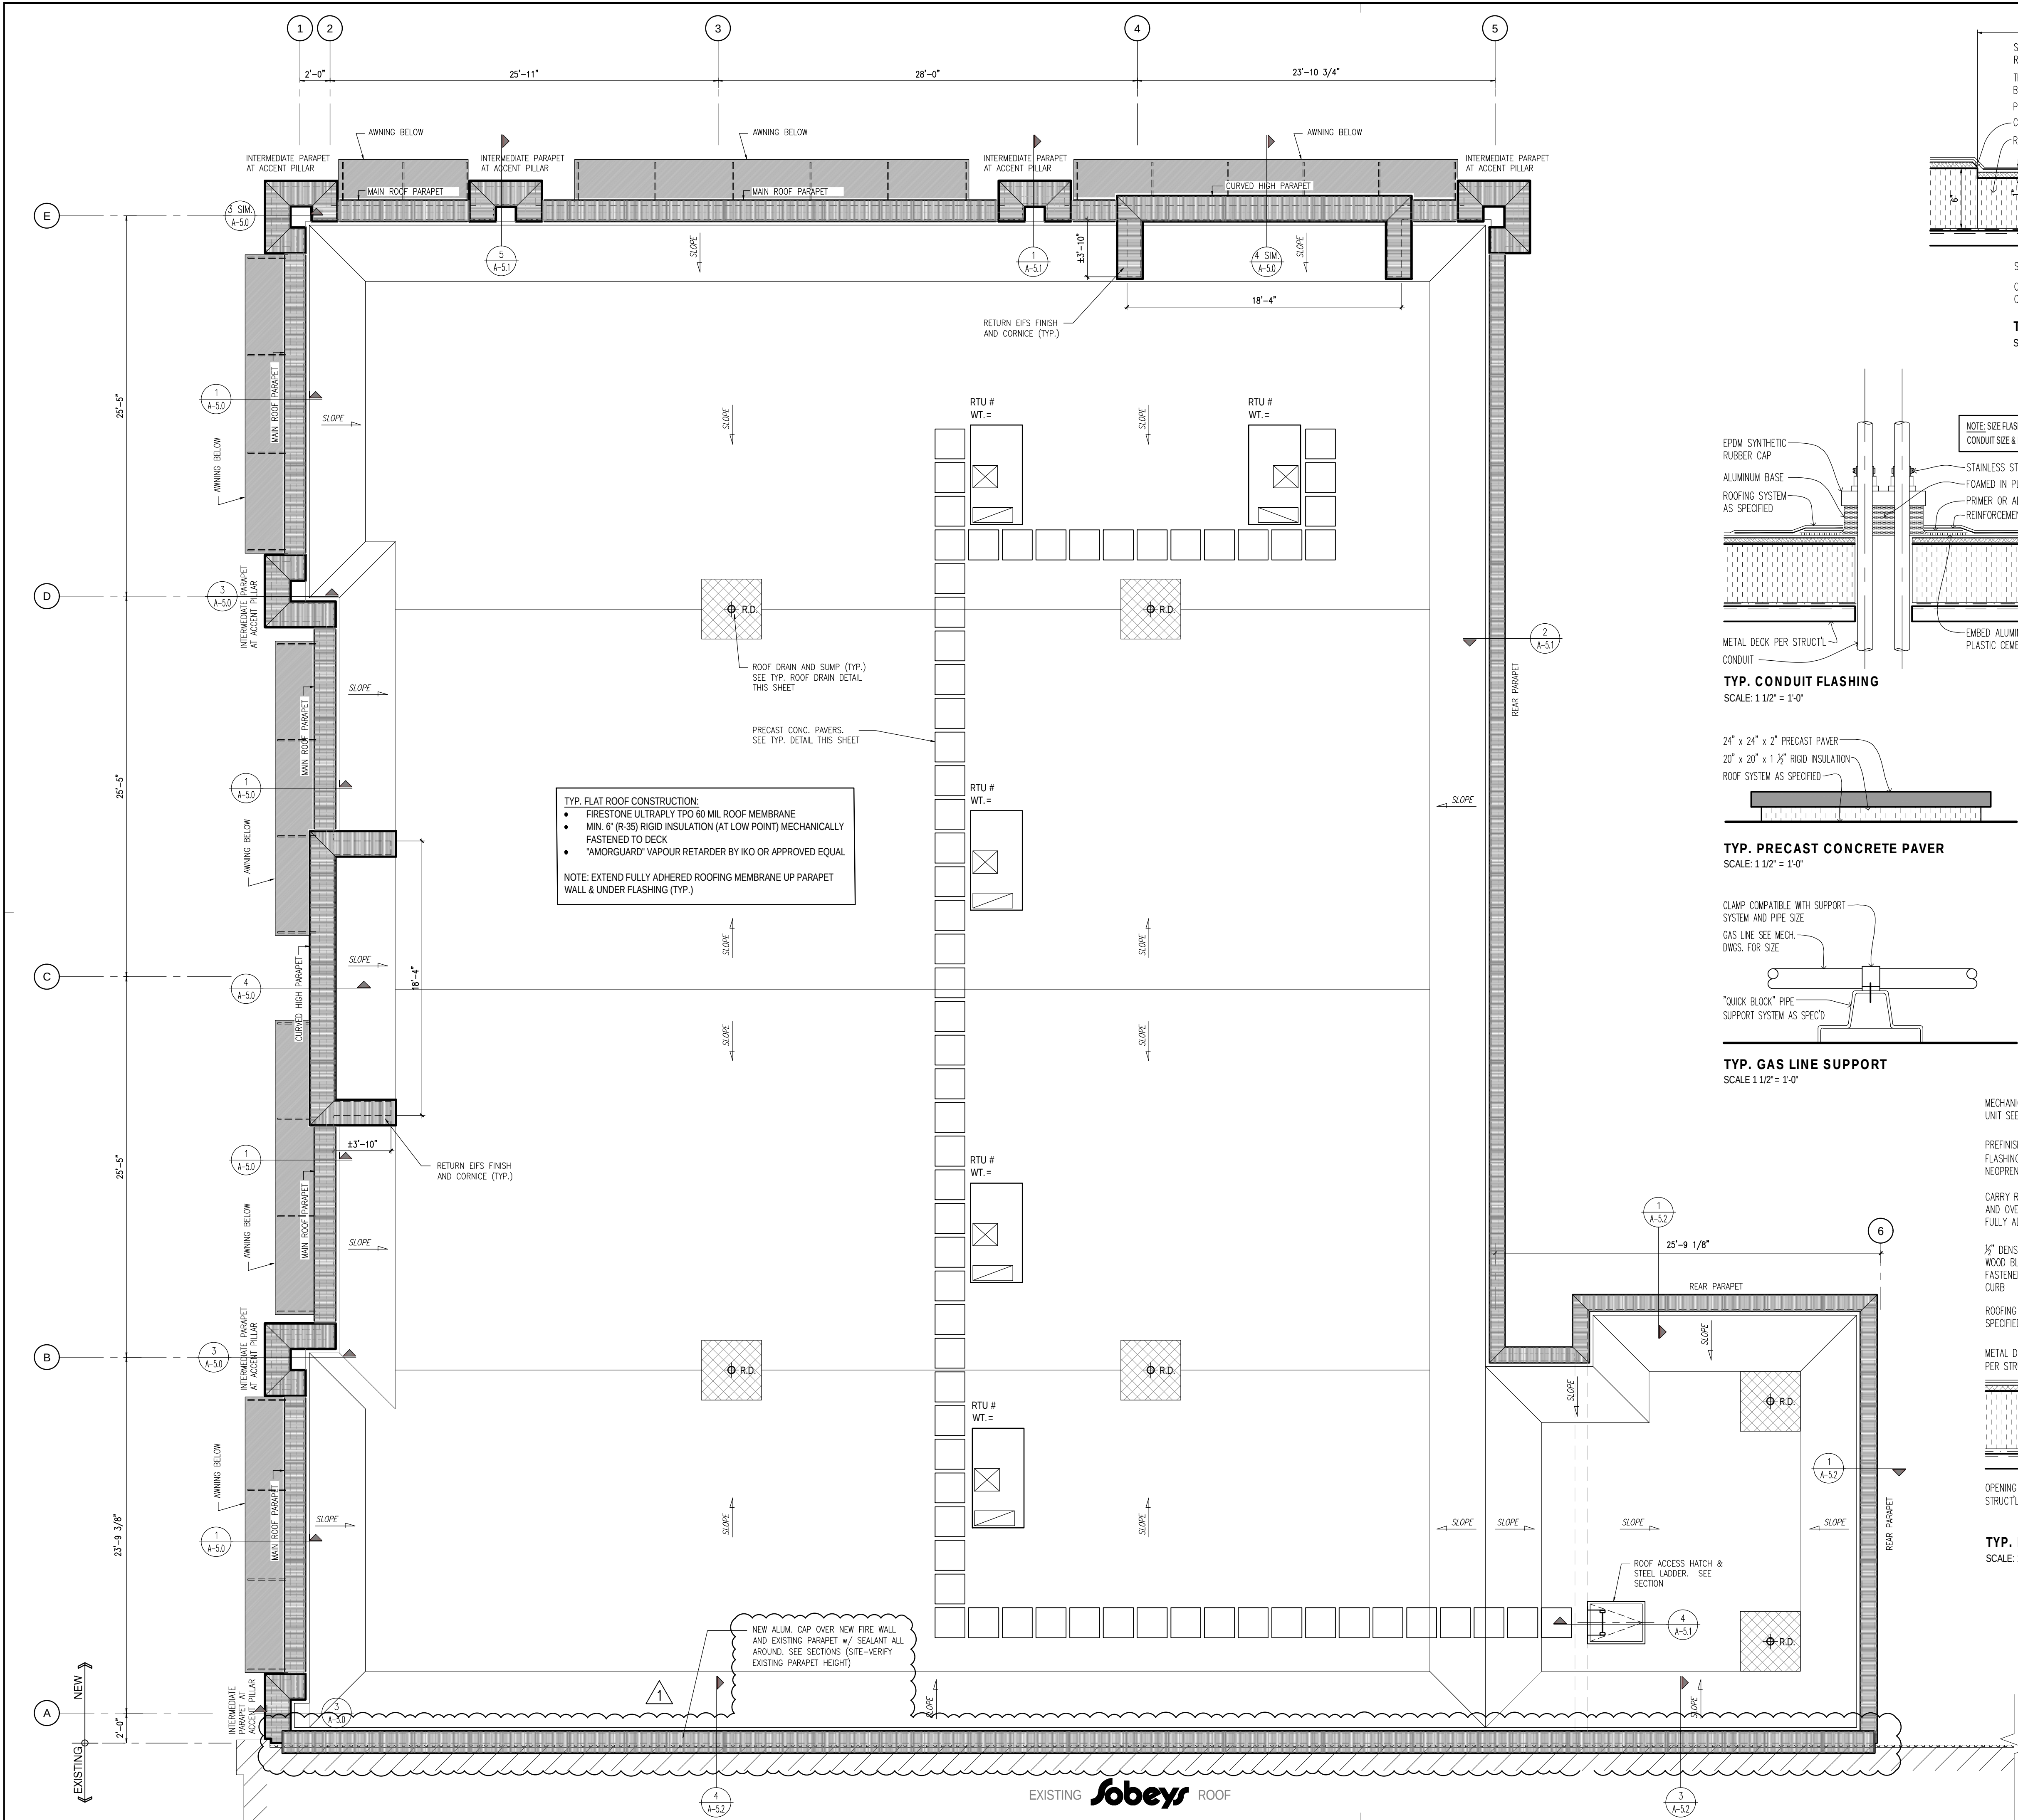

HANNA, GHOBRIAL
AND ASSOCIATES LTD.
engineering
architecture
3100 Temple Drive
Windsor, ON N8W 5J6
(519) 945-7373 FAX: 5636



This drawing shall not be used for construction unless it is countersigned by the CONSULTANT.

NOTE:
ENGINEERED SHOP DRAWINGS, FOR ANY MANUFACTURED COMPONENT FORMING PART OF THE BUILDING (i.e. ENGINEERED ROOF TRUSSES, ENGINEERED FLOOR JOISTS, TIMERS, ETC.), MUST BE SUBMITTED TO HANNA, GHOBRIAL & ASSOCIATES, LTD. FOR REVIEW AND APPROVAL. IF ENGINEERED SHOP DRAWINGS ARE NOT SUBMITTED AND APPROVED, HANNA, GHOBRIAL & ASSOCIATES, LTD. WILL NOT BE RESPONSIBLE FOR ANY ASSOCIATED COSTS OR DAMAGES.


ALL DRAWINGS, SPECIFICATIONS AND OTHER RELATED DOCUMENTS ARE THE COPYRIGHT PROPERTY OF THE CONSULTANT AND SHALL BE RETURNED UPON REQUEST.
REPRODUCTION OF DRAWINGS AND RELATED DOCUMENTS, IN WHOLE OR IN PART, IS FORBIDDEN WITHOUT THE WRITTEN PERMISSION OF THE CONSULTANT.
THE CONTRACTOR SHALL CHECK AND VERIFY ALL PERTINENT DIMENSIONS AND REPORT ANY DISCREPANCIES TO THE CONSULTANT BEFORE PROCEEDING WITH THE WORK.
THIS DRAWING SHALL NOT BE USED FOR CONSTRUCTION UNLESS IT IS COUNTERSIGNED BY THE CONSULTANT.
THIS DRAWING IS NOT TO BE SCALED.
USE FIGURED DIMENSIONS ONLY.

12		
11		
10		
9		
8		
7		
6		
5		
4	22/03/31	REV. PER CITY COMMENTS
3	22/02/08	FOR PERMIT
2	22/01/31	ARCH&STRU REVISION
1	21/08/13	CLIENT REVIEW
YY/MM/DD		
No. Date:	Issued For:	
Date:	OCTOBER 2021	
Drawn By:	H.R.	
Checked By:	R.J.	

Project Title:
83 SANDWICH STREET
BUILDING ADDITION
AMHERSTBURG, ONTARIO
Project No.:
21-0427

Sheet Title:
ROOF PLAN
& DETAILS

Sheet No.:
A-3.0

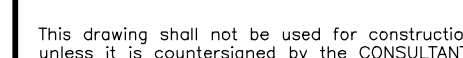

NOTE:
ENGINEERED SHOP DRAWINGS, FOR ANY
"MANUFACTURED COMPONENT" FORMING PART OF
THE BUILDING (i.e. ENGINEERED ROOF TRUSSES,
ENGINEERED FLOOR JOISTS, TIMERS, ETC.), MUST BE
SUBMITTED TO HANNA GHOBRIAL & ASSOCIATES, LTD.
FOR REVIEW AND APPROVAL. IF ENGINEERED SHOP
DRAWINGS ARE NOT SUBMITTED AND APPROVED,
HANNA GHOBRIAL & ASSOCIATES, LTD WILL NOT BE
RESPONSIBLE FOR ANY ASSOCIATED COSTS OR
DAMAGE.

ALL DRAWINGS, SPECIFICATIONS AND OTHER RELATED DOCUMENTS ARE THE COPYRIGHT PROPERTY OF THE **CONSULTANT** AND SHALL BE RETURNED UPON REQUEST.

REPRODUCTION OF DRAWINGS AND RELATED DOCUMENTS, IN WHOLE OR IN PART, IS FORBIDDEN WITHOUT THE WRITTEN PERMISSION OF THE **CONSULTANT**.

THE CONTRACTOR SHALL CHECK AND VERIFY ALL PERTINENT DIMENSIONS AND REPORT ANY DISCREPANCIES TO THE **CONSULTANT** BEFORE PROCEEDING WITH THE WORK.

THIS DRAWING SHALL NOT BE USED FOR CONSTRUCTION UNLESS IT IS COUNTERSIGNED BY THE **CONSULTANT**.

No.	YY/MM/DD Date:	Issued For:
	Date:	OCTOBER 2021
	Drawn By:	R.Z./H.R.
	Checked By:	R.J.
Project Title:		

83 SANDWICH STREET
BUILDING ADDITION

AMHERSTBURG, ONTARIO




21-0427

Sheet Title:

ELEVATIONS


Sheet No.:

A-4.0

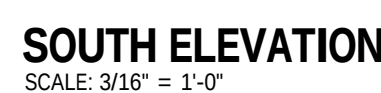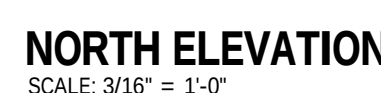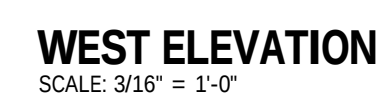







WALL TYPES

SCALE: 1" = 1'-0"

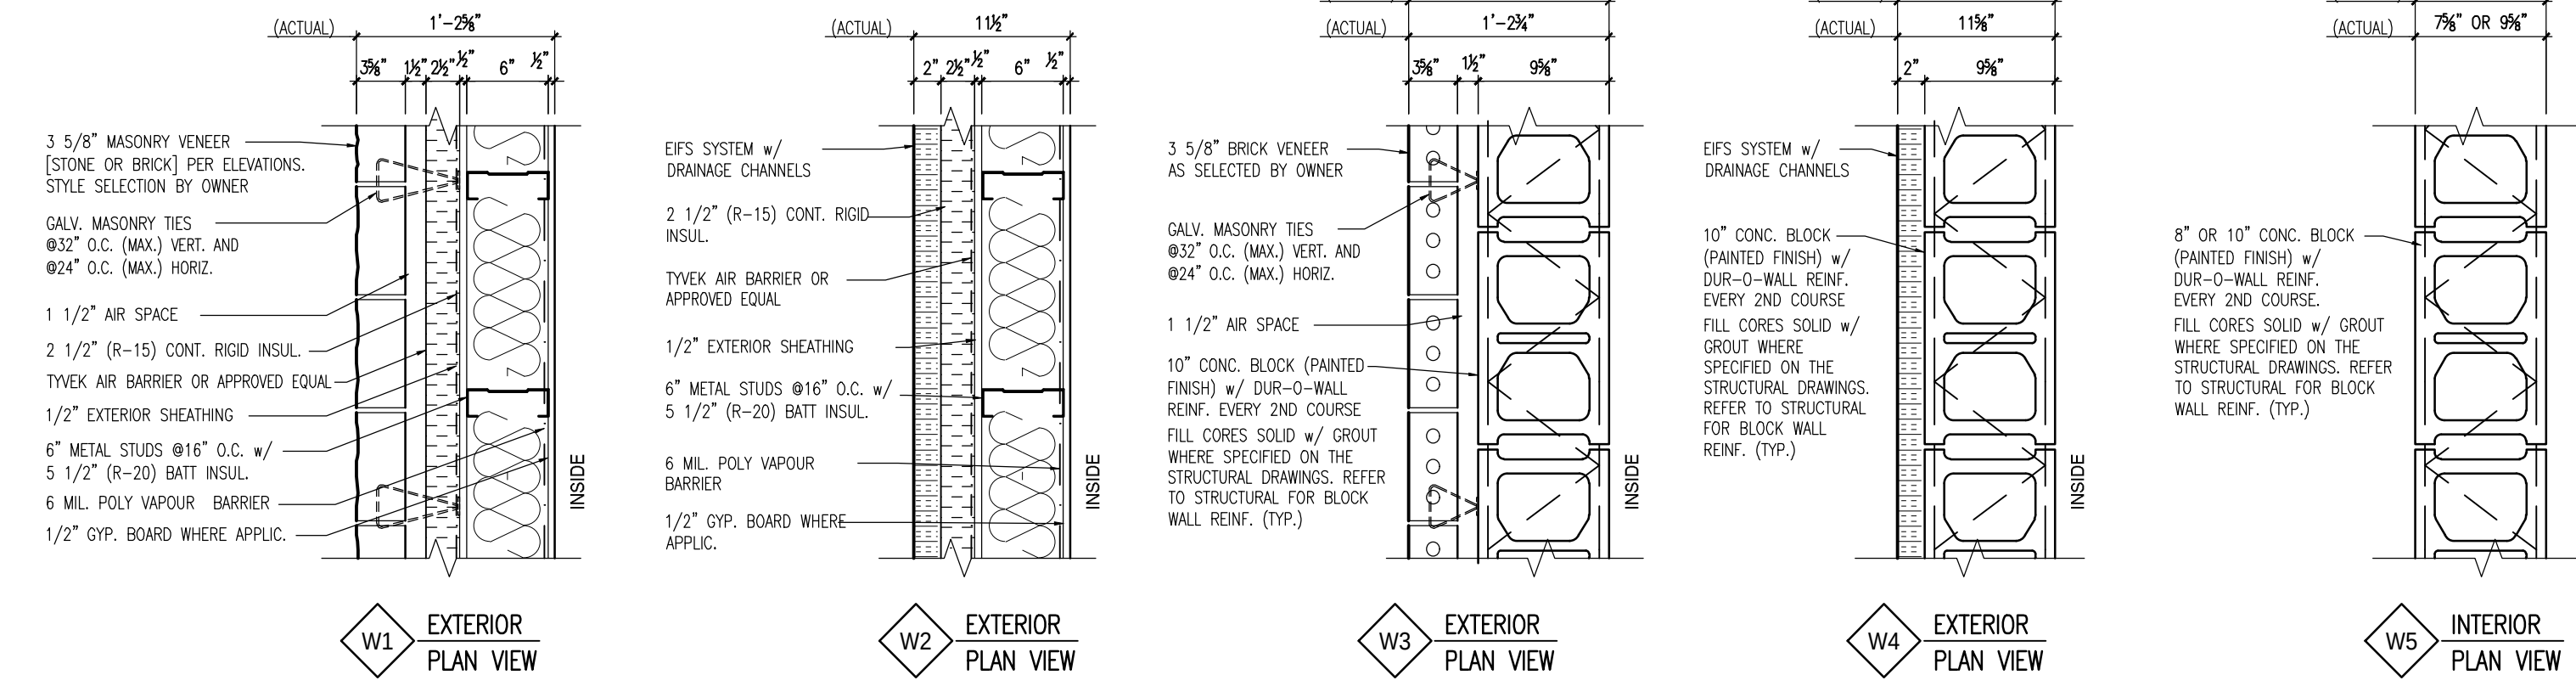

PARTITION TYPES

SCALE: 1" = 1'-0"

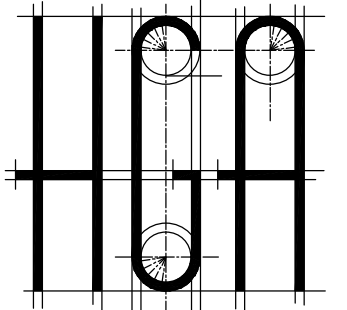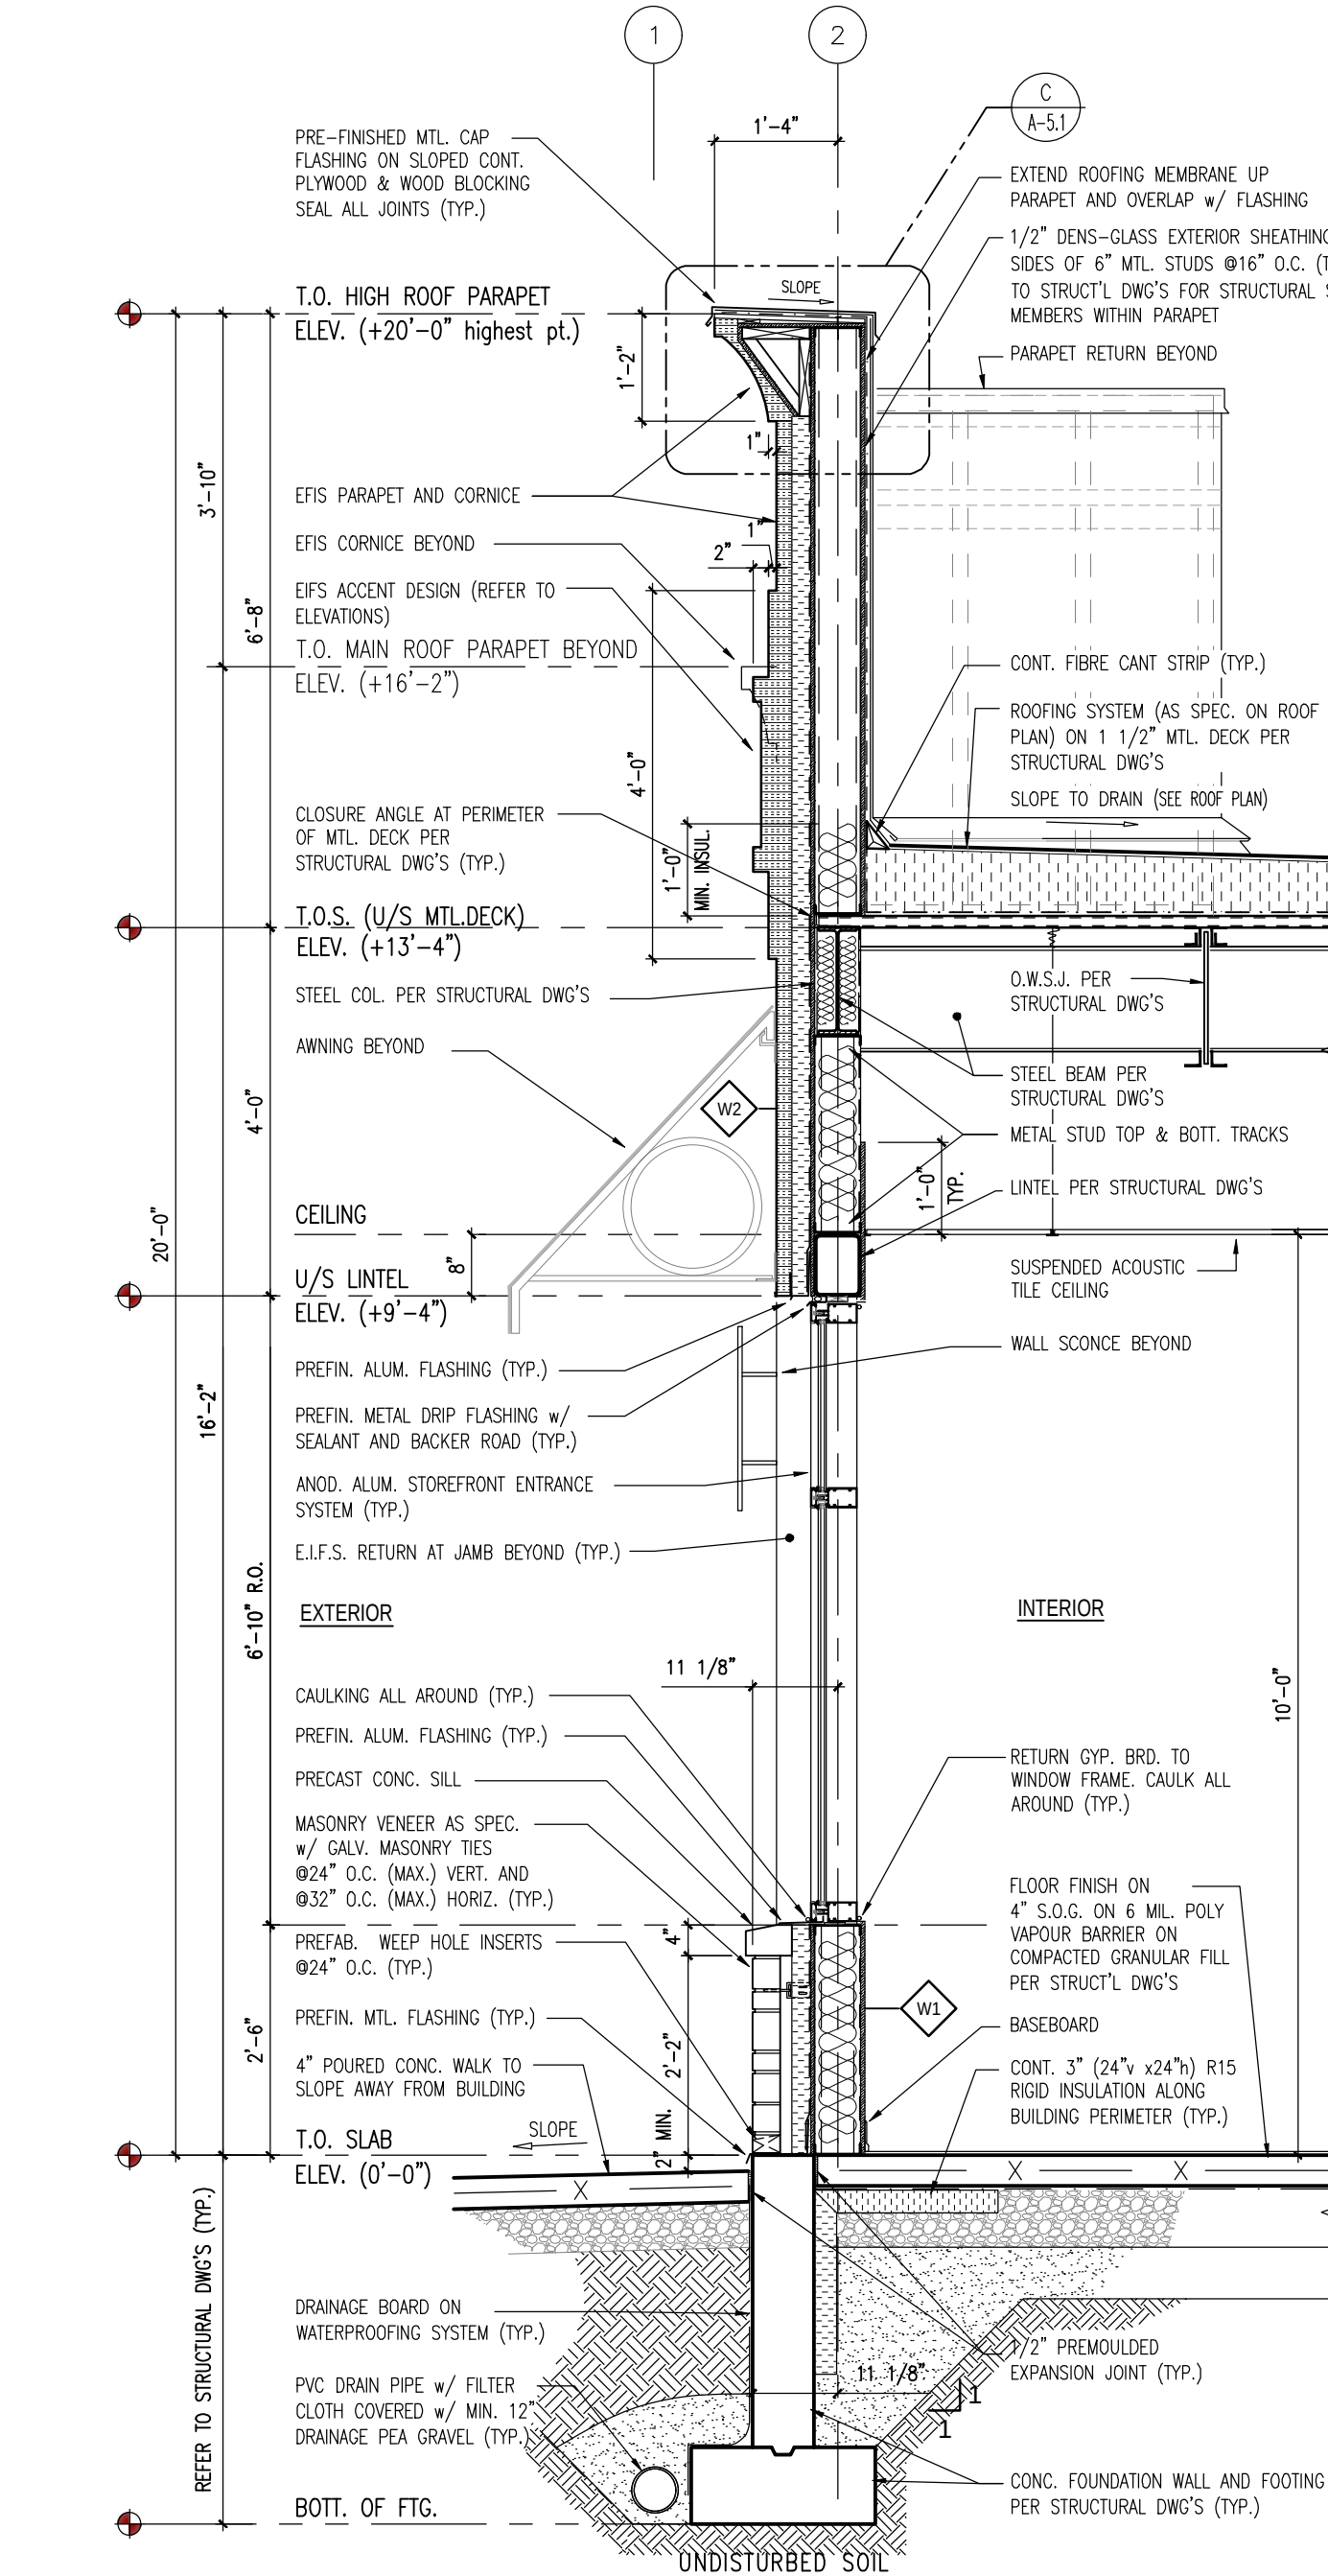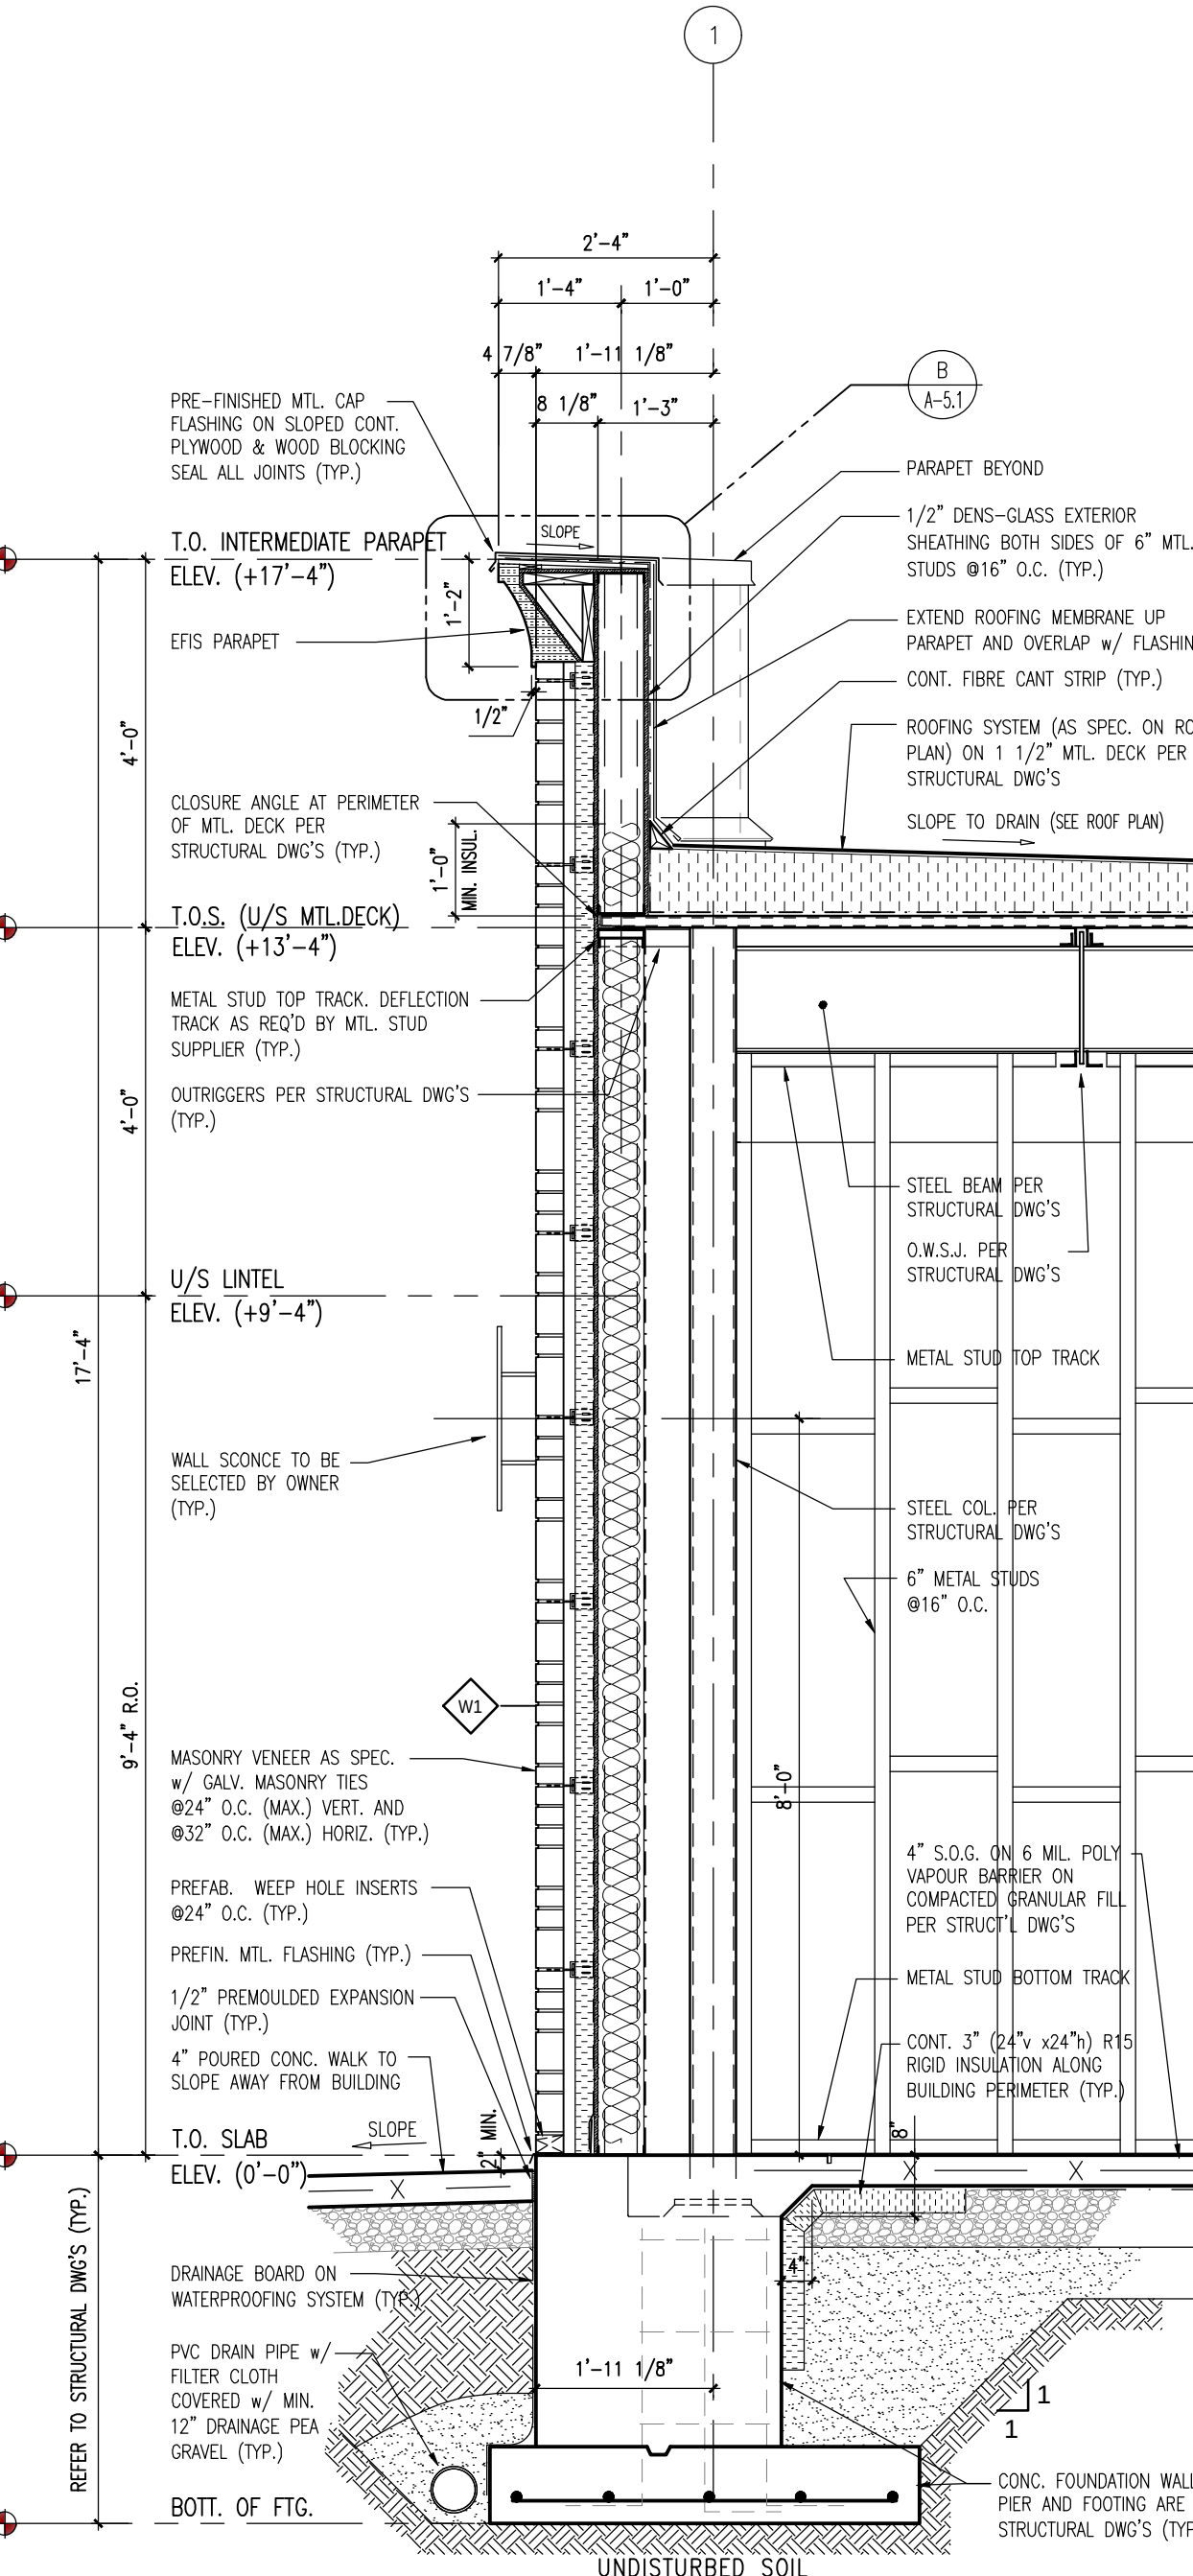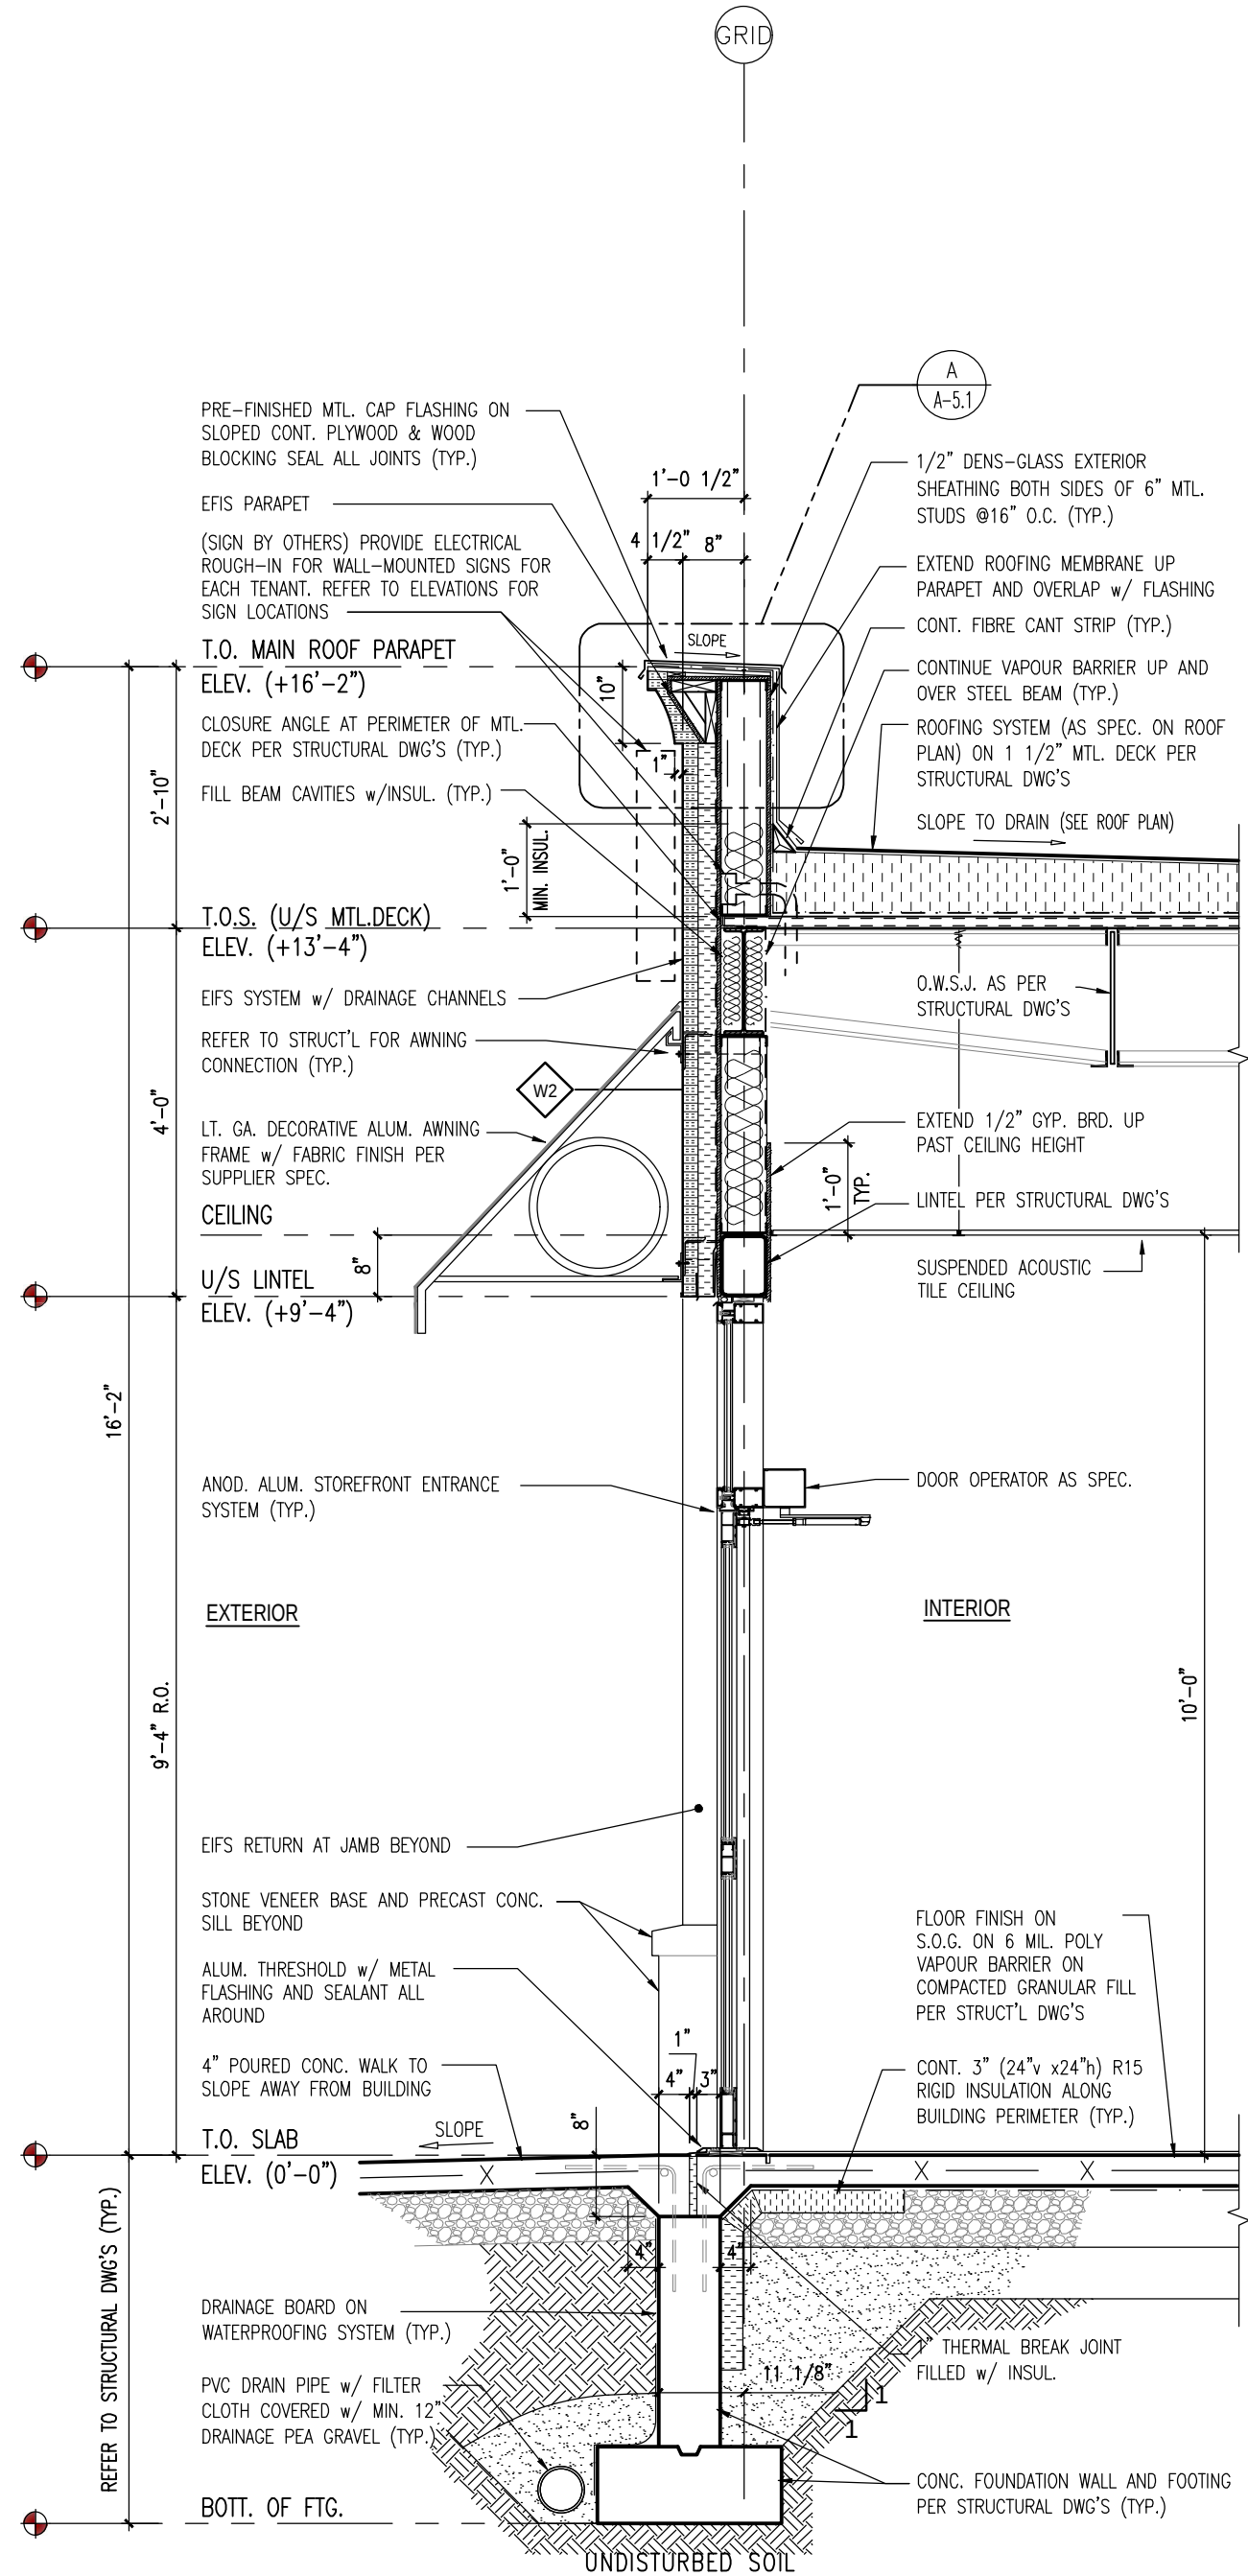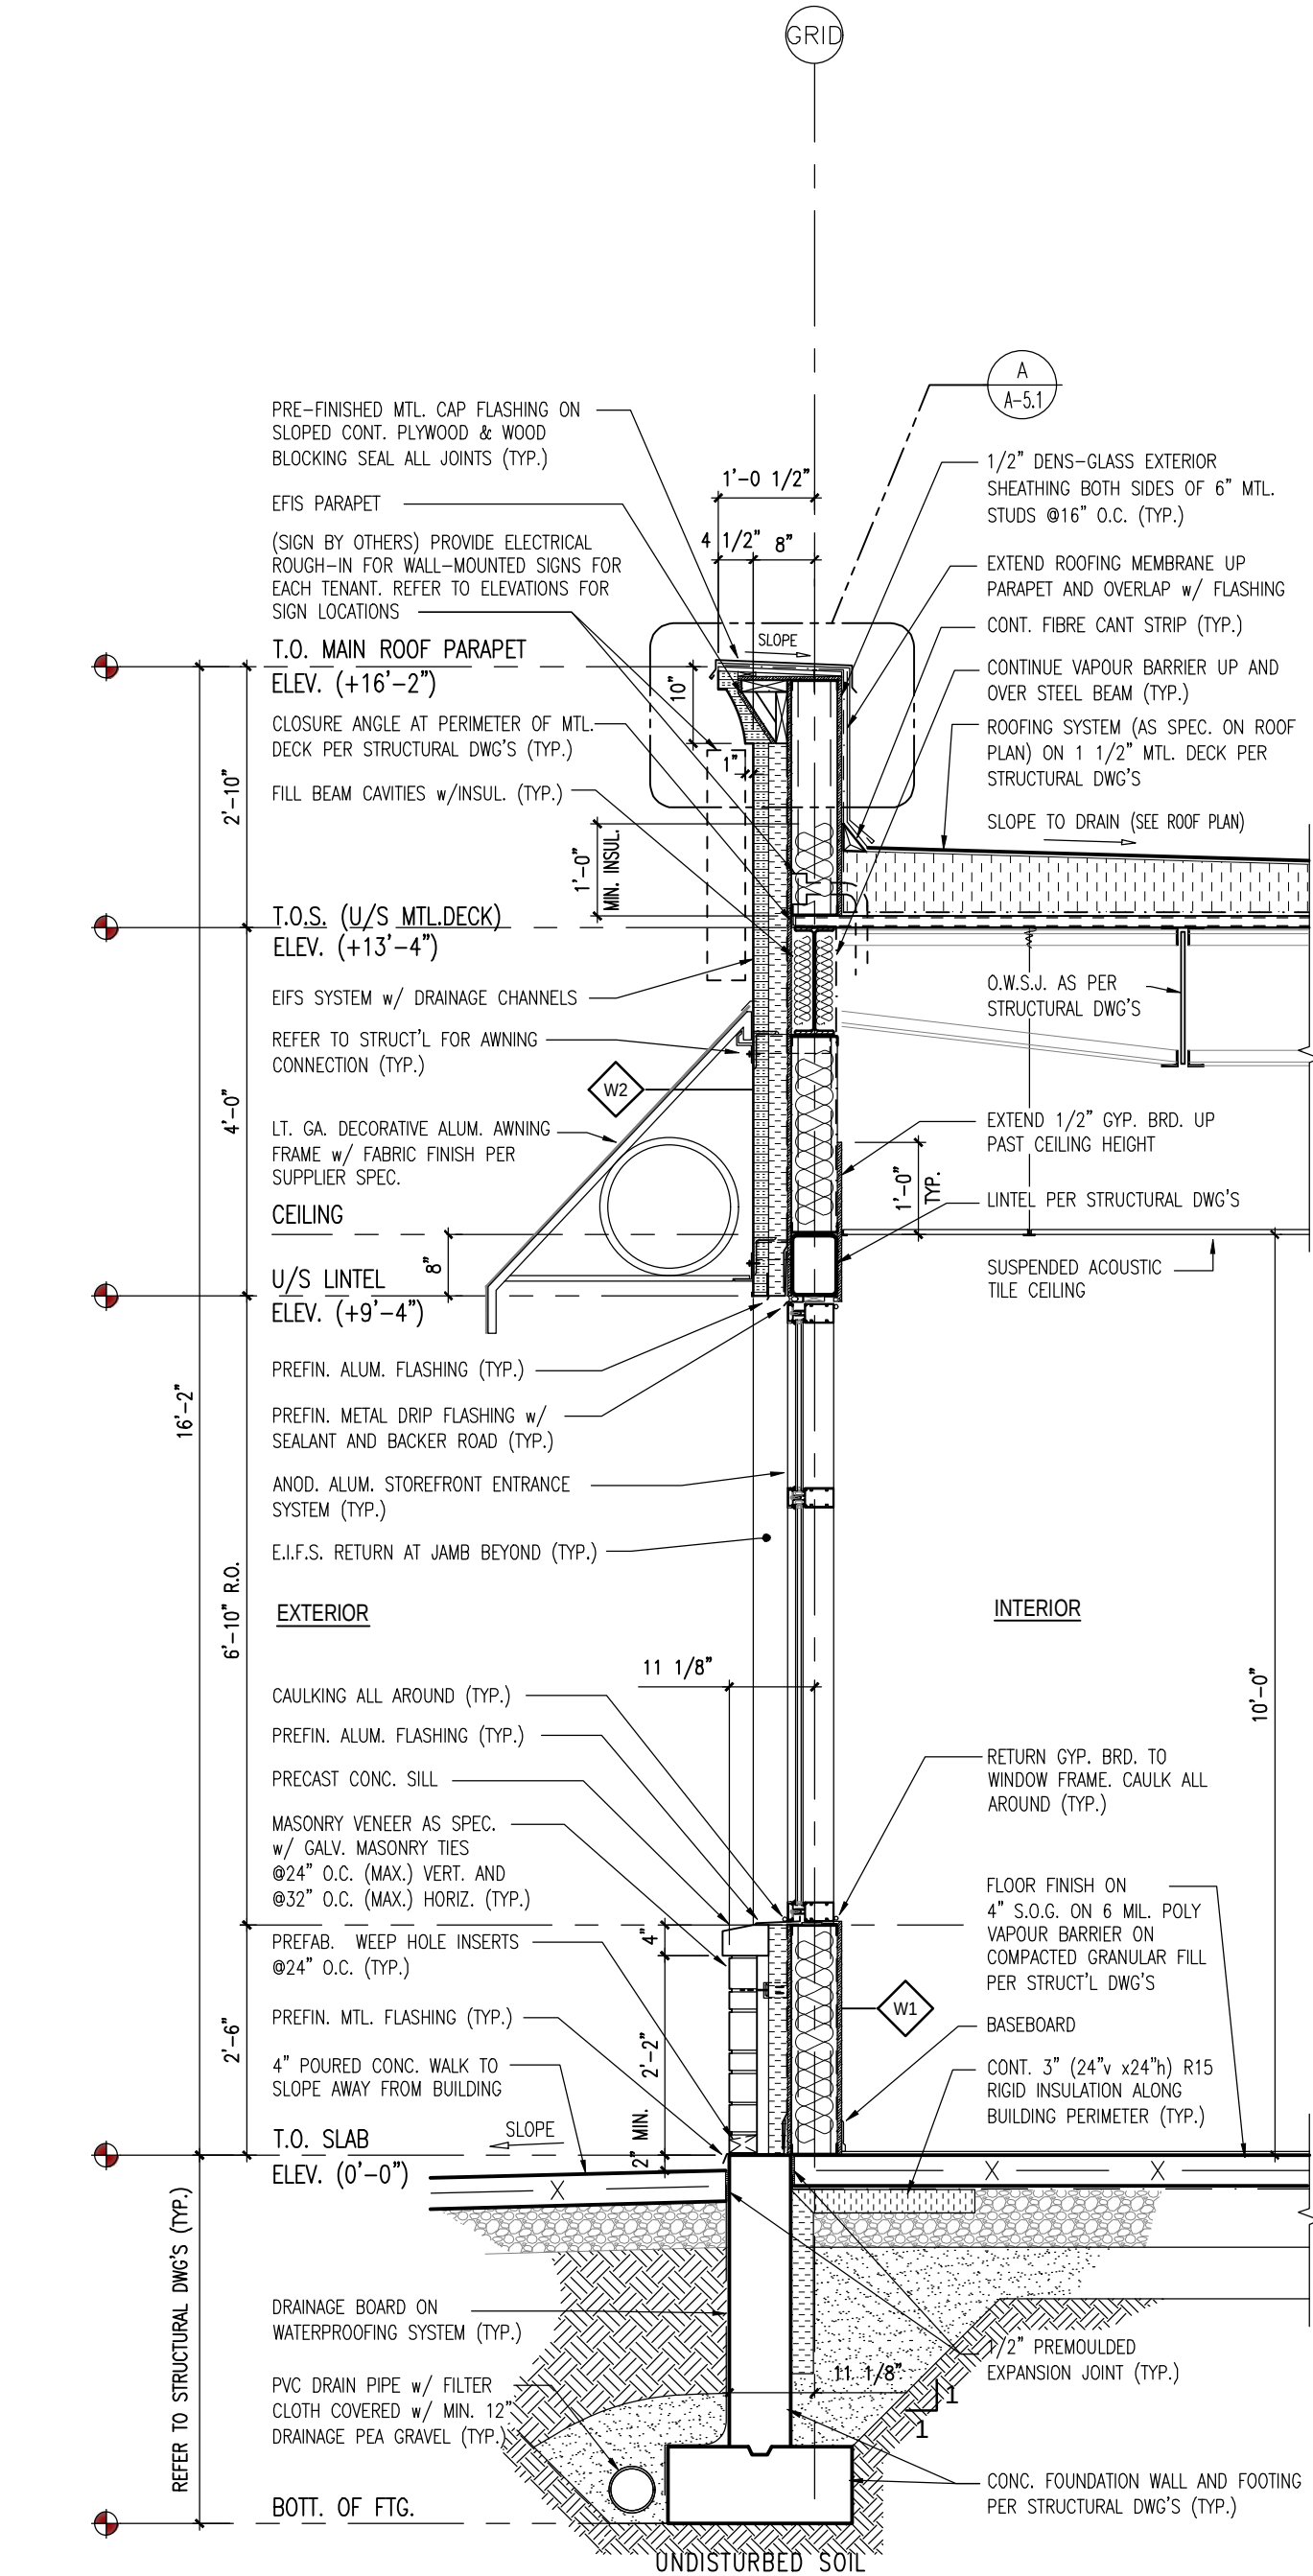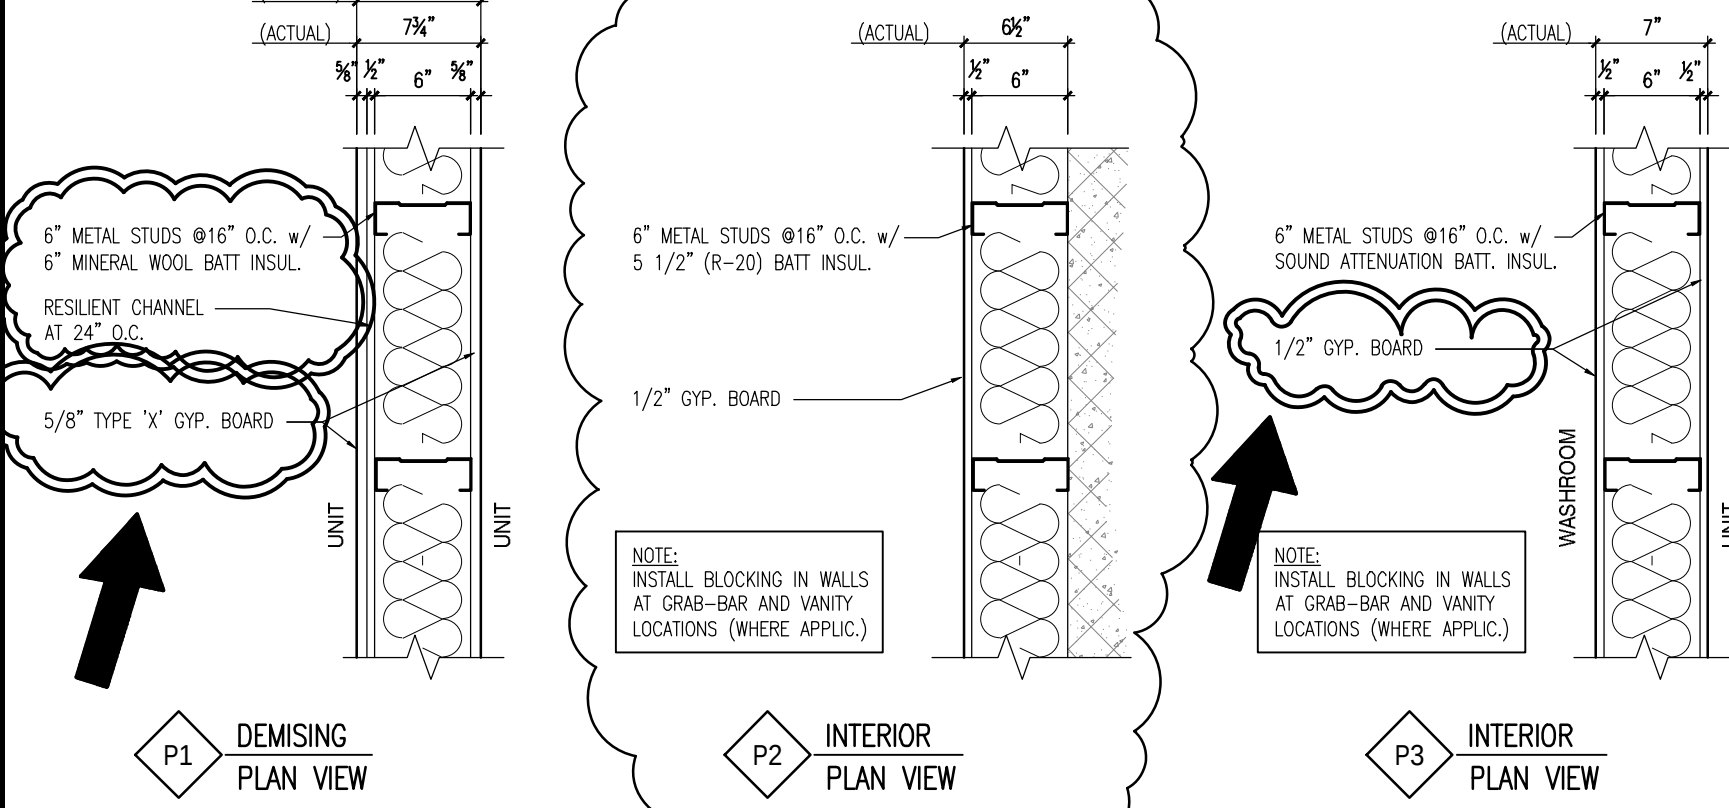

HANNA, GHOBRIAL
AND ASSOCIATES LTD.
engineering
architecture
3100 Temple Drive
Windsor, ON N8W 5J6
(519) 945-7373 FAX-5636



This drawing shall not be used for construction unless it is countersigned by the CONSULTANT.

NOTE:
ENGINEERED SHOP DRAWINGS, FOR ANY MANUFACTURED COMPONENT FORMING PART OF THE BUILDING (i.e. ENGINEERED ROOF TRUSSES, ENGINEERED FLOOR JOISTS, TIMERS, ETC.) MUST BE SUBMITTED TO HANNA GHOBRIAL & ASSOCIATES, LTD. FOR REVIEW AND APPROVAL. IF ENGINEERED SHOP DRAWINGS ARE NOT SUBMITTED AND APPROVED, HANNA GHOBRIAL & ASSOCIATES, LTD. WILL NOT BE RESPONSIBLE FOR ANY ASSOCIATED COSTS OR DAMAGES.

THE CONTRACTOR SHALL CHECK AND VERIFY ALL PERTINENT DIMENSIONS AND REPORT ANY DISCREPANCIES TO THE CONSULTANT BEFORE PROCEEDING WITH THE WORK.
THIS DRAWING SHALL NOT BE USED FOR CONSTRUCTION UNLESS IT IS COUNTERSIGNED BY THE CONSULTANT.
USE FIGURED DIMENSIONS ONLY.

12		
11		
10		
9		
8		
7		
6		
5		
4		
3	22/03/31	REV. PER CITY COMMENTS
2	22/02/08	FOR PERMIT
1	22/01/31	ARCH&STRU REVISION

No. Date: Issued For:

Date: OCTOBER 2021

Drawn By: H.R.

Checked By: R.J.

Project Title:

83 SANDWICH STREET BUILDING ADDITION

AMHERSTBURG, ONTARIO


Project No.: 21-0427

Sheet Title:


SECTIONS AND WALL TYPES

Sheet No.:


A-5.0

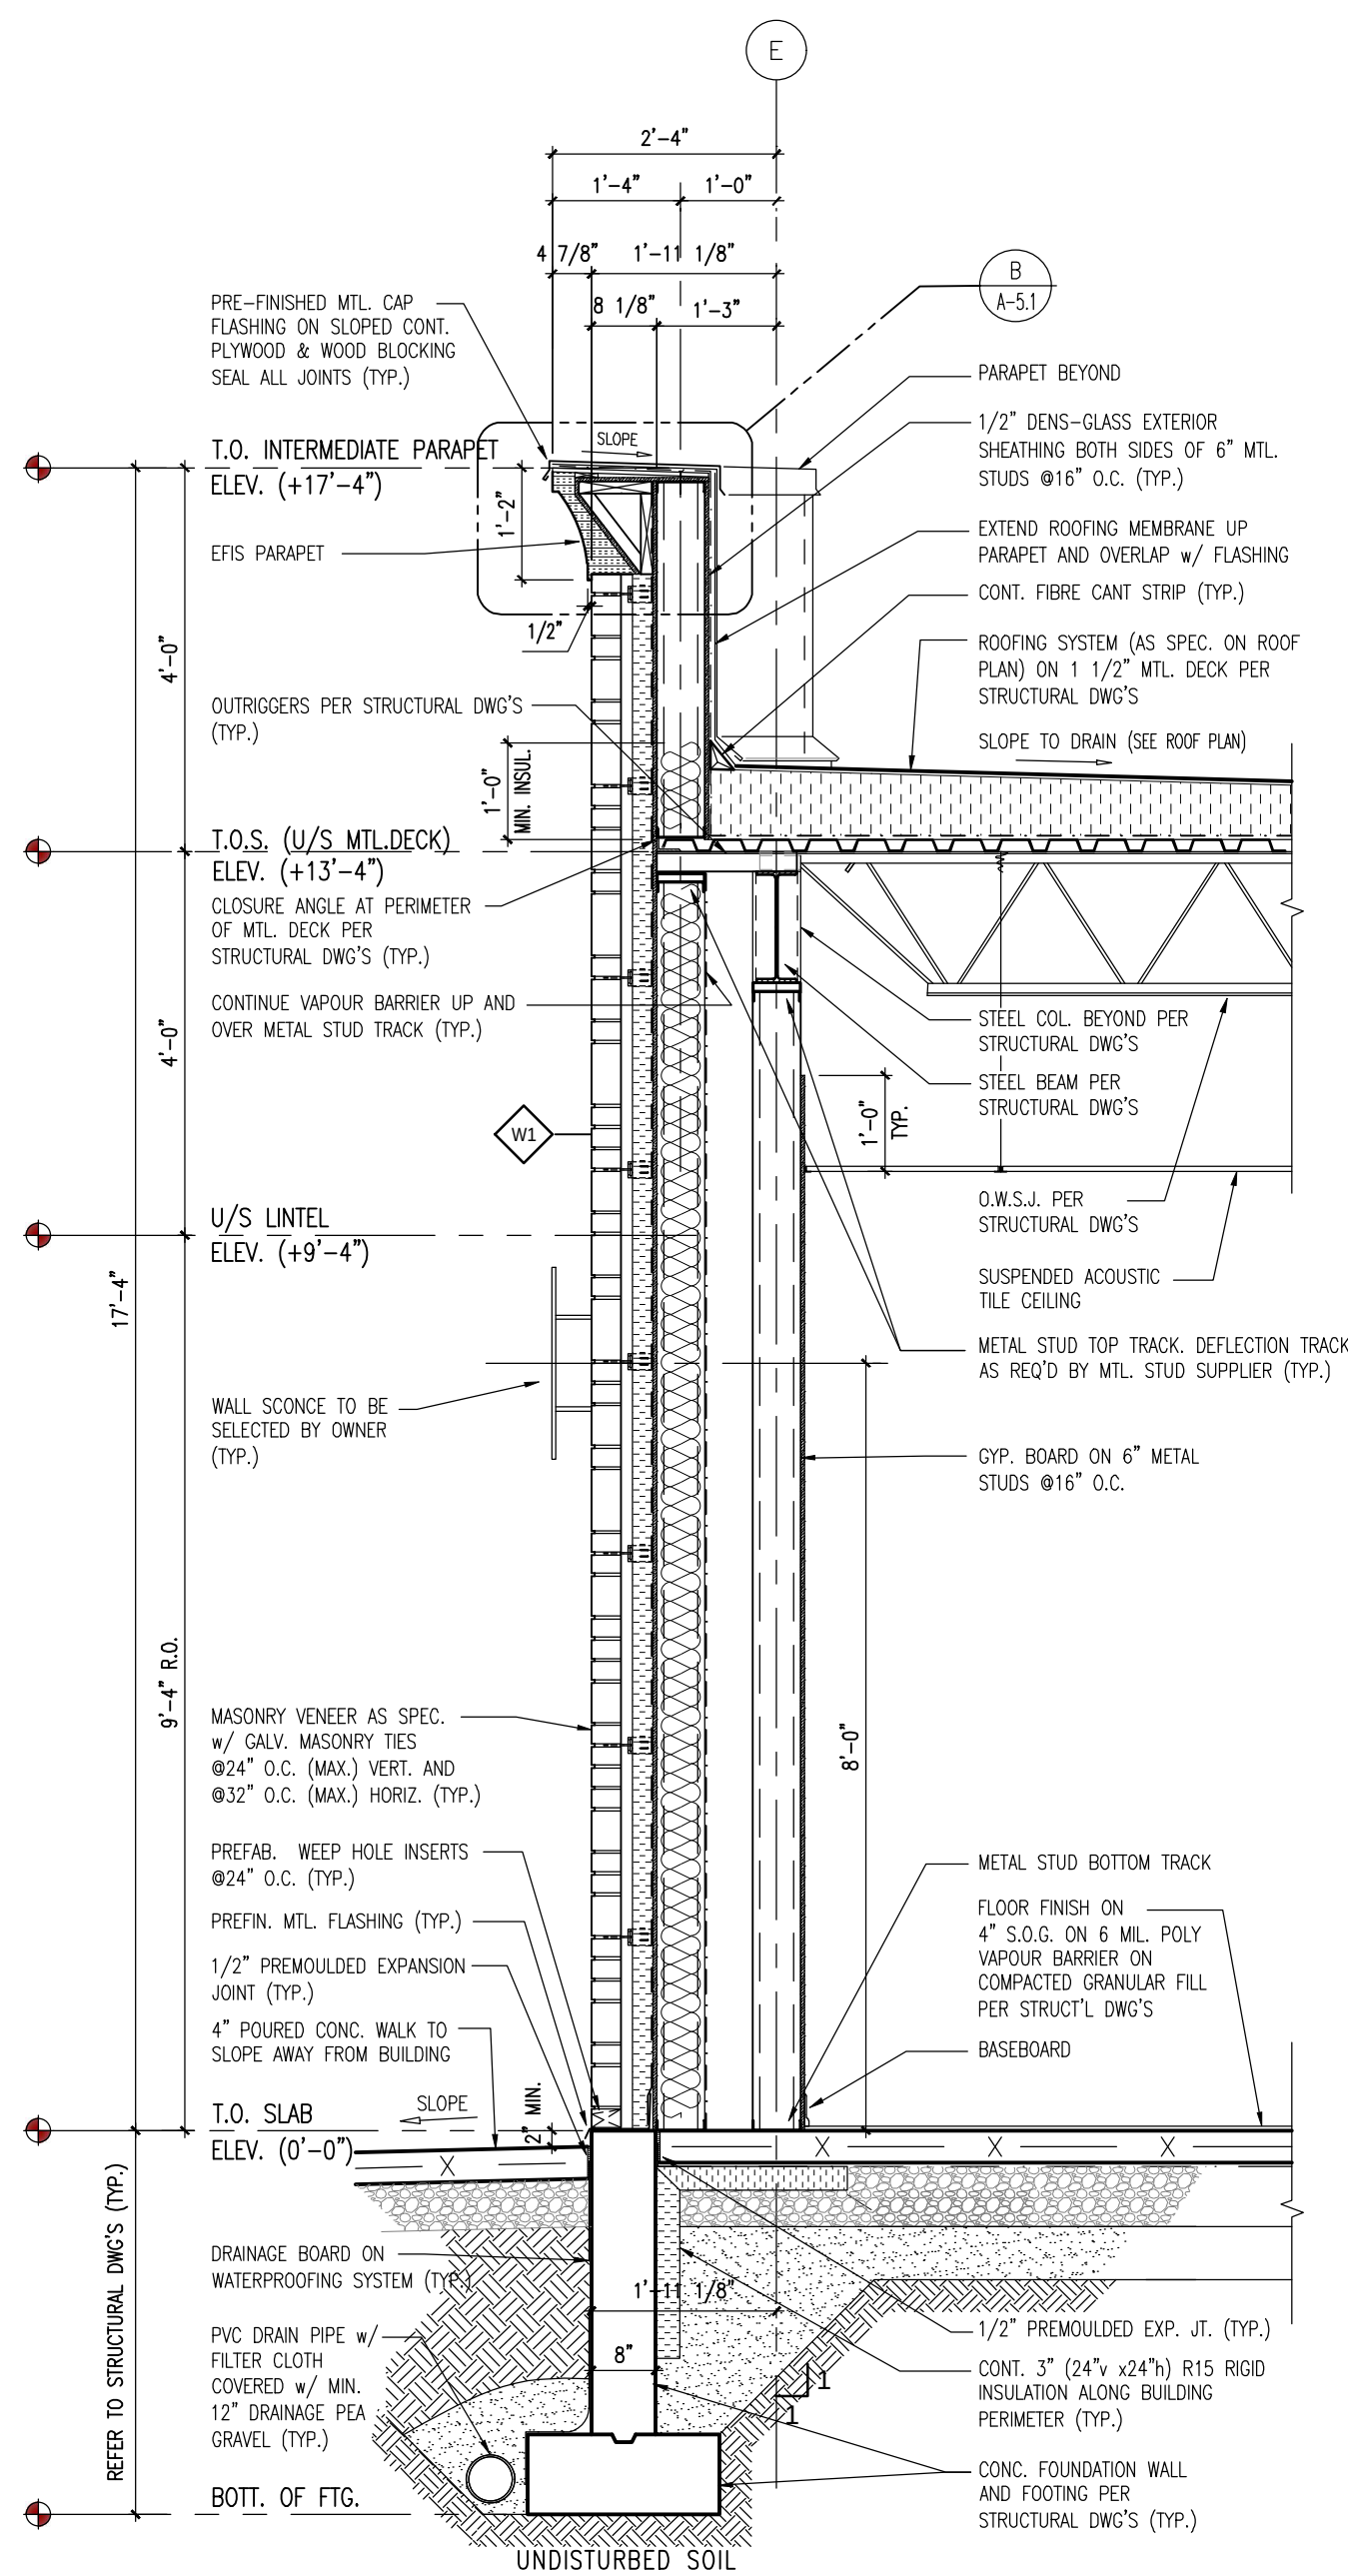


1 SECTION
A-2.0, A-3.0 SCALE: 1/2" = 1'-0"

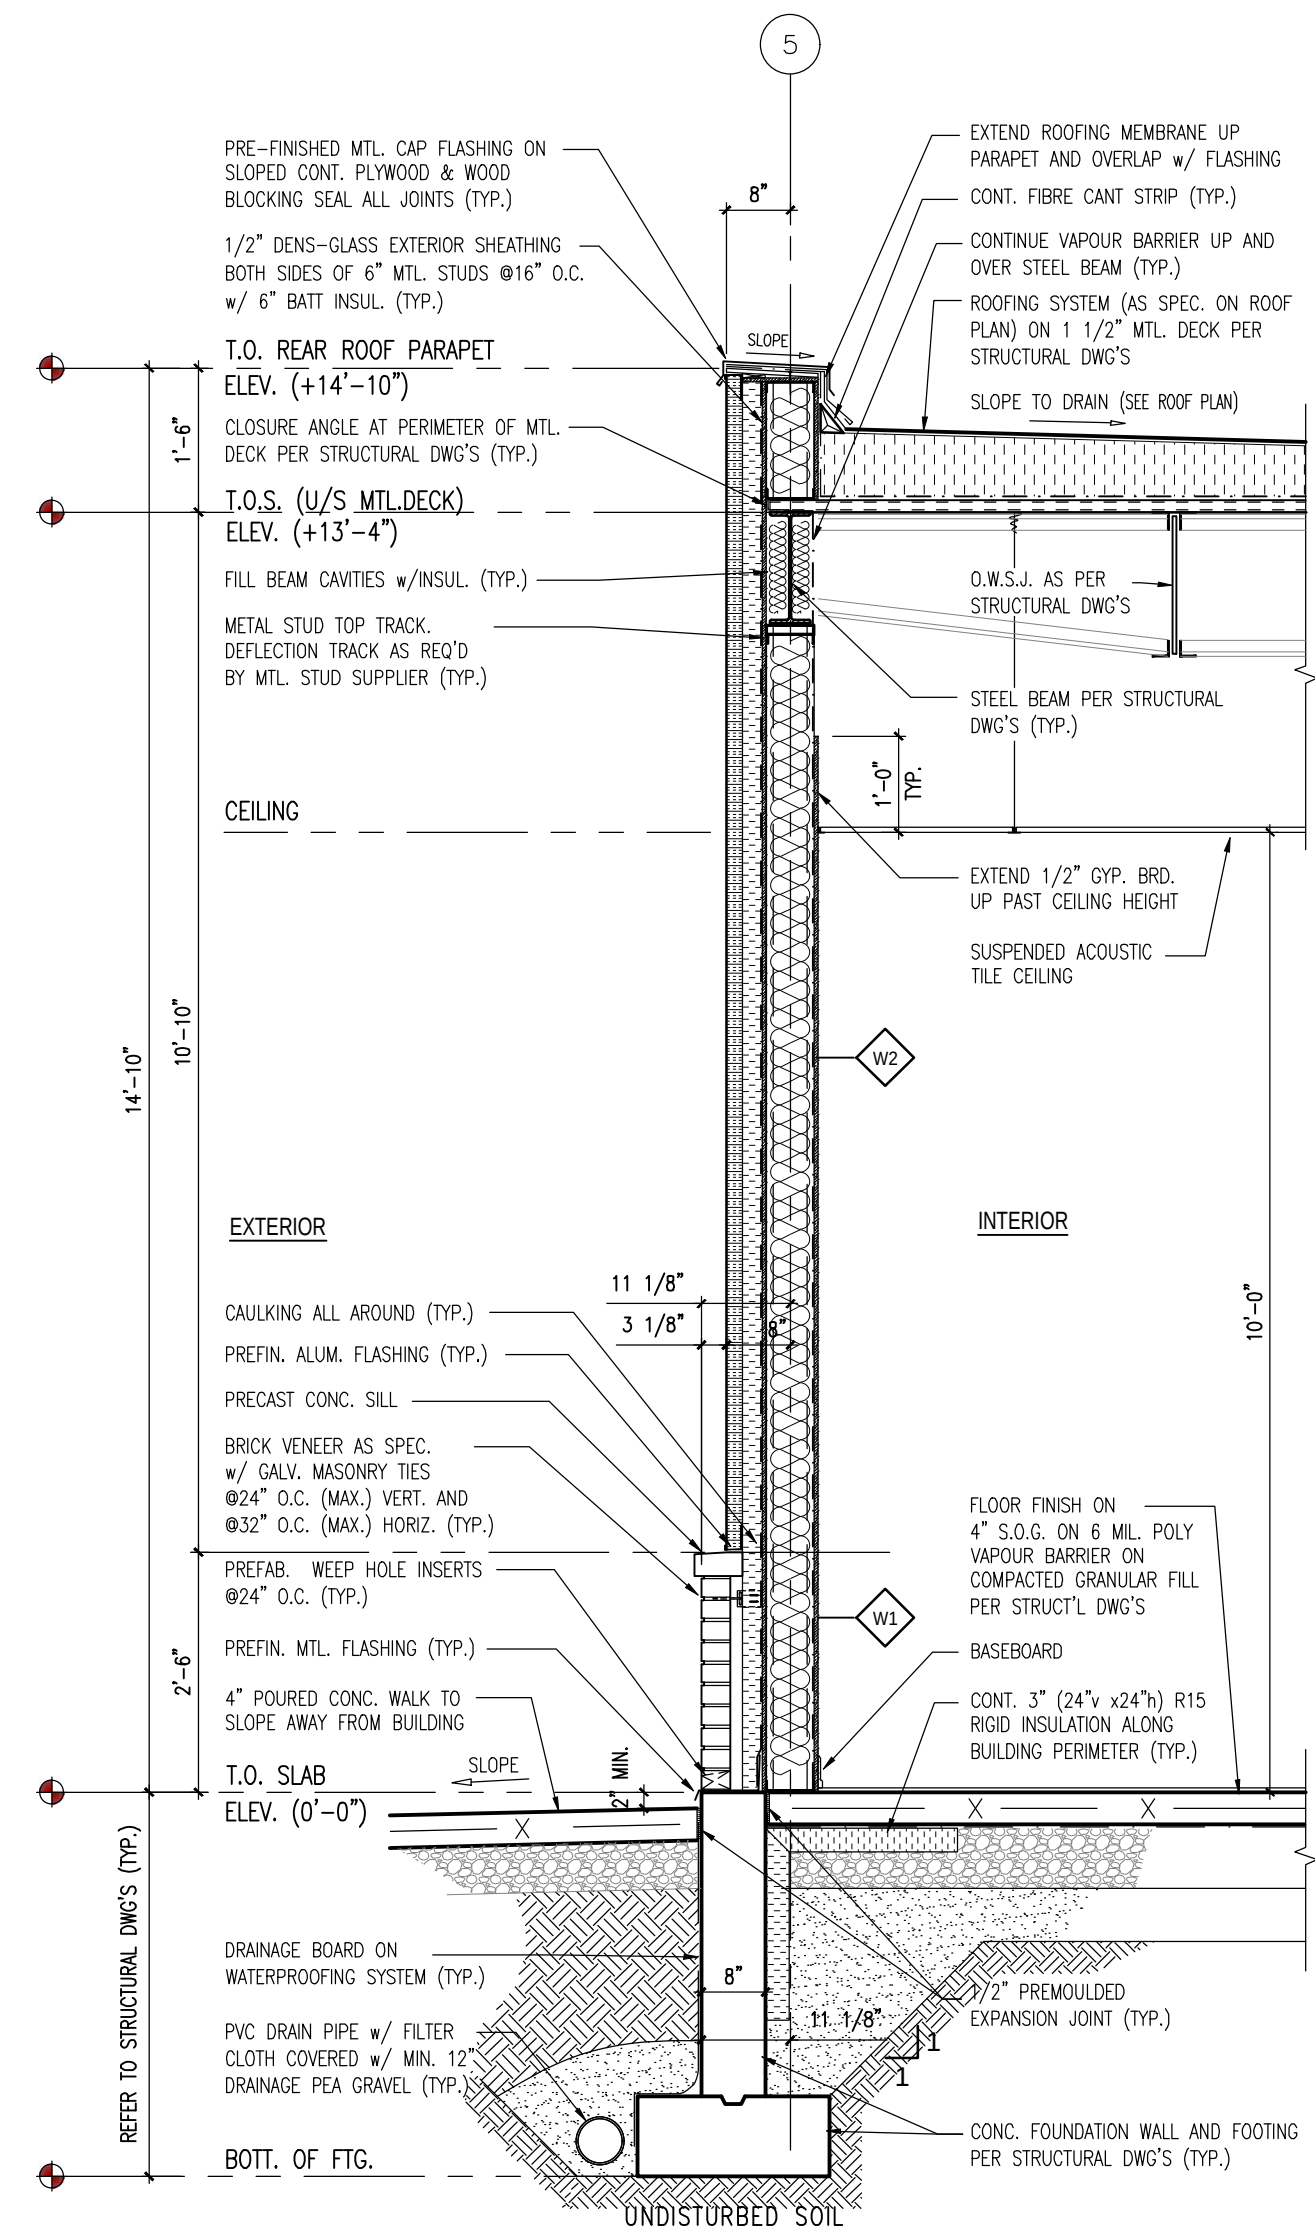


2 SECTION
A-2.0, A-3.0 SCALE: 1/2" = 1'-0"

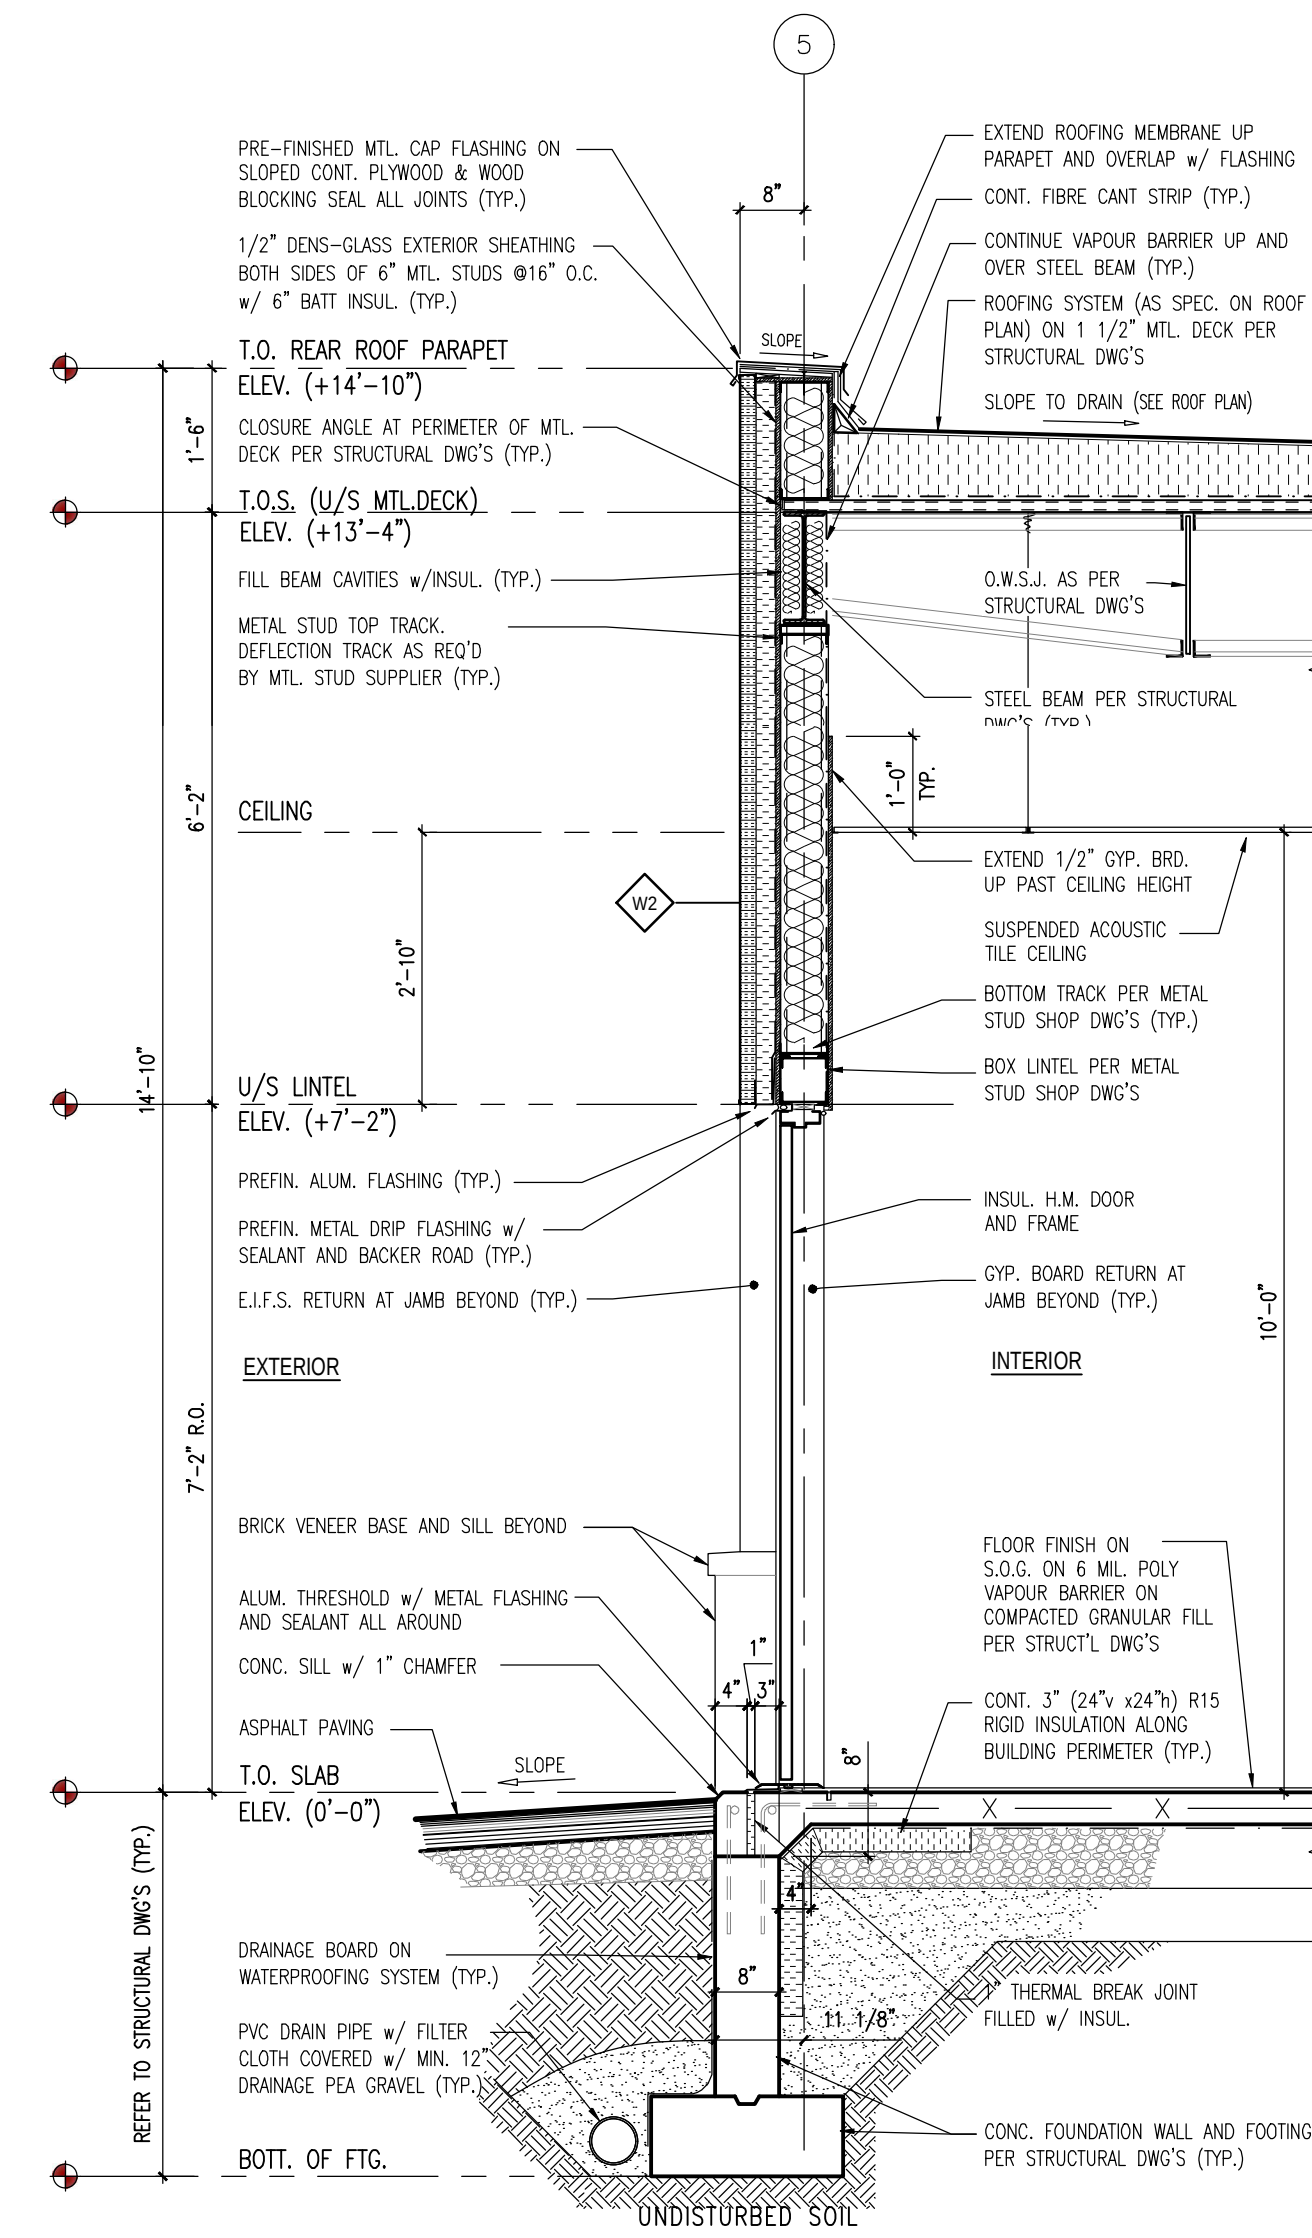


3 SECTION
A-2.0, A-3.0 SCALE: 1/2" = 1'-0"

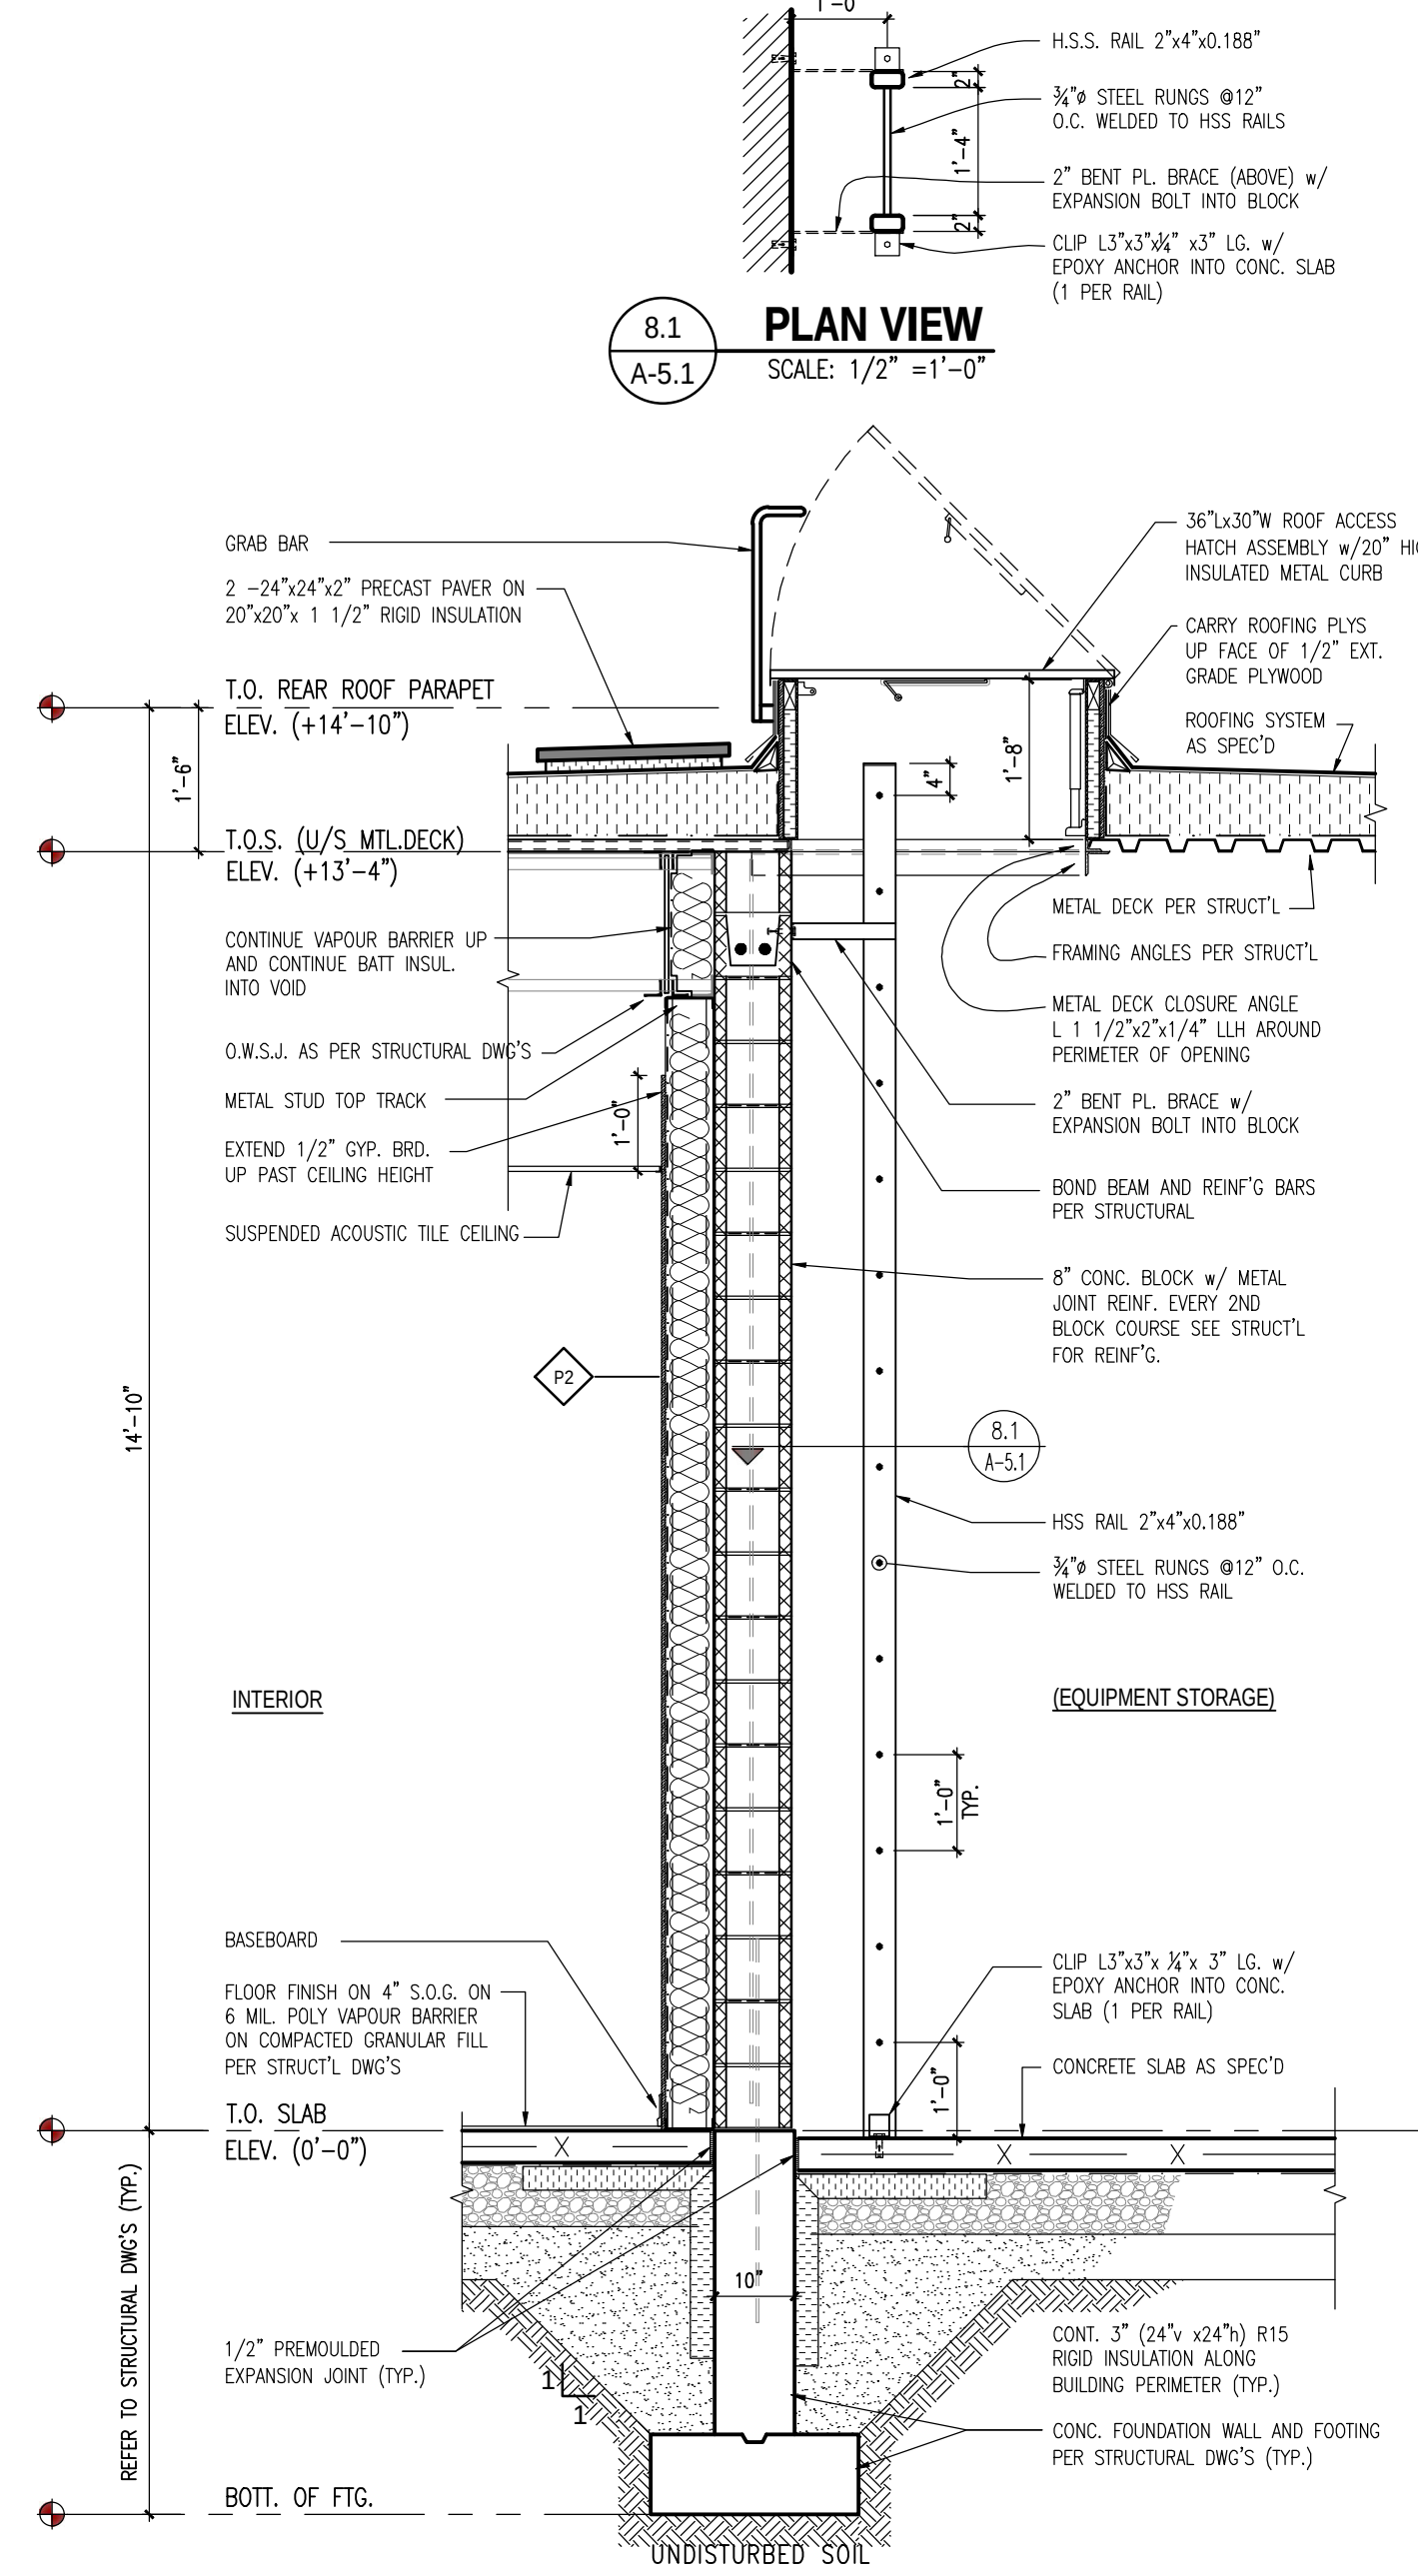


4 SECTION
A-2.0, A-3.0 SCALE: 1/2" = 1'-0"

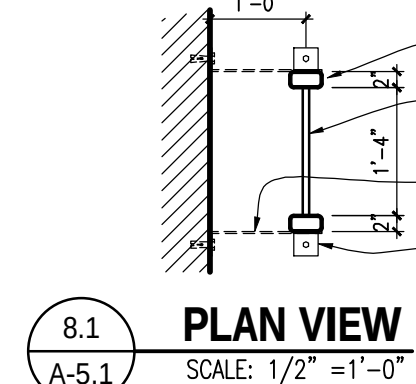


8.1 PLAN VIEW
A-5.1 SCALE: 1/2" = 1'-0"

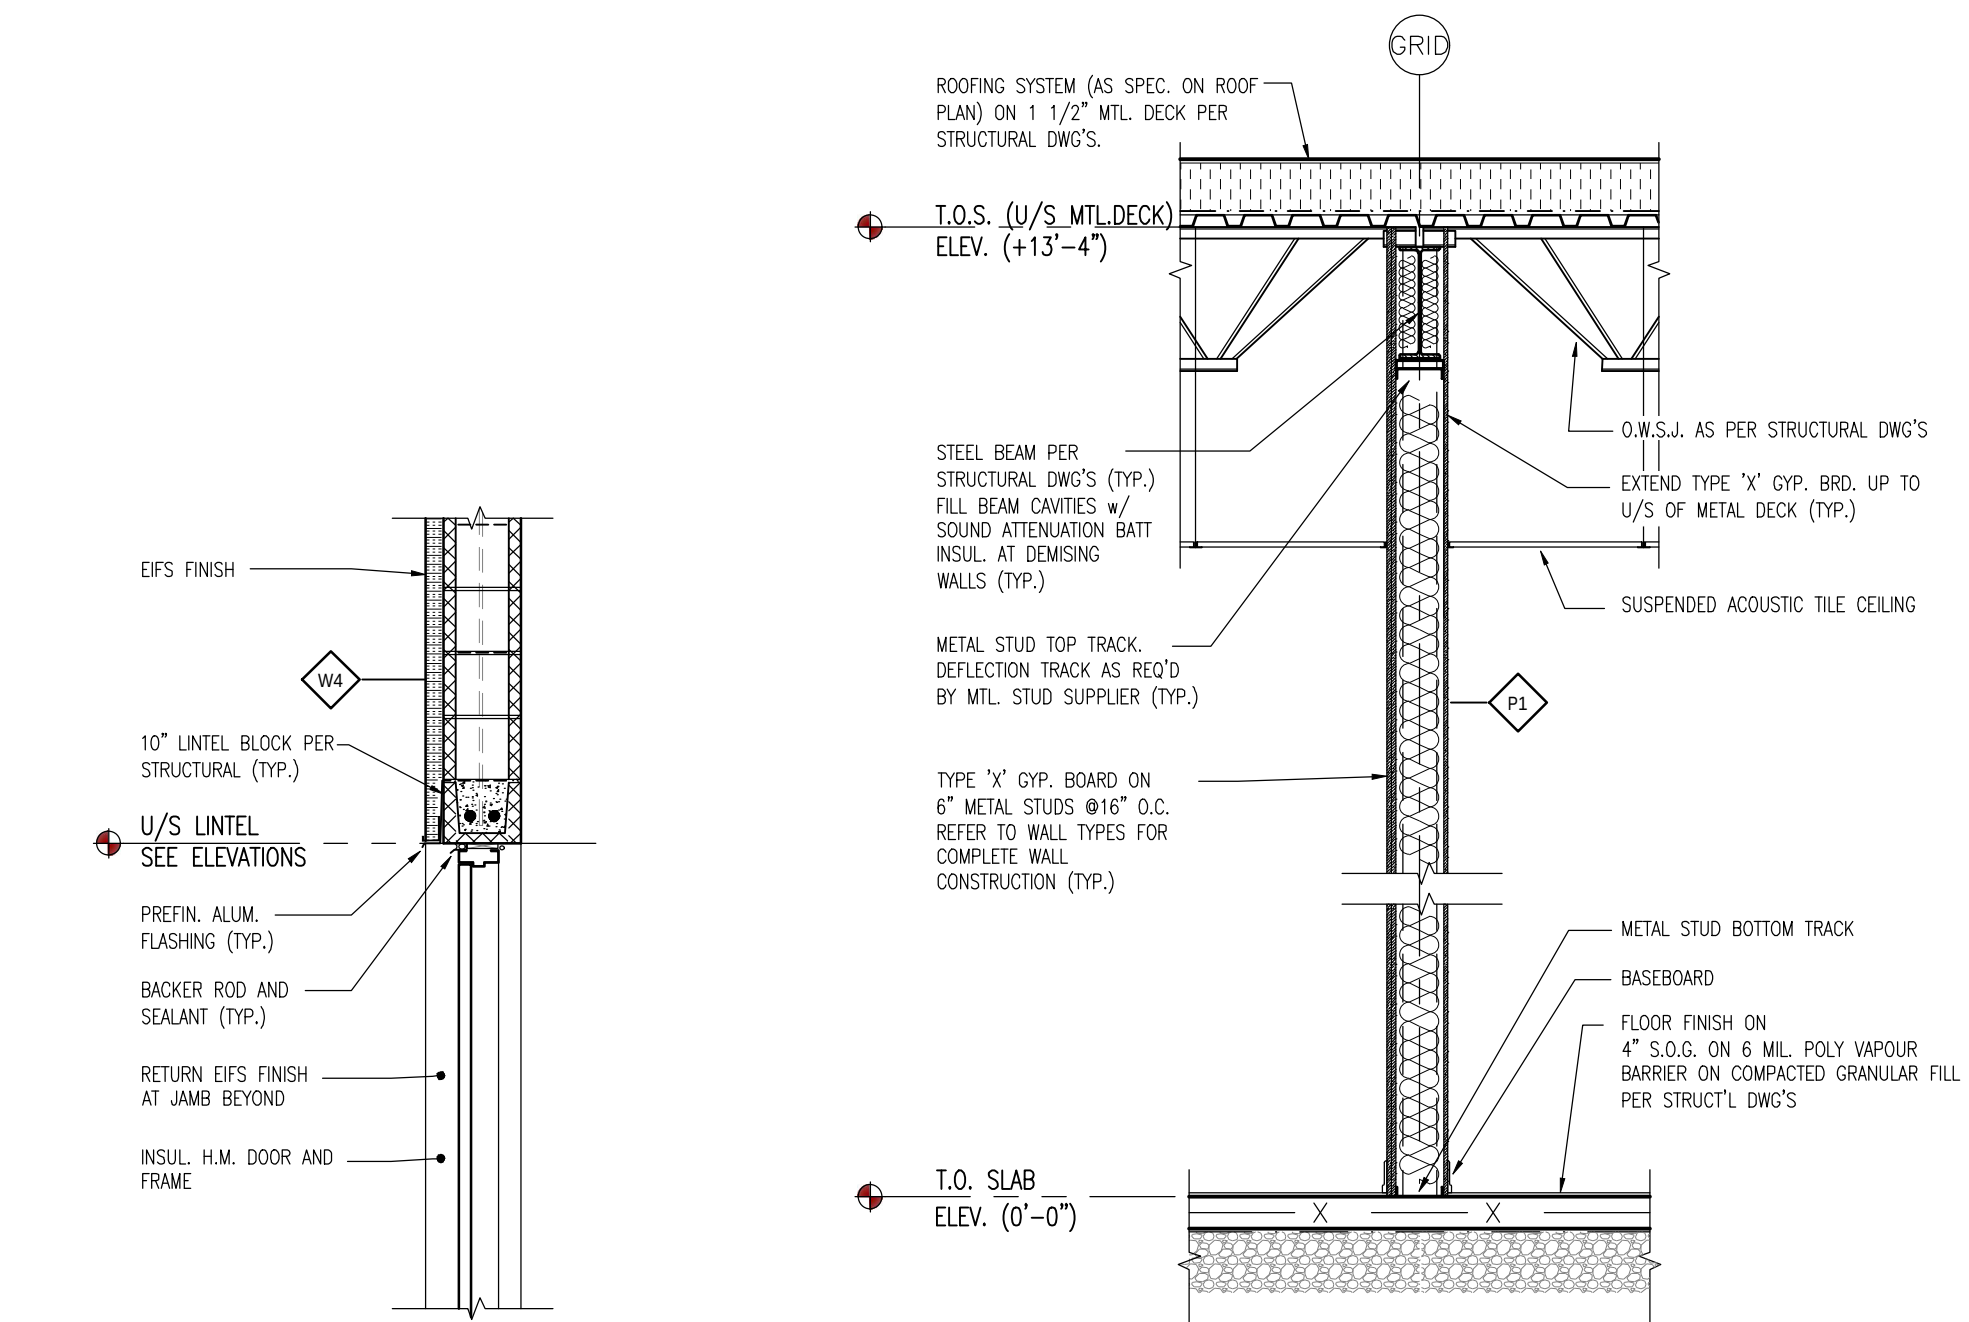


5 SECTION
A-2.0 SCALE: 1/2" = 1'-0"

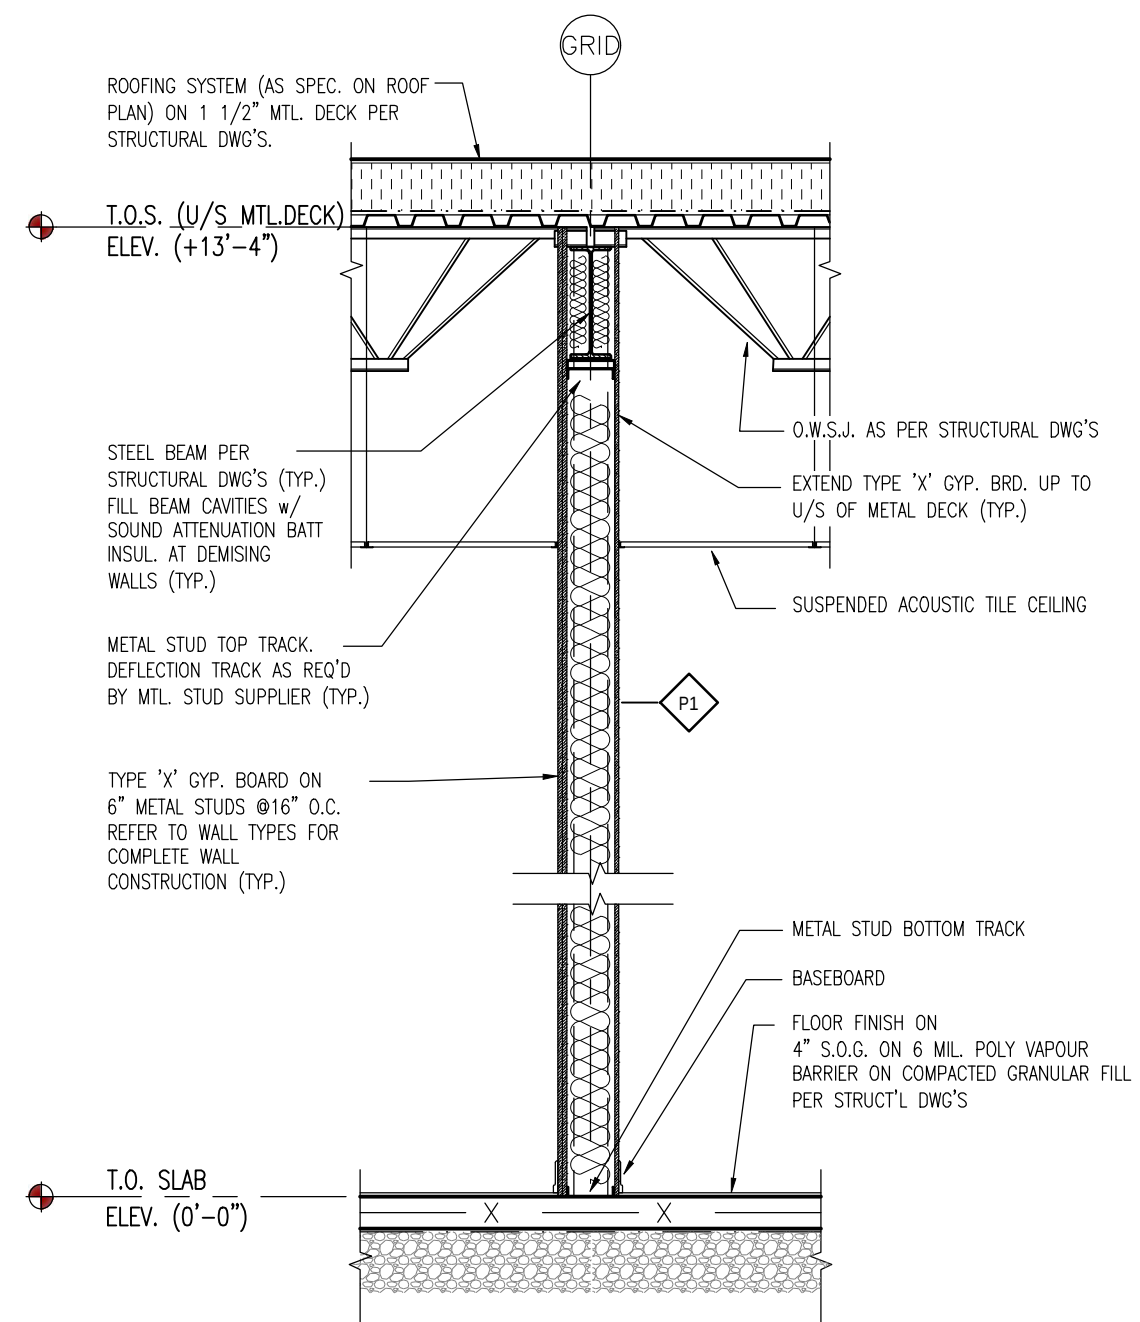


6 SECTION
A-2.0, A-3.0 SCALE: 1/2" = 1'-0"

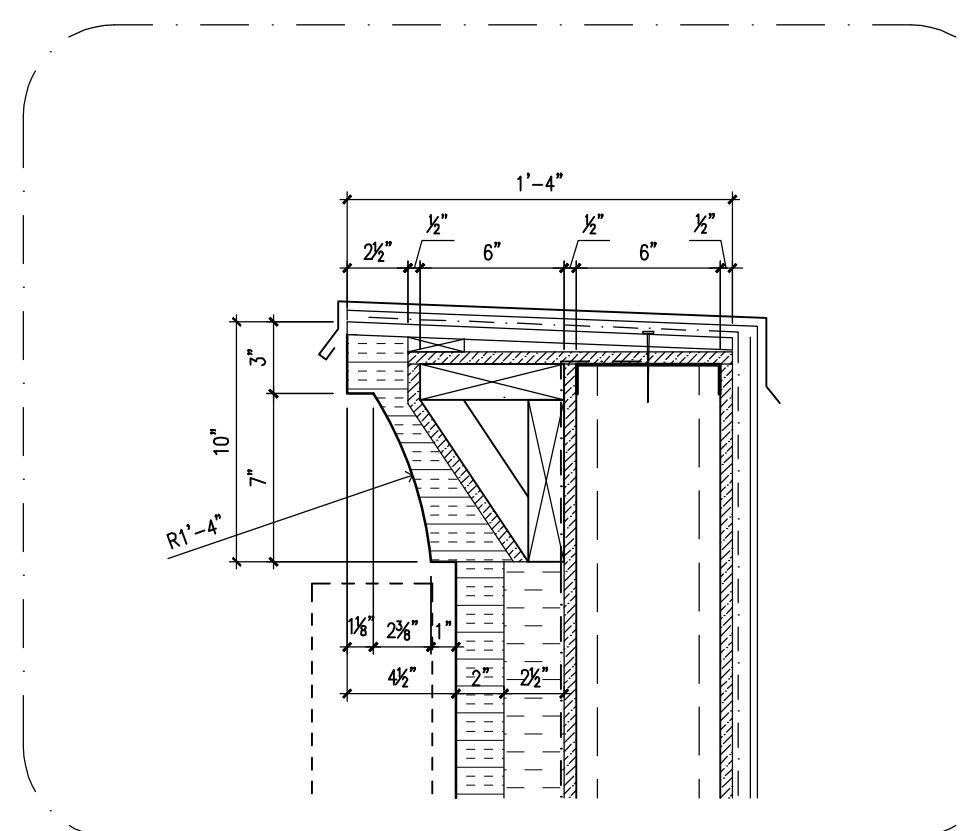


A ENLARGED DETAIL
A-5.0 SCALE: 1 1/2" = 1'-0"

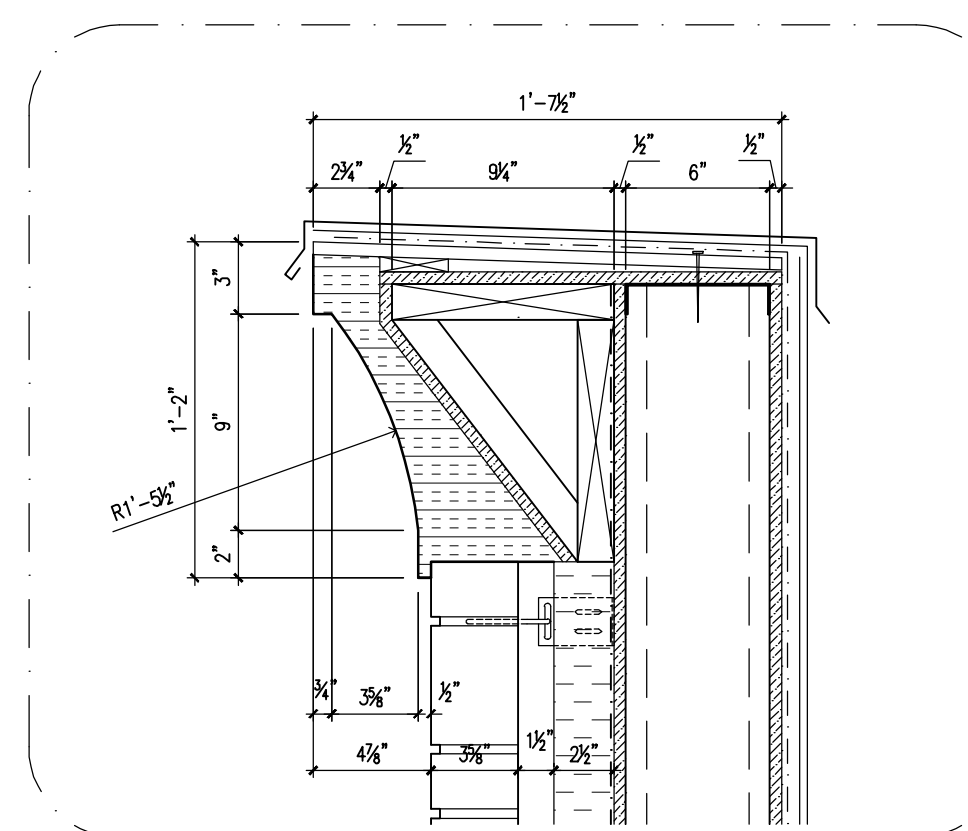

B ENLARGED DETAIL
A-5.0, A-5.1 SCALE: 1 1/2" = 1'-0"

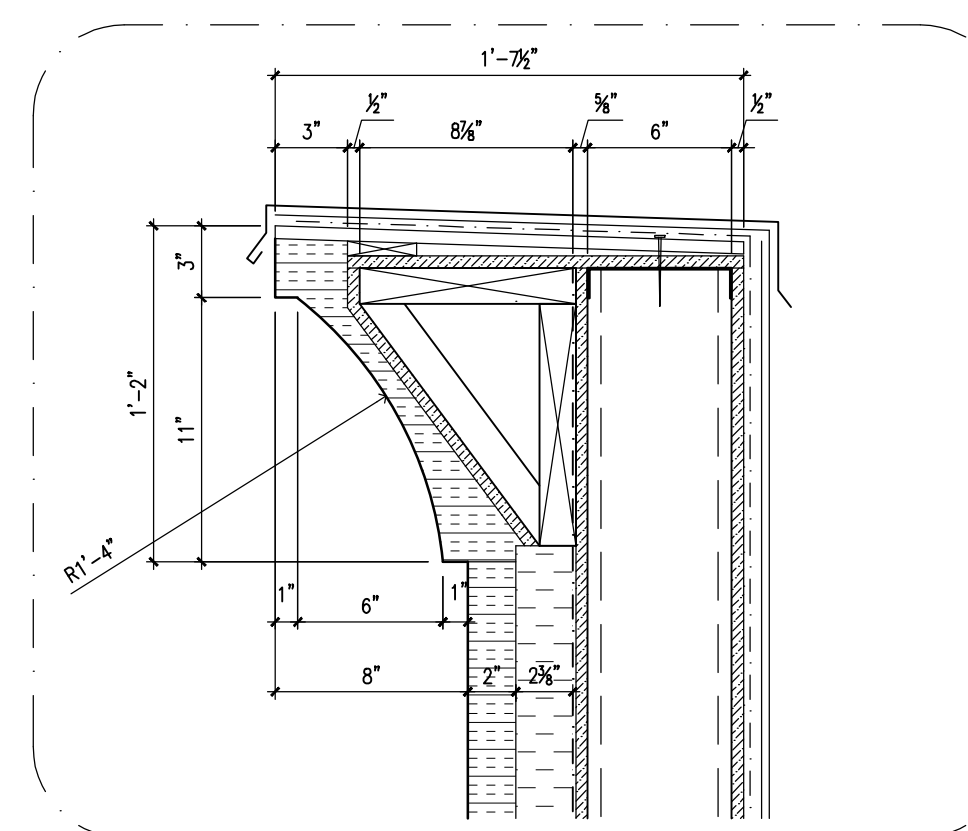

C ENLARGED DETAIL
A-5.0 SCALE: 1 1/2" = 1'-0"

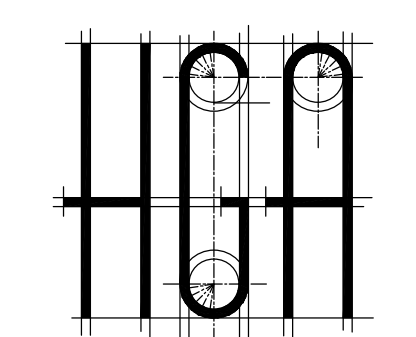




**HANNA, GHOBRIAL
AND ASSOCIATES LTD.**
engineering
architecture
3100 Temple Drive
Windsor, ON N8W 5J6
(519) 945-7373 FAX-5636




This drawing shall not be used for construction unless it is countersigned by the CONSULTANT.
NOTE: ENGINEERED SHOP DRAWINGS, FOR ANY MANUFACTURED COMPONENT FORMING PART OF THE BUILDING (i.e. ENGINEERED ROOF TRUSSES, ENGINEERED FLOOR JOISTS, TRIMERS, ETC.) MUST BE SUBMITTED TO HANNA, GHOBRIAL & ASSOCIATES, LTD. FOR REVIEW AND APPROVAL. IF ENGINEERED SHOP DRAWINGS ARE NOT SUBMITTED AND APPROVED, HANNA, GHOBRIAL & ASSOCIATES, LTD. WILL NOT BE RESPONSIBLE FOR ANY ASSOCIATED COSTS OR DAMAGES.

ALL DRAWINGS, SPECIFICATIONS AND OTHER RELATED DOCUMENTS ARE THE COPYRIGHT PROPERTY OF THE CONSULTANT AND SHALL BE RETURNED UPON REQUEST. REPRODUCTION OF DRAWINGS AND RELATED DOCUMENTS, IN WHOLE OR IN PART, IS FORBIDDEN WITHOUT THE WRITTEN PERMISSION OF THE CONSULTANT. THE CONTRACTOR SHALL CHECK AND VERIFY ALL PERTINENT DIMENSIONS AND REPORT ANY DISCREPANCIES TO THE CONSULTANT BEFORE PROCEEDING WITH THE WORK. THIS DRAWING SHALL NOT BE USED FOR CONSTRUCTION UNLESS IT IS COUNTERSIGNED BY THE CONSULTANT. THIS DRAWING IS NOT TO BE SCALED. USE FIGURED DIMENSIONS ONLY.


12		
11		
10		
9		
8		
7		
6		
5		
4		
3	22/03/31	REV. PER CITY COMMENTS
2	22/02/08	FOR PERMIT
1	22/01/31	ARCH&STRU REVISION
No.	Date:	Issued For:
	Date:	OCTOBER 2021
	Drawn By:	H.R.
	Checked By:	R.J.
	Project Title:	83 SANDWICH STREET BUILDING ADDITION
	Project No.:	AMHERSTBURG, ONTARIO
		21-0427
	Sheet Title:	SECTIONS
	Sheet No.:	A-5.1

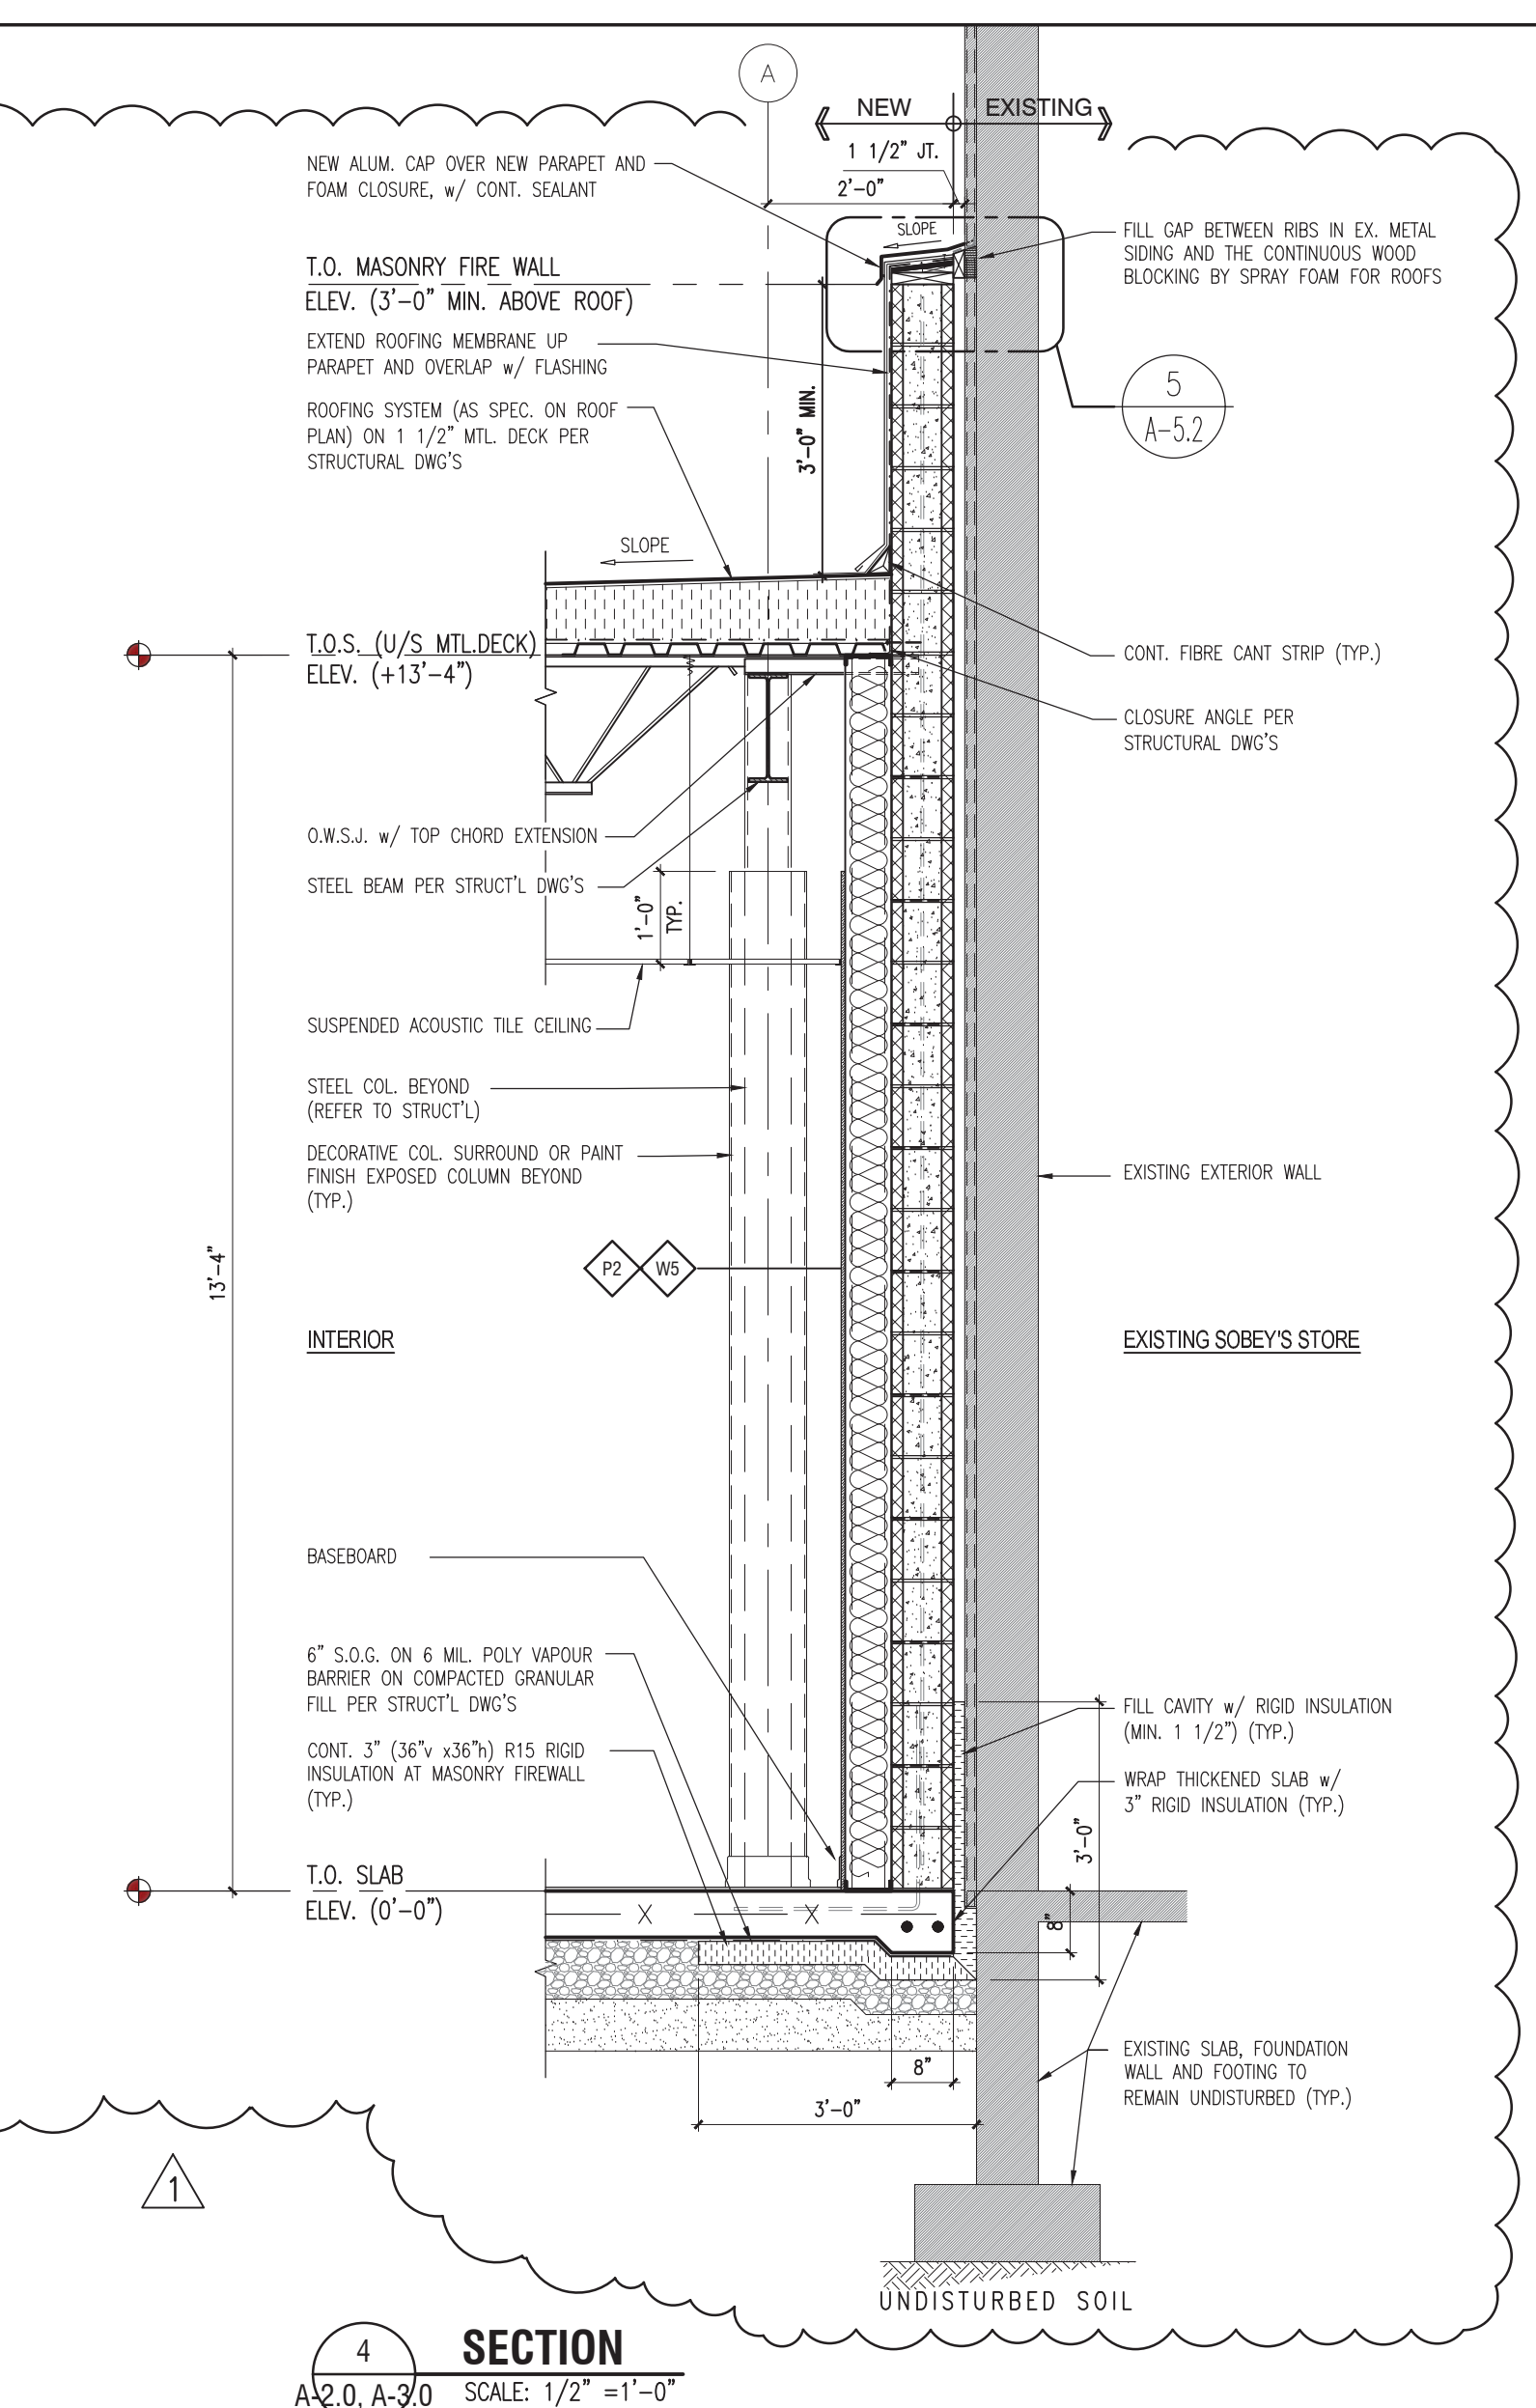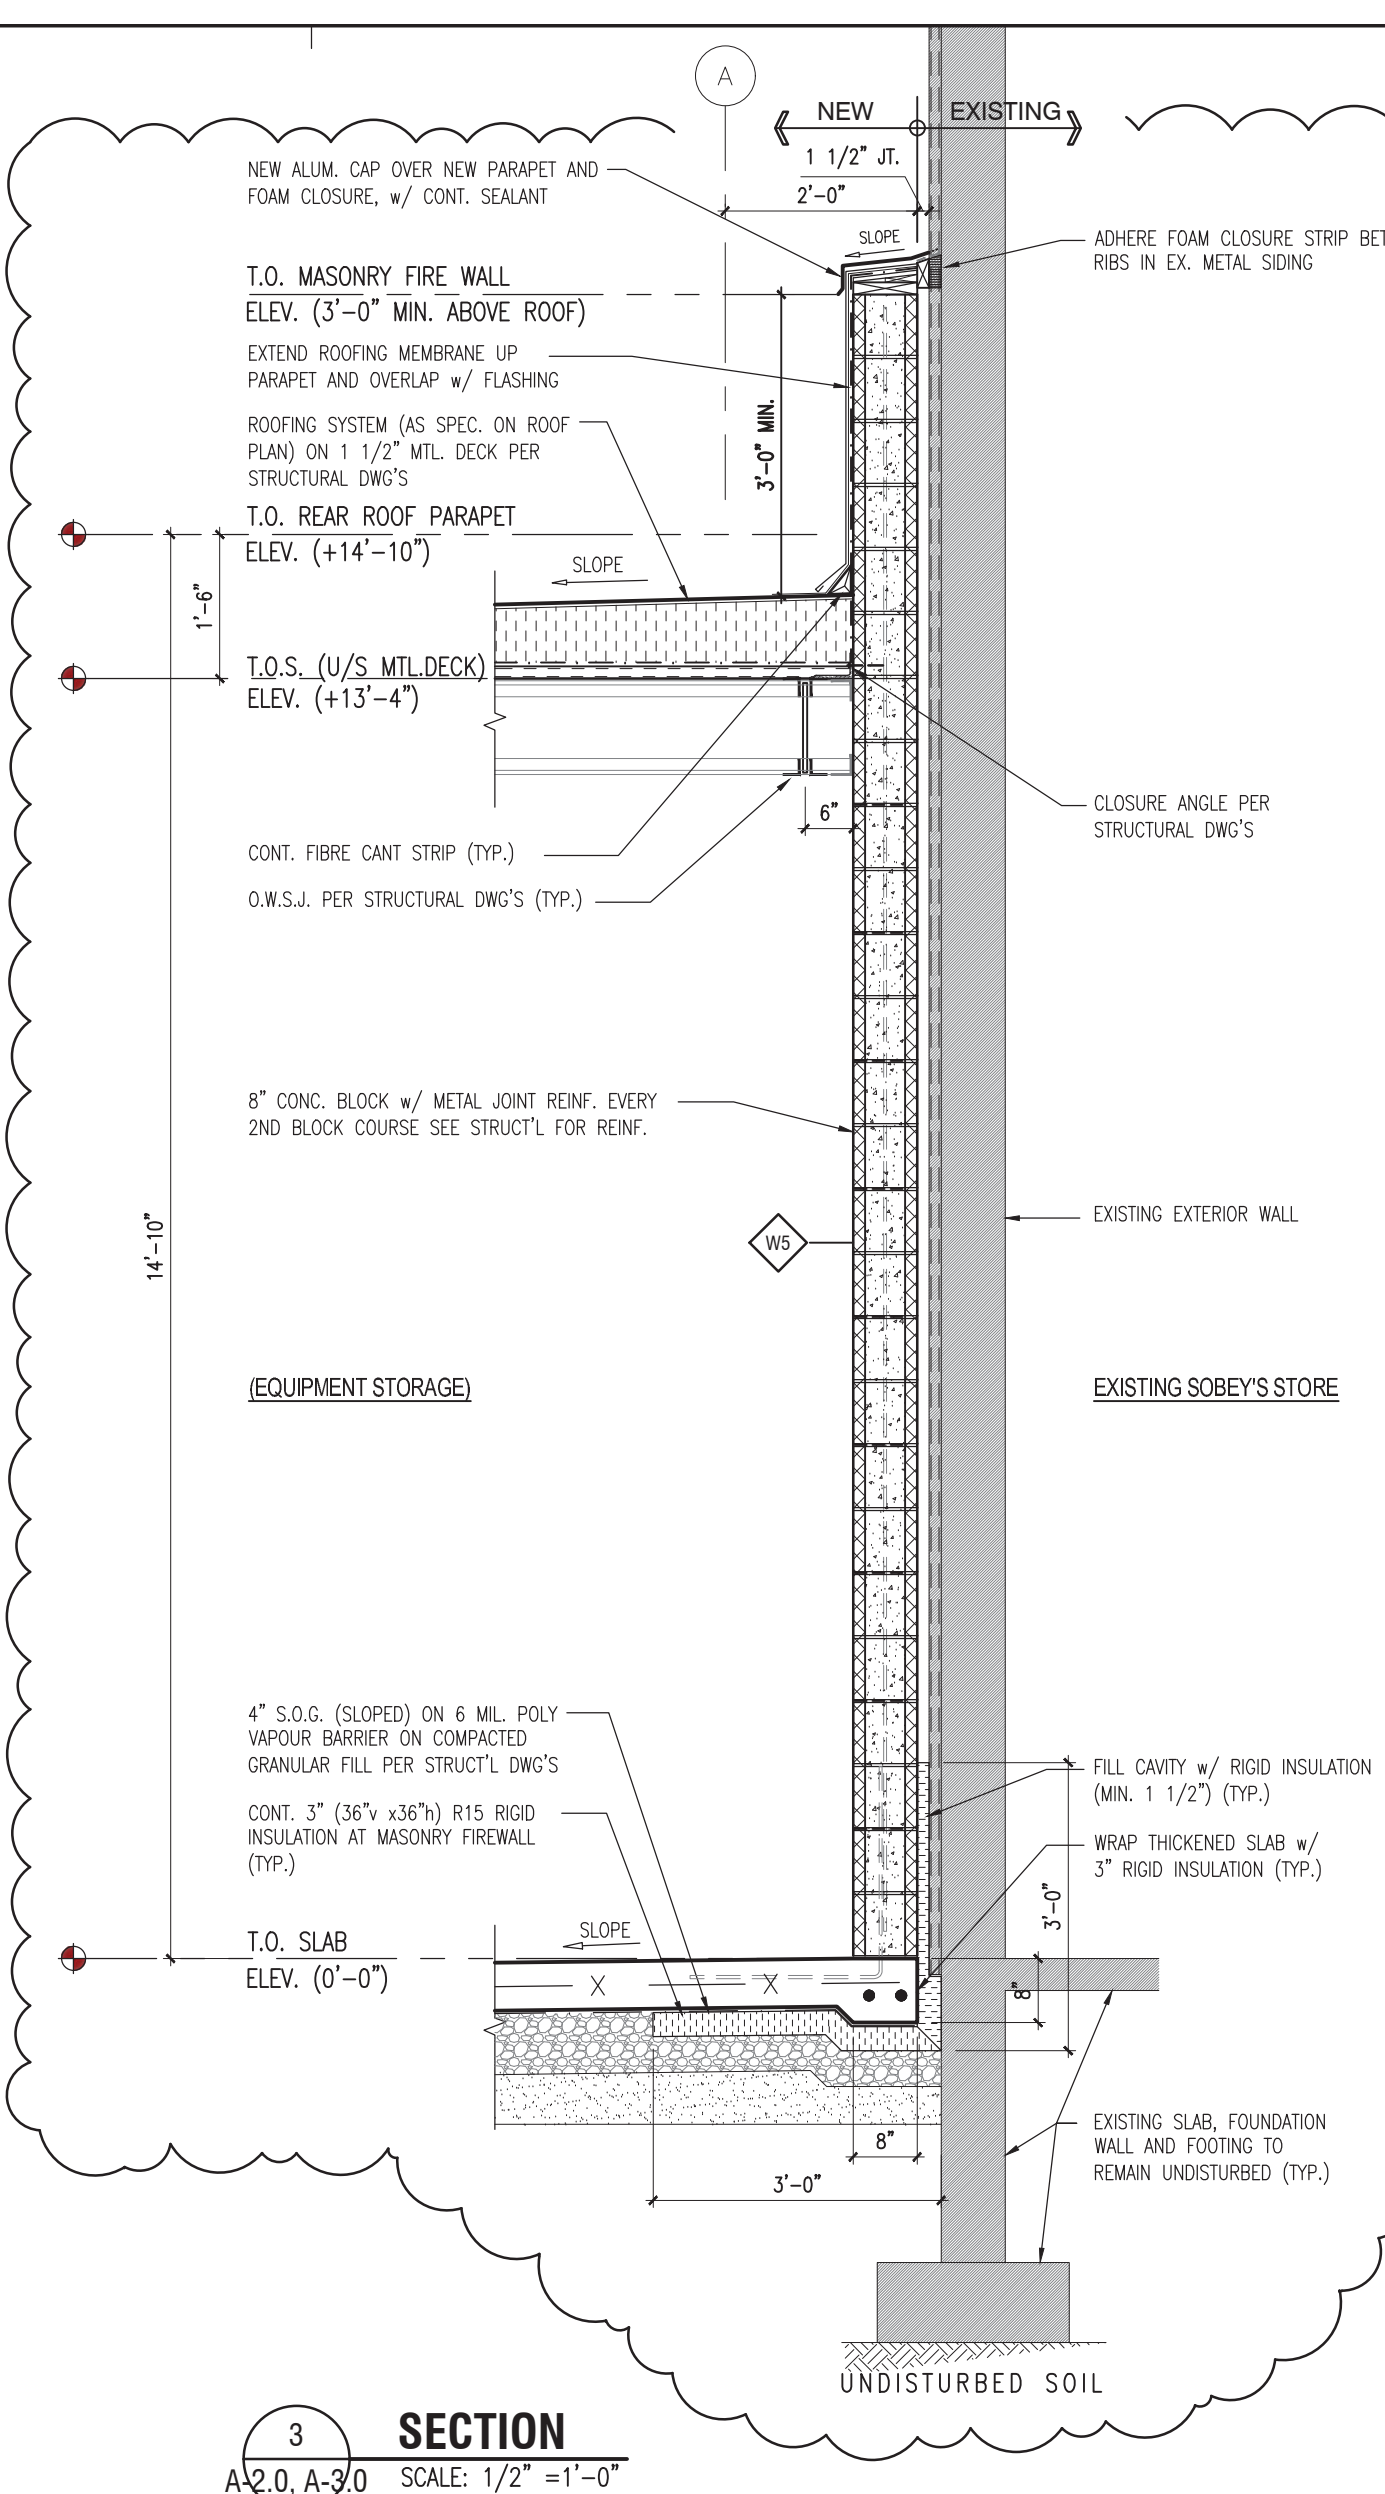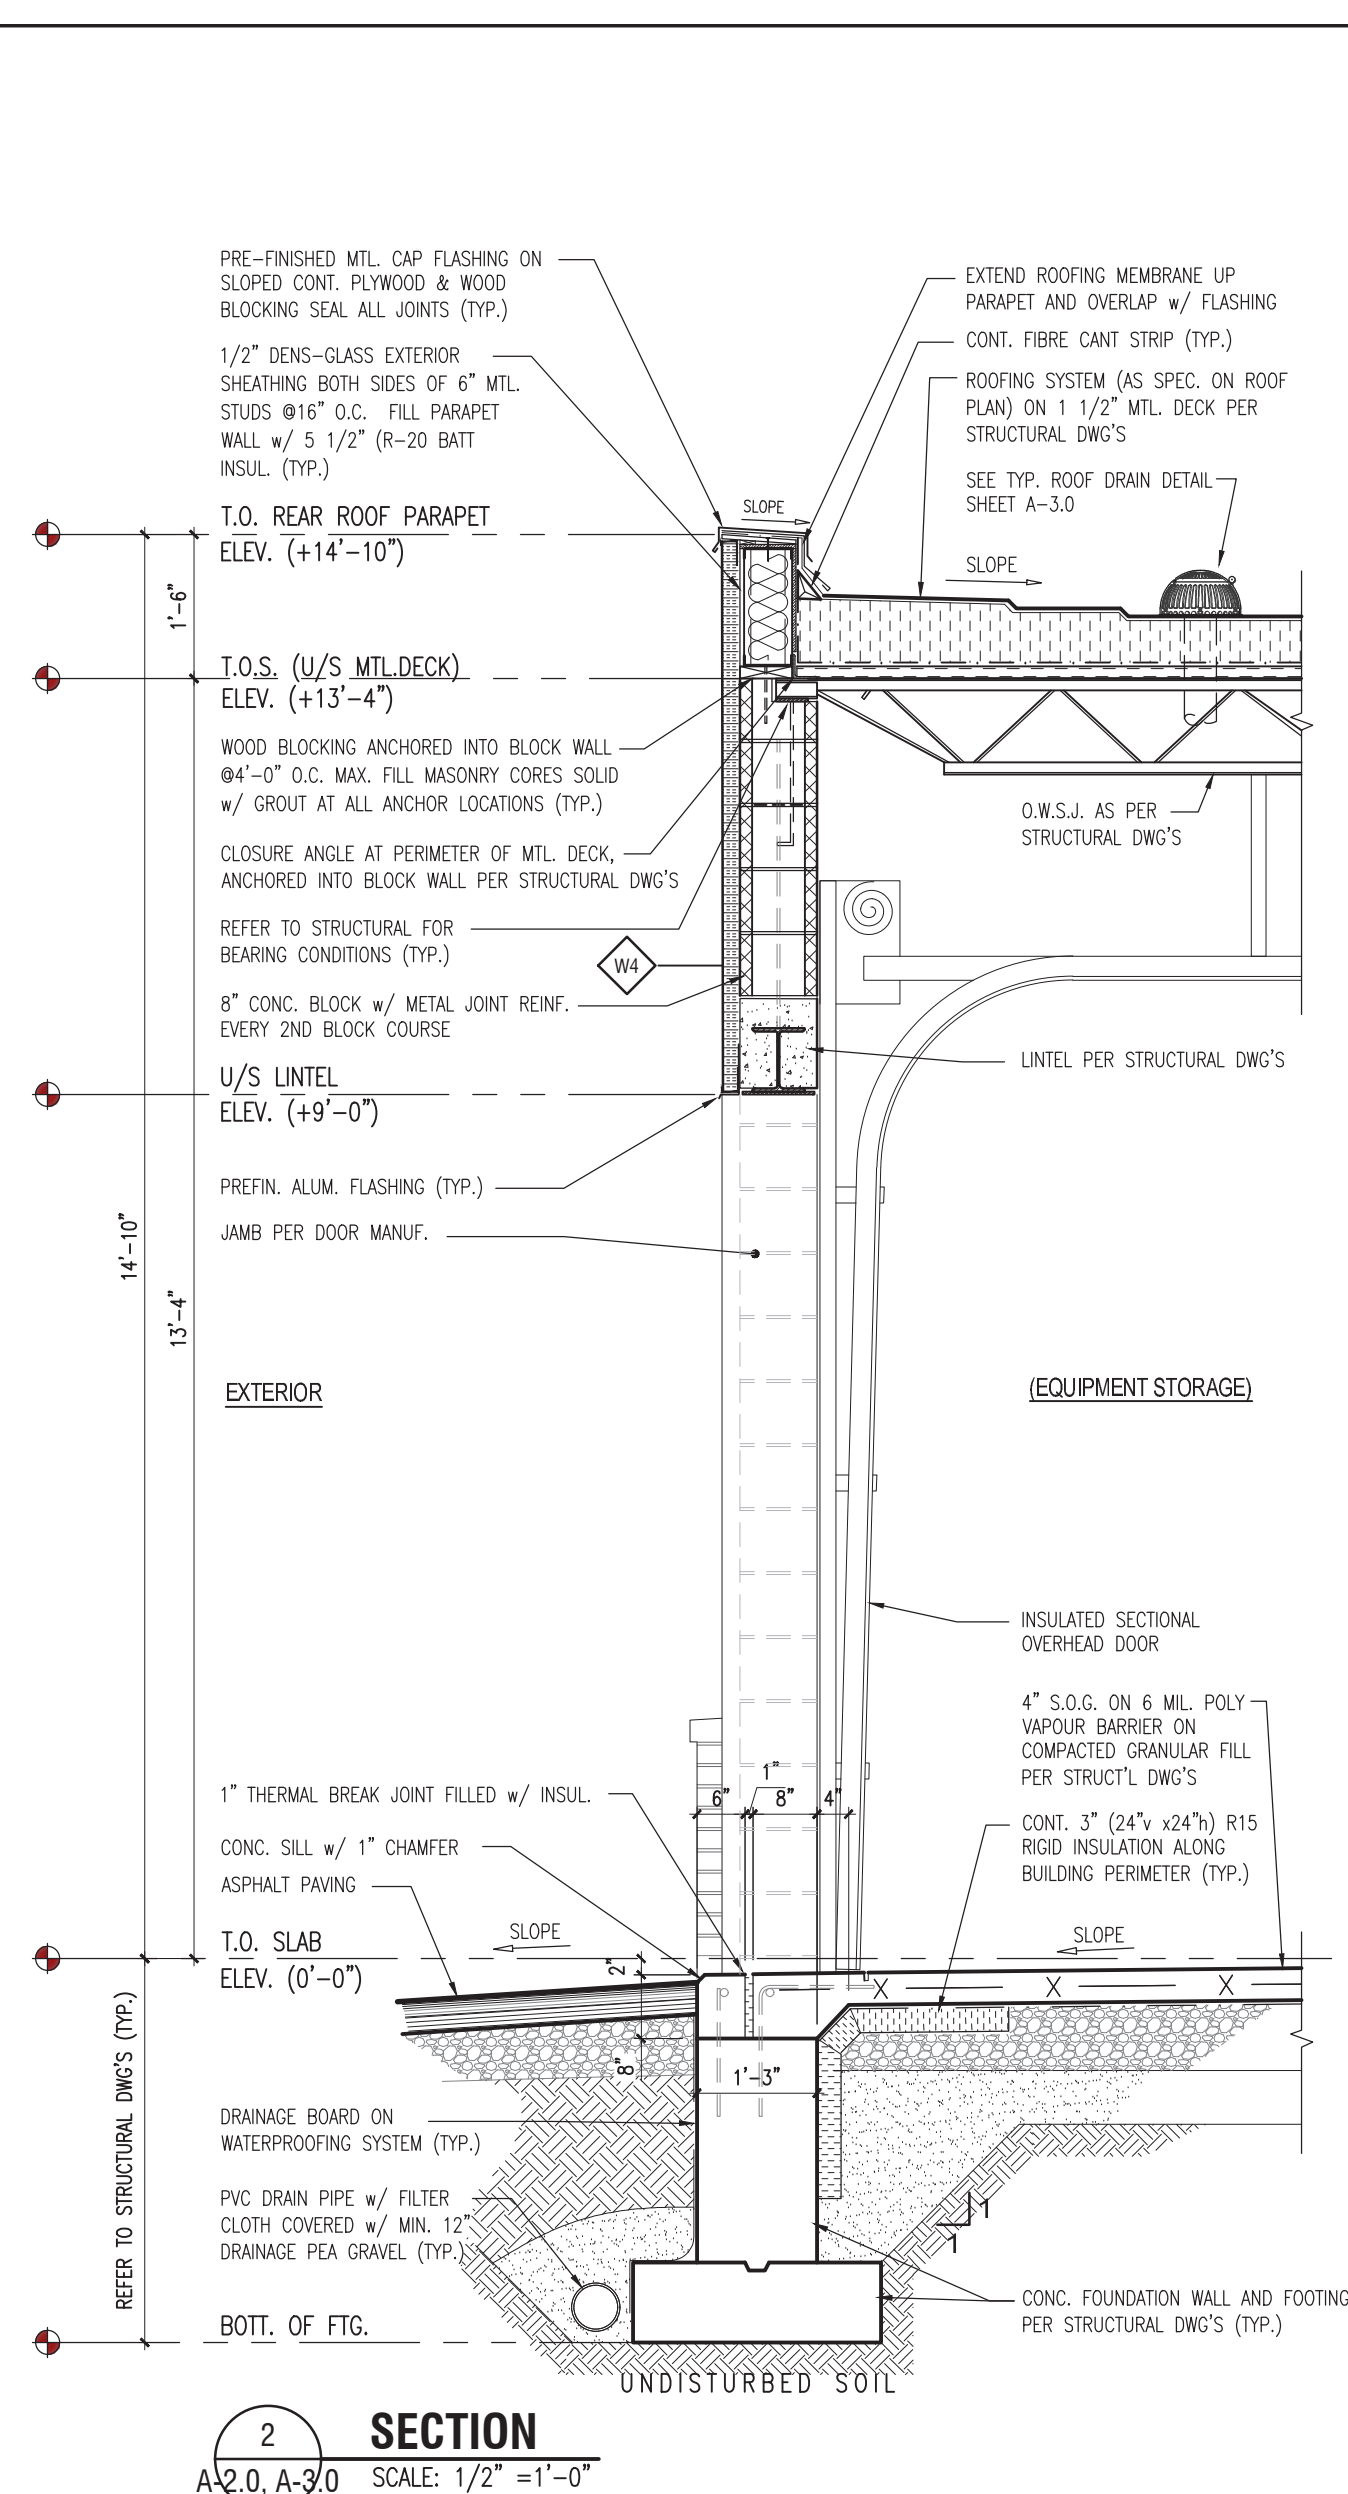


A-5.2

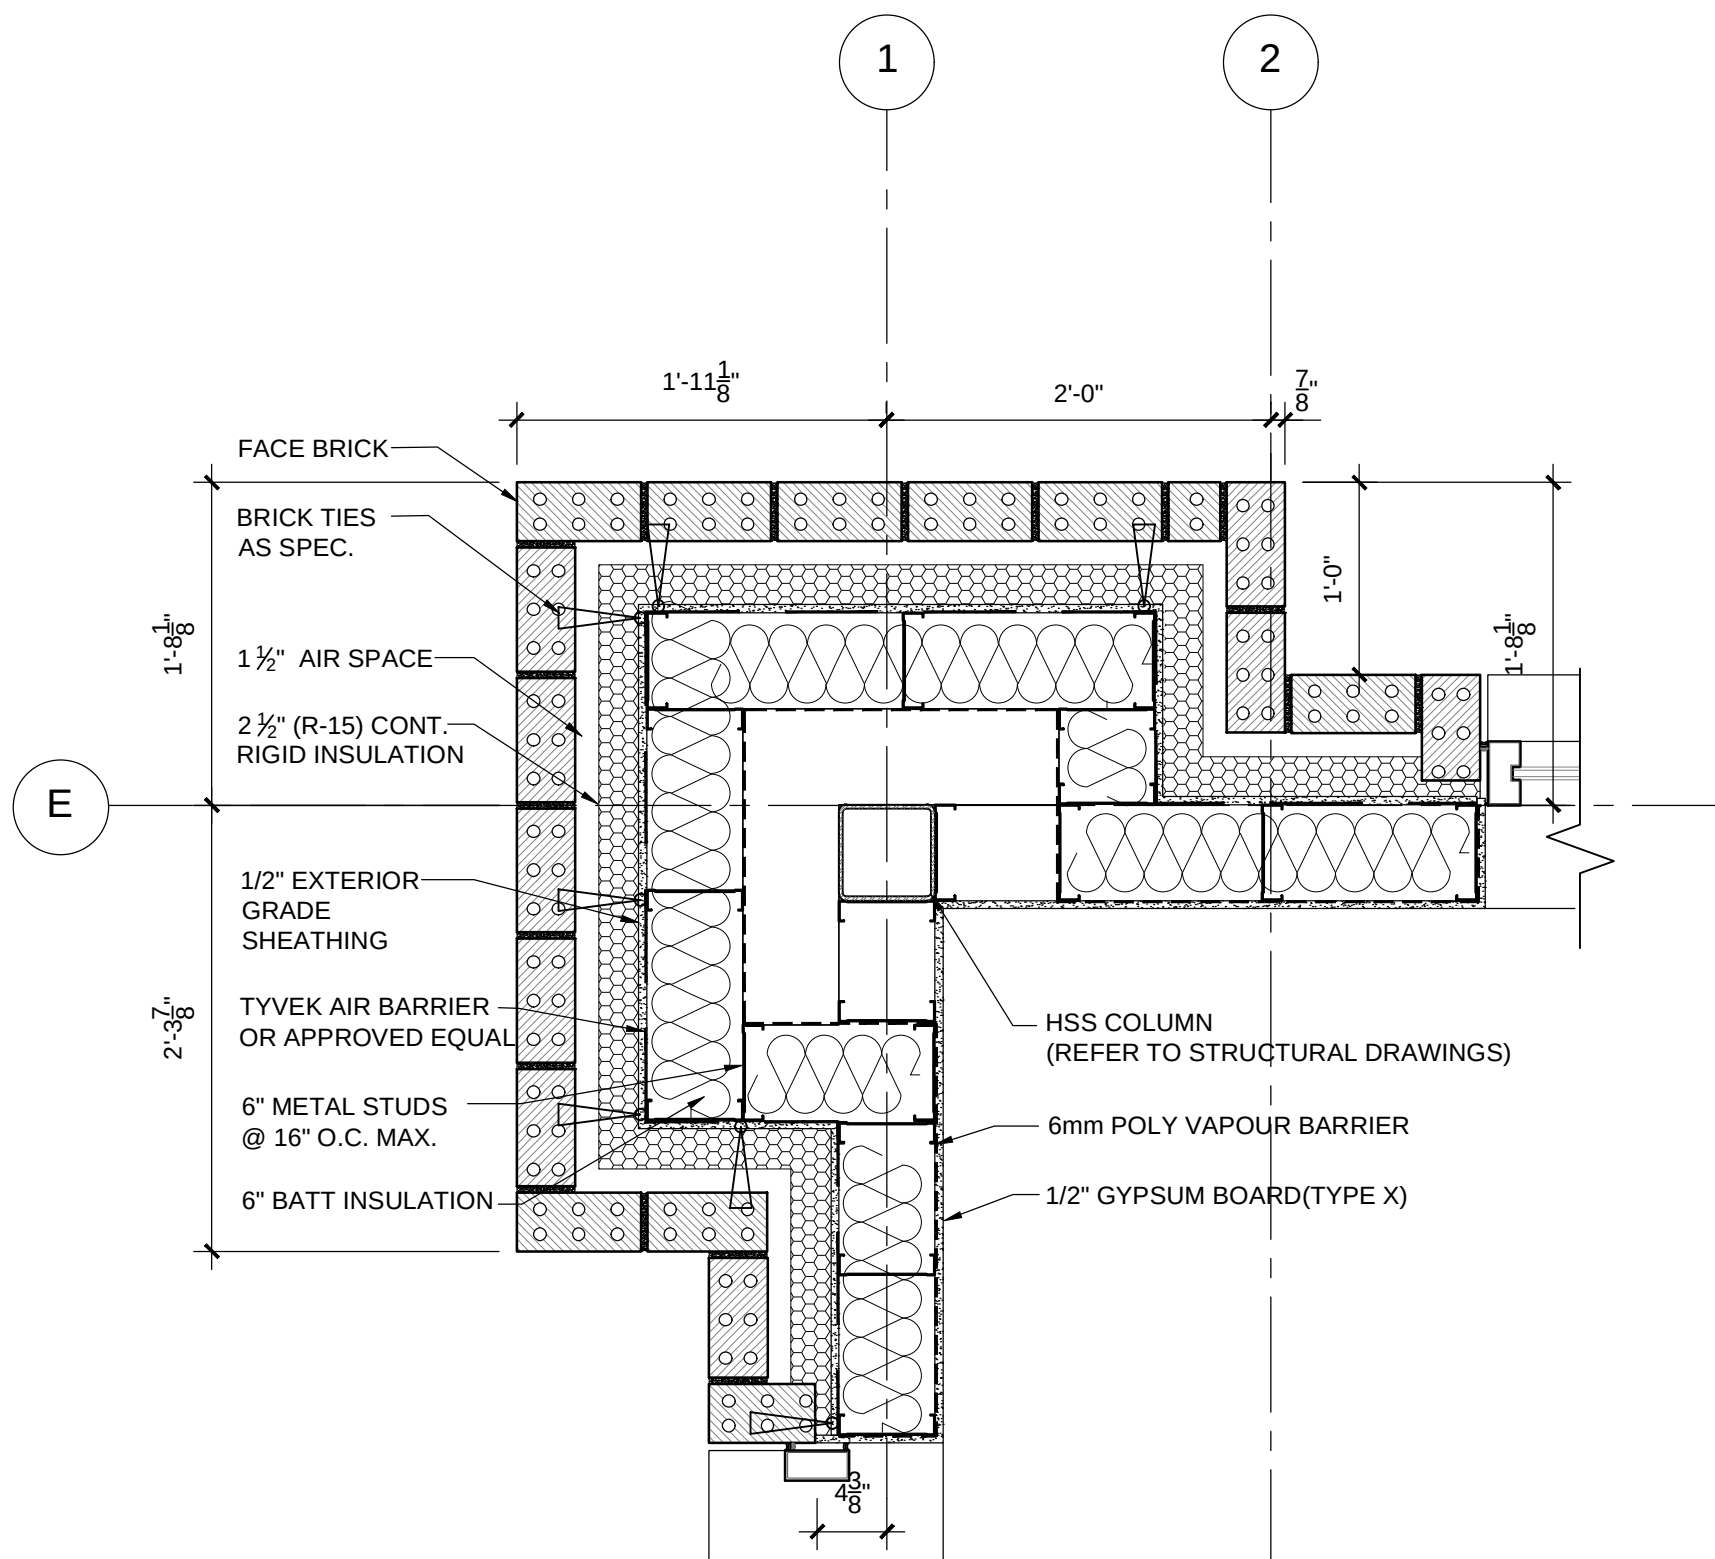


1
A-2.0
PLAN NORTH
ENLARGED PLAN
SCALE: 1"=1'-0"

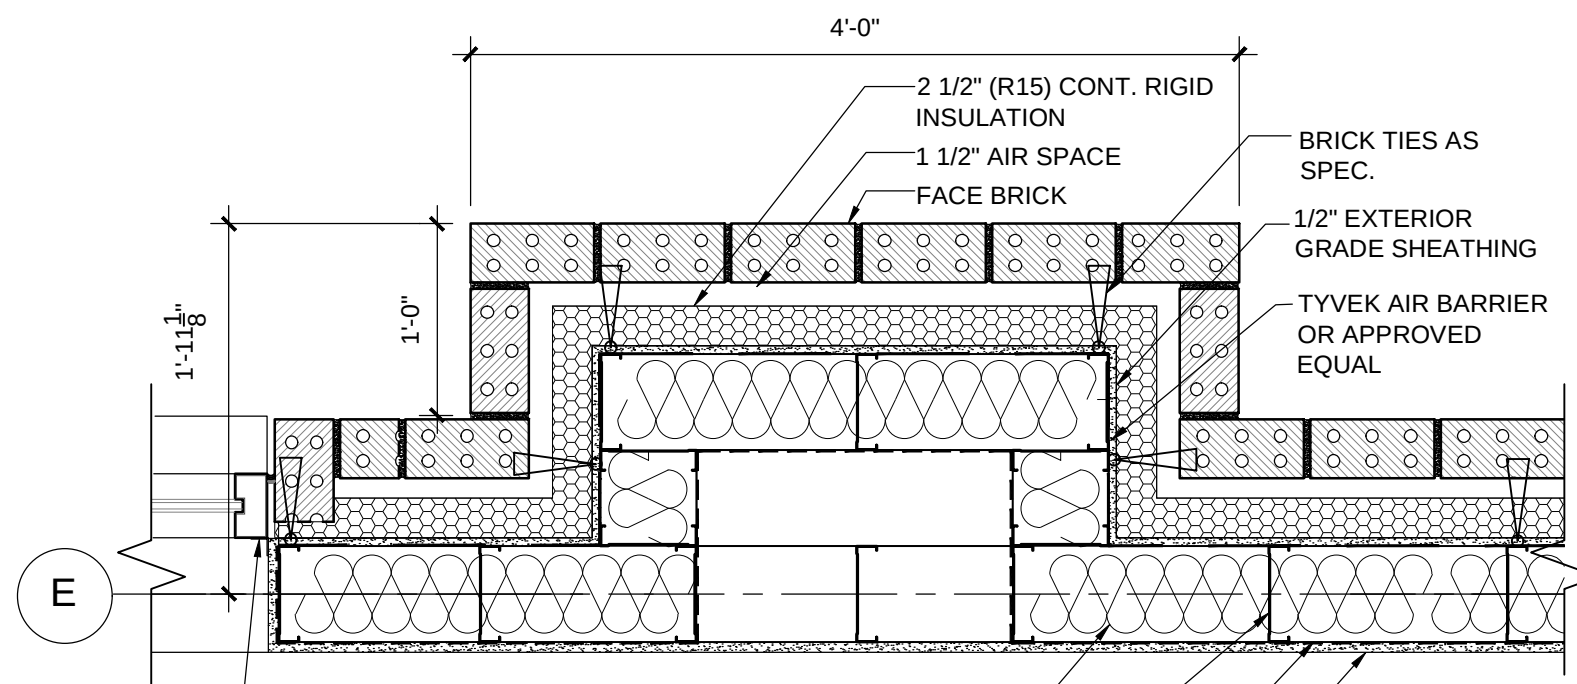


2
A-2.0
PLAN NORTH
ENLARGED PLAN
SCALE: 1"=1'-0"

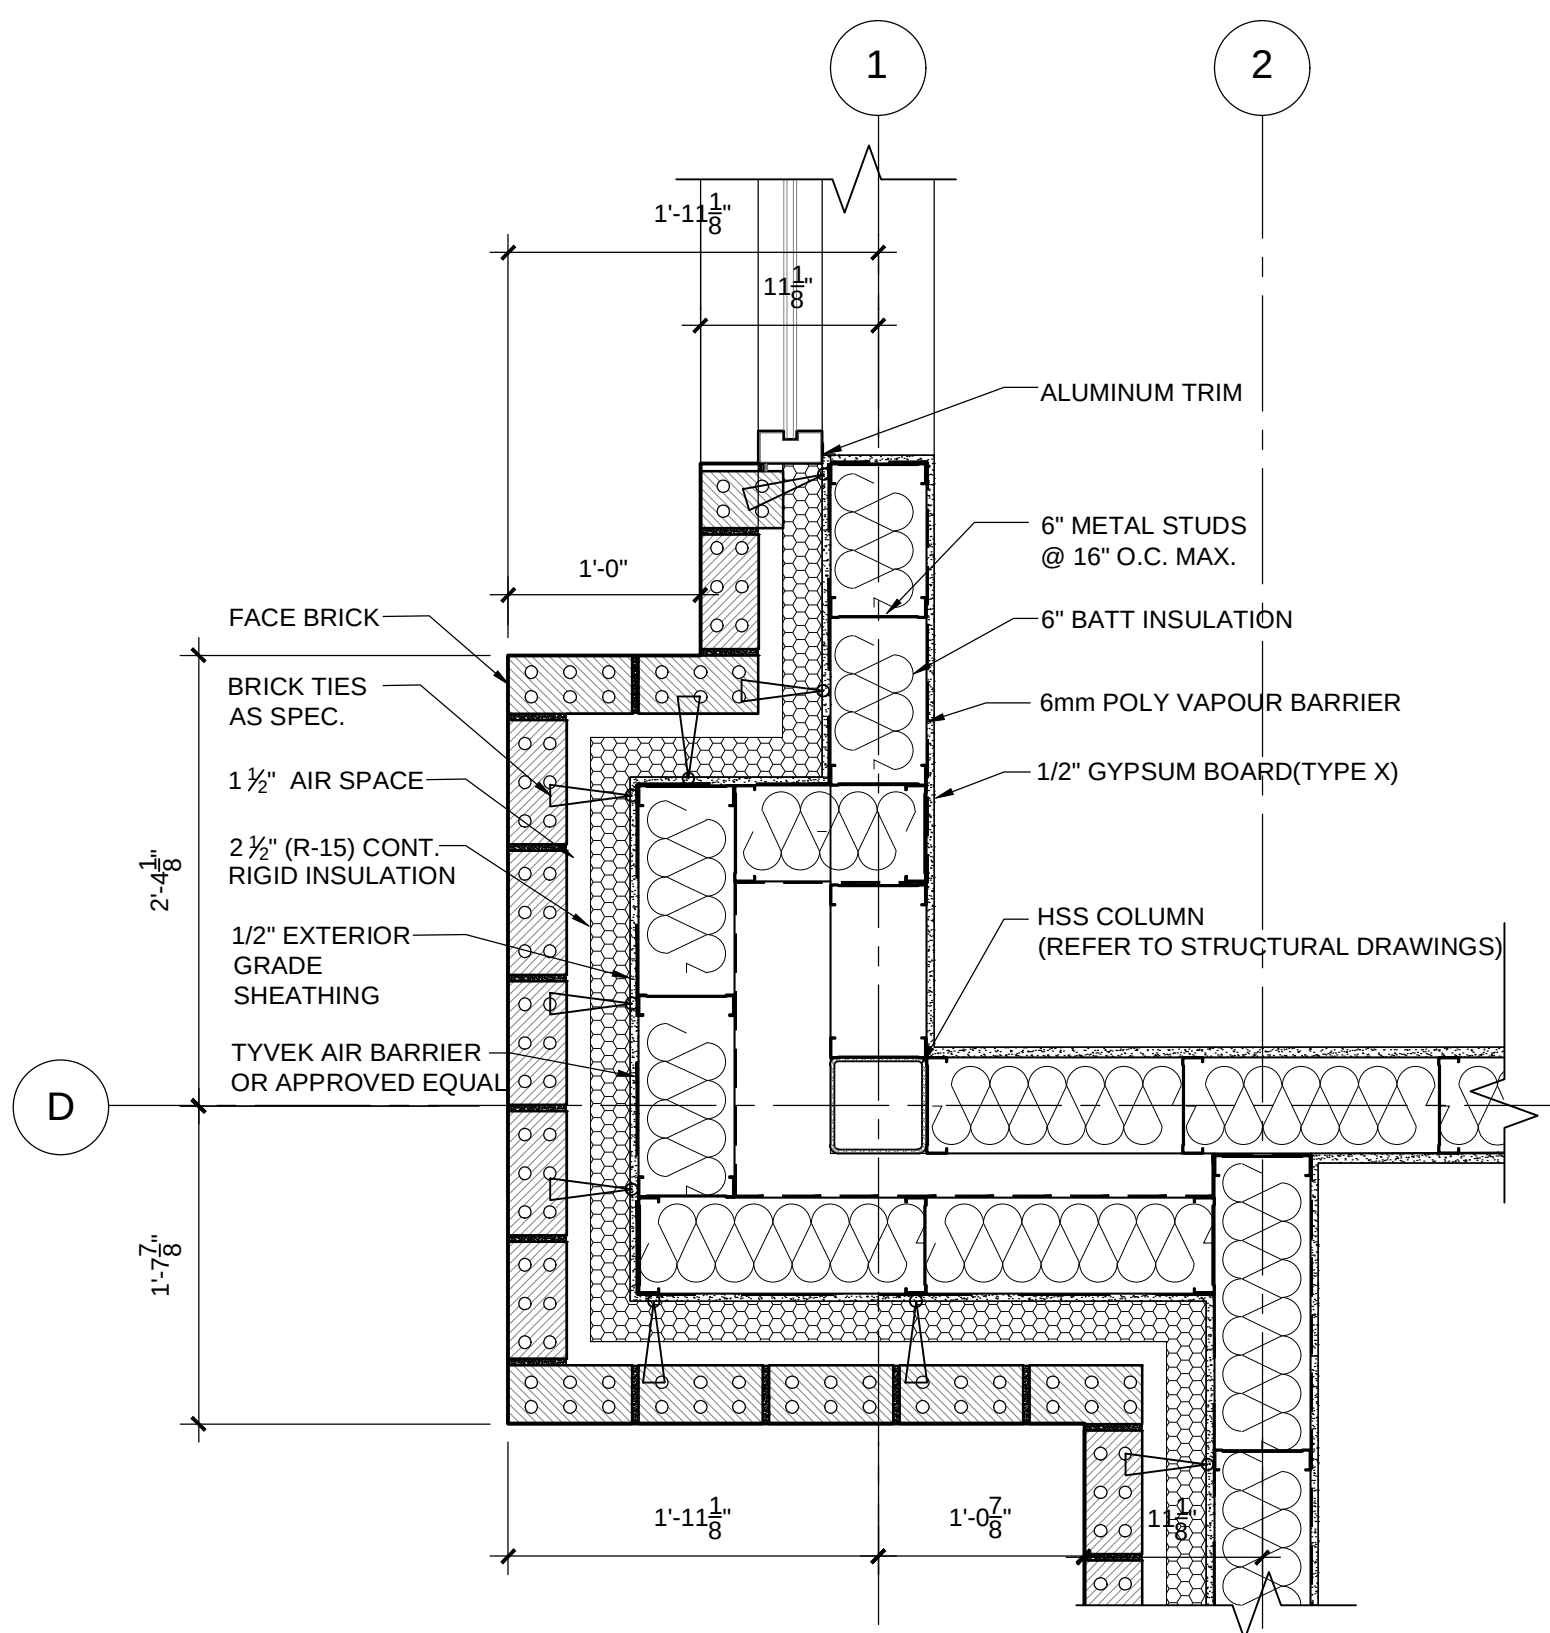

3
A-2.0
PLAN NORTH
ENLARGED PLAN
SCALE: 1"=1'-0"

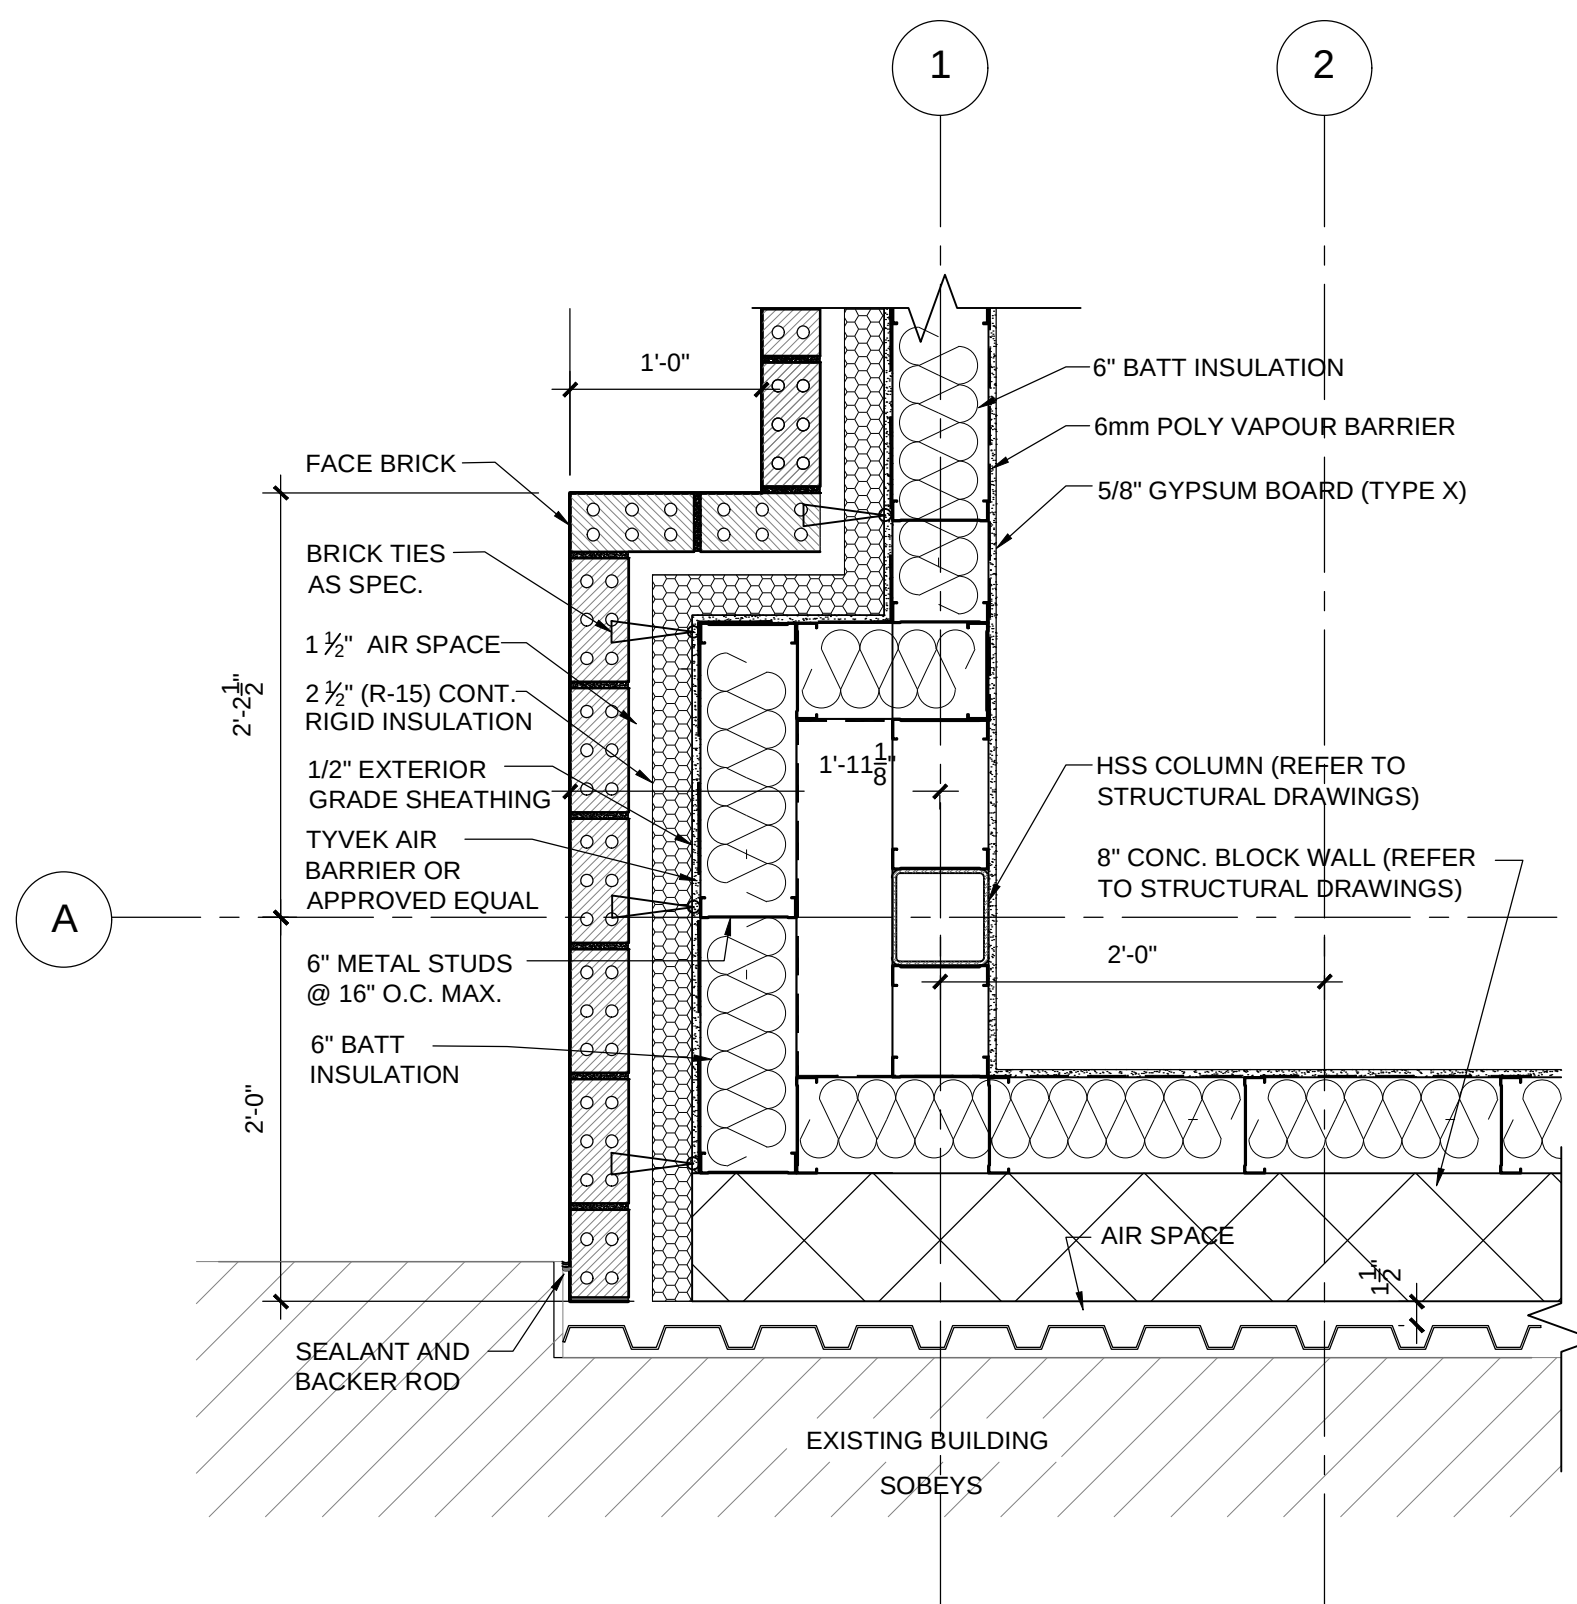

4
A-2.0
PLAN NORTH
ENLARGED PLAN
SCALE: 1"=1'-0"

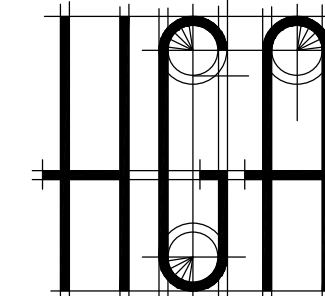

**HANNA, GHOBRIAL
AND ASSOCIATES LTD.**
engineering
architecture

3100 Temple Drive
Windsor, ON N8W 5J6
(519) 945-7373 FAX-5636



This drawing shall not be used for construction unless it is countersigned by the CONSULTANT.

NOTE:
ENGINEERED SHOP DRAWINGS: FOR ANY "MANUFACTURED COMPONENT" FORMING PART OF THE BUILDING (i.e. ENGINEERED ROOF TRUSSES, ENGINEERED FLOOR JOISTS, TIMERS, ETC.) MUST BE SUBMITTED TO HANNA GHOBRIAL & ASSOCIATES, LTD. FOR REVIEW AND APPROVAL. IF ENGINEERED SHOP DRAWINGS ARE NOT SUBMITTED AND APPROVED, HANNA GHOBRIAL & ASSOCIATES, LTD. WILL NOT BE RESPONSIBLE FOR ANY ASSOCIATED COSTS OR DAMAGES.

ALL DRAWINGS, SPECIFICATIONS AND OTHER RELATED DOCUMENTS ARE THE COPYRIGHT PROPERTY OF THE CONSULTANT AND SHALL BE RETURNED UPON REQUEST. REPRODUCTION OF DRAWINGS AND RELATED DOCUMENTS, IN WHOLE OR IN PART, IS FORBIDDEN WITHOUT THE WRITTEN PERMISSION OF THE CONSULTANT.

THE CONTRACTOR SHALL CHECK AND VERIFY ALL PERTINENT DIMENSIONS AND REPORT ANY DISCREPANCIES TO THE CONSULTANT BEFORE PROCEEDING WITH THE WORK.

THIS DRAWING SHALL NOT BE USED FOR CONSTRUCTION UNLESS IT IS COUNTERSIGNED BY THE CONSULTANT.

THIS DRAWING IS NOT TO BE SCALED.

USE FIGURED DIMENSIONS ONLY.

12		
11		
10		
9		
8		
7		
6		
5		
4		
3		
2		
1	22/03/31	PERMIT

No. Date: Issued For:

Date: OCTOBER 2021

Drawn By: R.Z.

Checked By: R.J.

Project Title:

83 SANDWICH STREET
BUILDING ADDITION

AMHERSTBURG, ONTARIO

Project No.:

21-0427

Sheet Title:

PLAN ENLARGED
DETAILS

Sheet No.:

A-2.1