

Item	Site Data Matrix	OBC Reference
1	Project Description: NEW BUILDING ADDED TO AN EXISTING SHOPPING CENTER 1 STOREY, LCBO.	☒ New ☐ Addition ☐ Alteration ☐ Change of Use
2	Zoning Designation:	CH-8), SHOPPING CENTER-RETAIL STORE
3	Existing Land Use:	PARKING LOT
4	Major Occupancy(s):	MERCANTILE OCCUPANCY
5	Building Classification: Group (E) Division () 3.2.2 (62)	
6	Site Area Existing: 50,767.3 m ² Proposed: --- Total: 50,767.3 m ²	Building Area Existing: 17,138.6 m ² Proposed: 6,108.5 m ² Total: 23,247.1 m ²
7	Lot Coverage Maximum: 25.353 k m ² 50% Provided: 272,804.4 m ² 34.9%	Minimum Lot Width Required: --- Provided: 173.7m (569'-8")
8	Minimum Front Yard Depth Required: 0.0m (0'-0") Provided: 0.6m (1'-11.5")	Minimum Rear Yard Depth Required: 0.0m (0'-0") Provided: 147.9m (485'-2")
9	Parking Use Classification: Existing: 864 Proposed: 762 Required: 23 (1 CAR/ 25 m ²) Total: 762	Bicycle Spaces Existing: N/A Proposed: N/A Required: N/A Total: N/A
10	Landscaped Area Existing: 33,566.67 m ² Proposed: 32,566.67 m ² Total: 32,566.67 m ²	Screening Fence Length Existing: N/A Proposed: 30.9' Total: 30.9'

Should archaeological deposits be found during construction activities, all work in the area must stop immediately and the City's Manager of Cultural Affairs and the Ontario Ministry of Tourism, Culture and Sport must be notified, and clearance given by the Ministry.


In the event that human remains are encountered during construction, all work in that area must be stopped immediately and the site secured. The local police or coroner must be contacted to determine whether or not the skeletal remains are human, and whether the remains constitute a part of a crime scene. The Ontario Ministry of Tourism, Culture and Sport and the Registrar of the Cemeteries Regulation Unit of the Ministry of Consumer Services must then be notified, and clearance be given by the Ministry of Tourism, Culture and Sport.

A building shall not be located beneath existing above ground electrical conductors. Where a building is to be constructed in proximity to above ground electrical conductors, horizontal clearances between buildings and conductors shall comply with Subsection 3.1.19. of the Ontario Building Code.

SITE STATISTICS					
PARKING	EXISTING PARKING	AREA (SQ.M.)	ZONING FORMULA	REQUIRED	PROPOSED
BRICK STUCCO BUILDING					
BRICK & STUCCO BUILDING					
BRICK & FRAME BUILDING					
TOTAL		6,381.63	1 CAR PER/ 30 m ²	212.7	234
WALMART		10,757.00	1 CAR PER/ 30 m ²	358.6	± 496
LCBO		570.00	1 CAR PER/ 25 m ²	22.8	29
TOTAL	#869 CARS			596 CARS	765 CARS

NOTE:

ALL SURVEY INFO. BY
BRIAN COAD OF VERHAEGEN STUBBERFIELD
WORK ORDER: 4-24532-X01
PLAN FILE No: J- 402

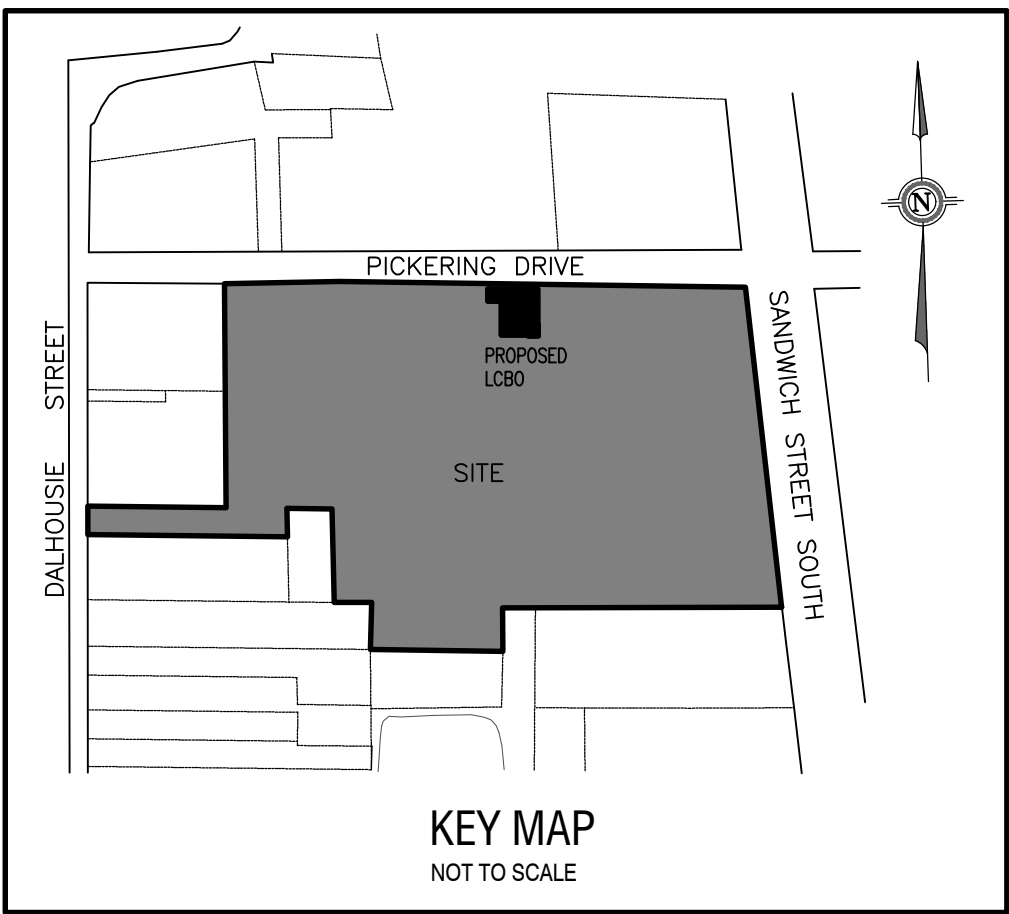

HANNA, GHOBRIAL AND ASSOCIATES LTD.
engineering
architecture
3100 Temple Drive, Suite 100
Windsor, ON N9W 5J6
(519) 945-7373 FAX: -5636

This drawing shall not be used for construction unless it is countersigned by the CONSULTANT

NOTE:
ENGINEERED SHOP DRAWINGS, FOR ANY MANUFACTURED COMPONENT FORMING PART OF THE BUILDING (i.e. ENGINEERED ROOF TRUSSES, ENGINEERED FLOOR JOISTS, TIMERS, ETC.) MUST BE SUBMITTED TO HANNA GHOBRIAL & ASSOCIATES, LTD. FOR REVIEW AND APPROVAL. IF ENGINEERED SHOP DRAWINGS ARE NOT SUBMITTED AND APPROVED, HANNA GHOBRIAL & ASSOCIATES, LTD. WILL NOT BE RESPONSIBLE FOR ANY ASSOCIATED COSTS OR DAMAGES.

ALL DRAWINGS, SPECIFICATIONS AND OTHER RELATED DOCUMENTS ARE THE COPYRIGHT PROPERTY OF THE CONSULTANT AND SHALL BE RETURNED UPON REQUEST.
REPRODUCTION OF DRAWINGS AND RELATED DOCUMENTS, IN WHOLE OR IN PART, IS FORBIDDEN WITHOUT THE WRITTEN PERMISSION OF THE CONSULTANT.
THE CONTRACTOR SHALL CHECK AND VERIFY ALL PERTINENT DIMENSIONS AND REPORT ANY DISCREPANCIES TO THE CONSULTANT BEFORE PROCEEDING WITH THE WORK.
THIS DRAWING SHALL NOT BE USED FOR CONSTRUCTION UNLESS IT IS COUNTERSIGNED BY THE CONSULTANT.
THIS DRAWING IS NOT TO BE SCALED.
USE FIGURED DIMENSIONS ONLY.

12	
11	
10	
9	
8	2023/09/26 SPA - REV. TRUCK ROUTE
7	2023/09/12 REVIEW BY WALMART
6	2023/09/06 SITE PLAN APPLICATION
5	2023/08/15 PHOTOMETRIC ANALYSIS
4	2023/08/03 CLIENT REVIEW
3	2023/07/31 PRE-SUBMITTAL APPLIC.
2	2023/07/26 CLIENT REVIEW
1	2023/06/21 SITE PLAN APPLICATION

No. Date: Issued For:

Date: JUNE 2023

Drawn By: H.R.

Checked By: E.B.K.

Client:
Joseph B. Mikhail
Mikhail Holdings Ltd.
100 Ouellette Ave., Suite 700
Windsor, ON, N9A 6T3

Project Title:

LCBO
NEW
LCBO STORE

Address: 400 SANDWICH STREET
AMHERSTBURG, ONTARIO N9W 3L4


Project No.:
22-0445

Sheet Title:

OVERALL SITE PLAN


Sheet No.:

SP-1

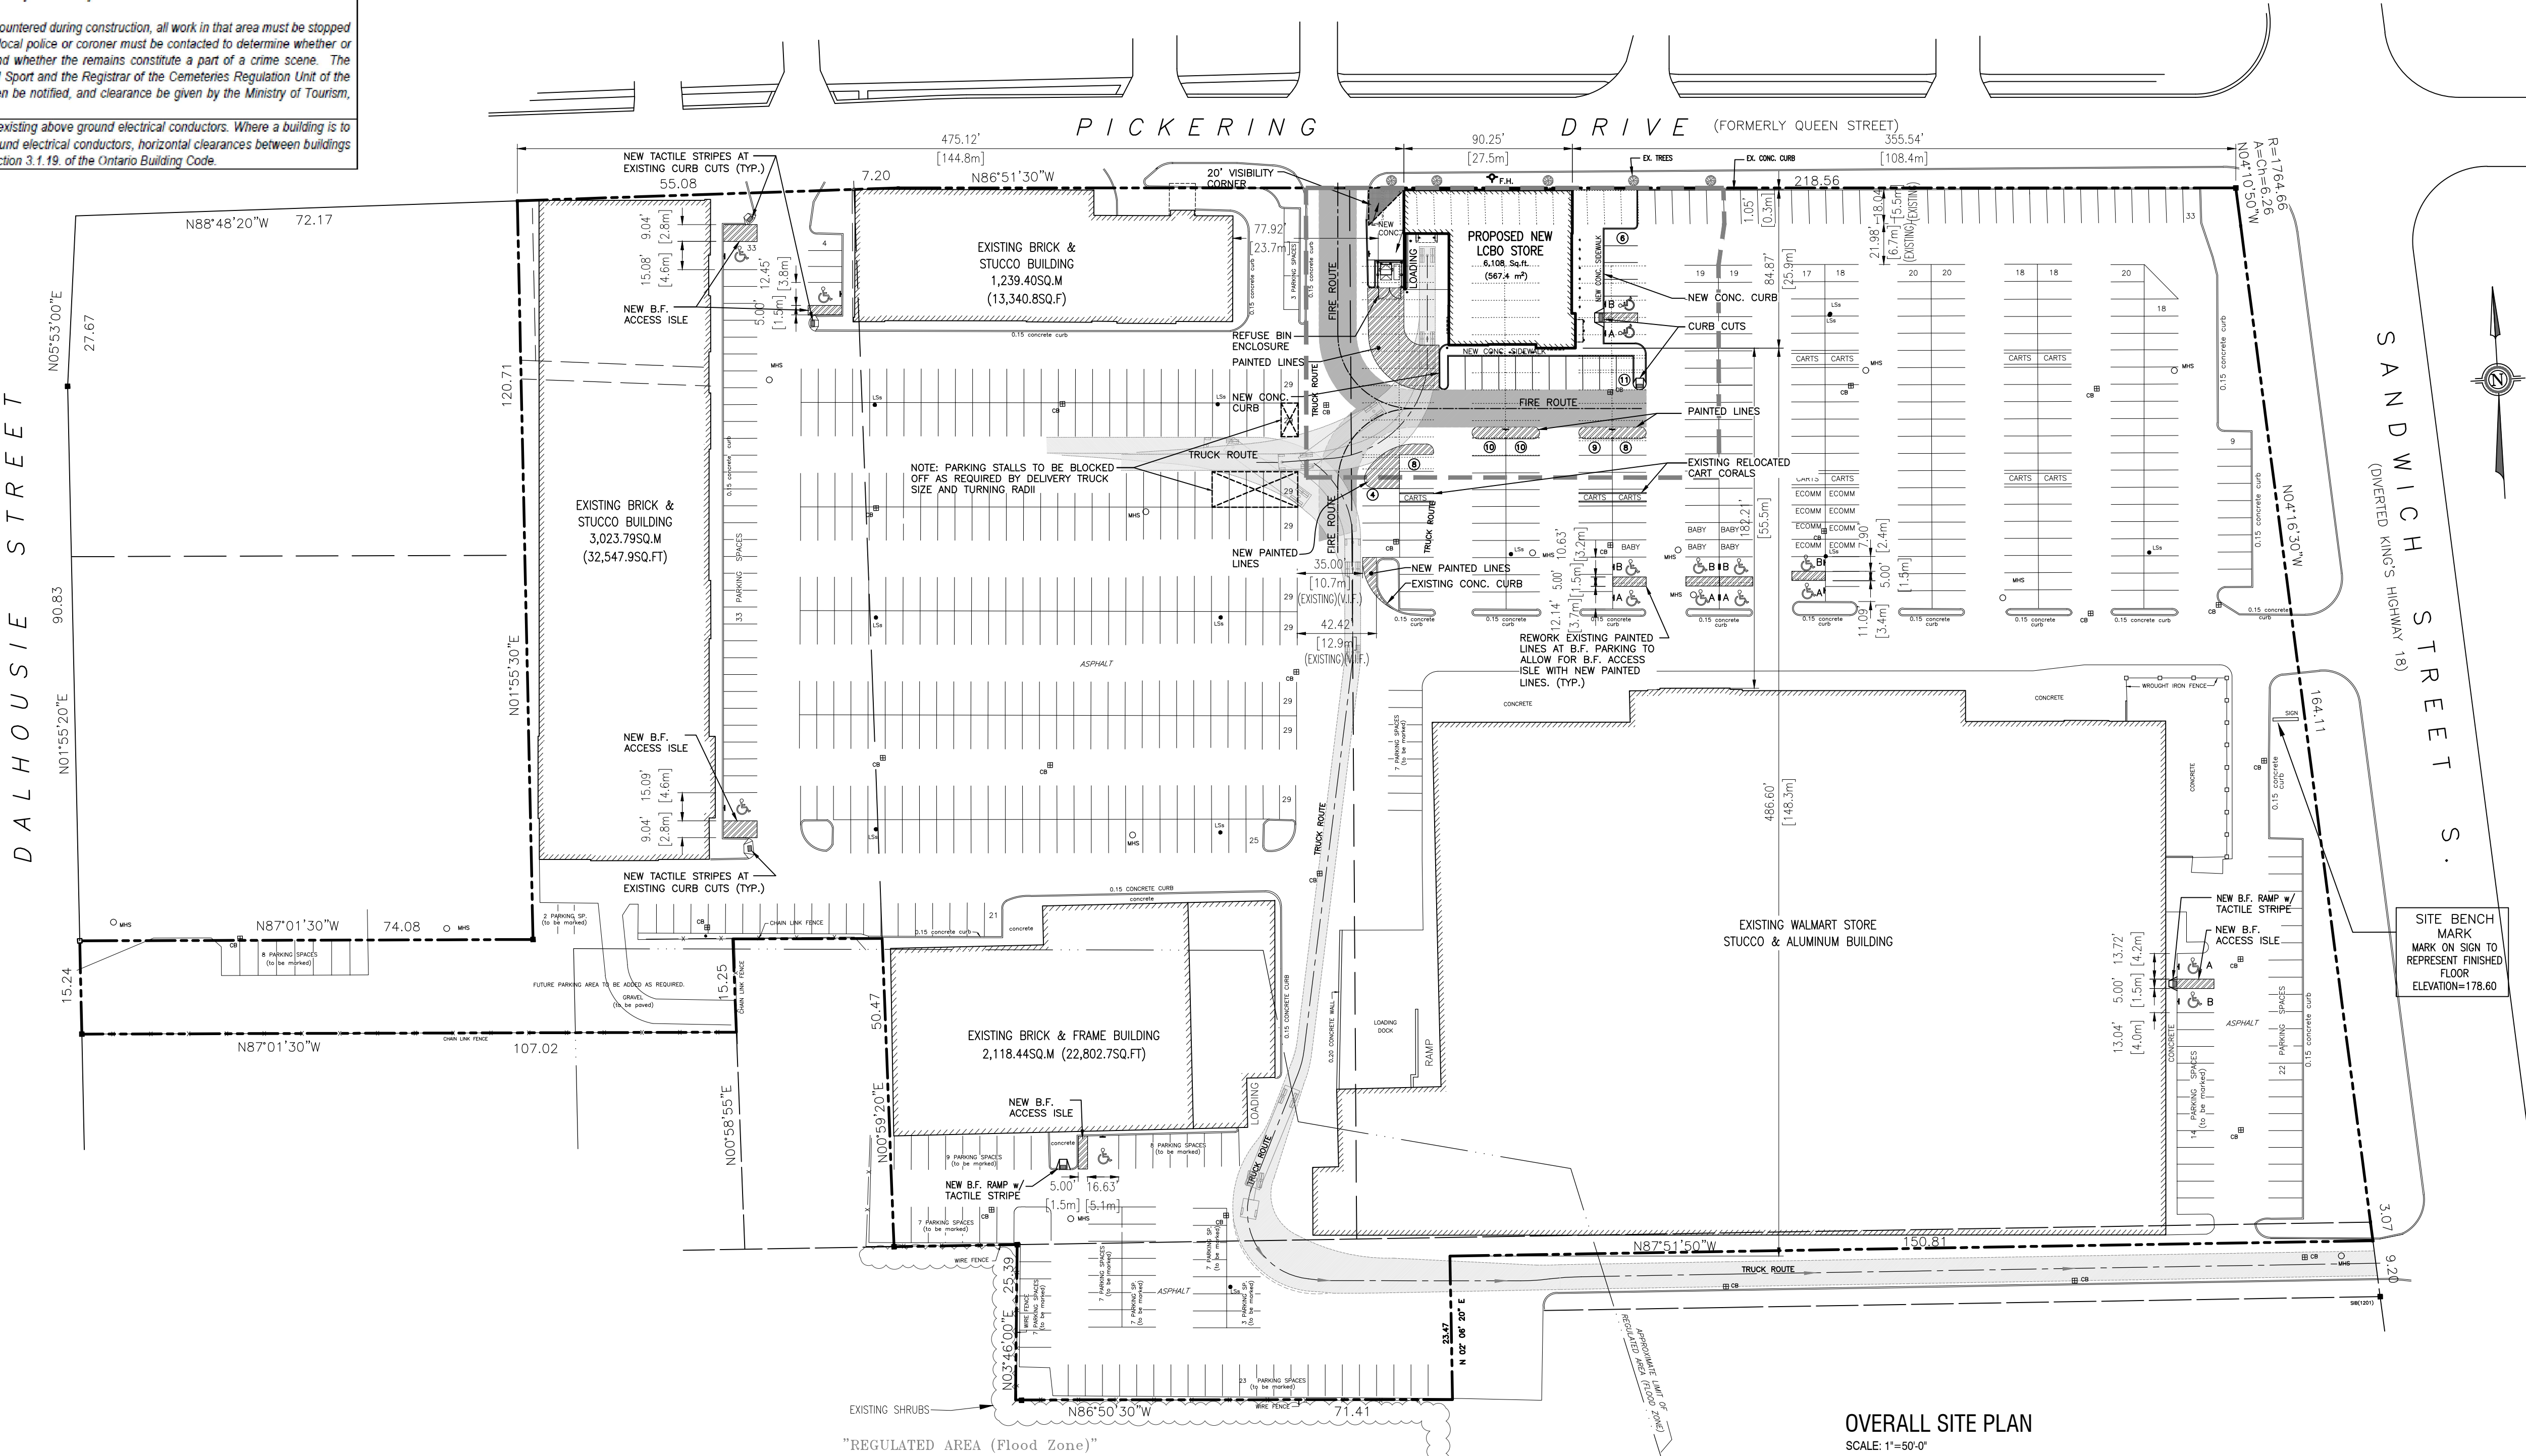


OVERALL SITE PLAN
SCALE: 1"=50'-0"

FILE LOCATION: Y:\22-0445 - New LCBO Amherstburg - 400 Sandwich Street - MH\Arch\Construction Documents\SP-1 - Site Plans & Details - Sp-0203.dwg

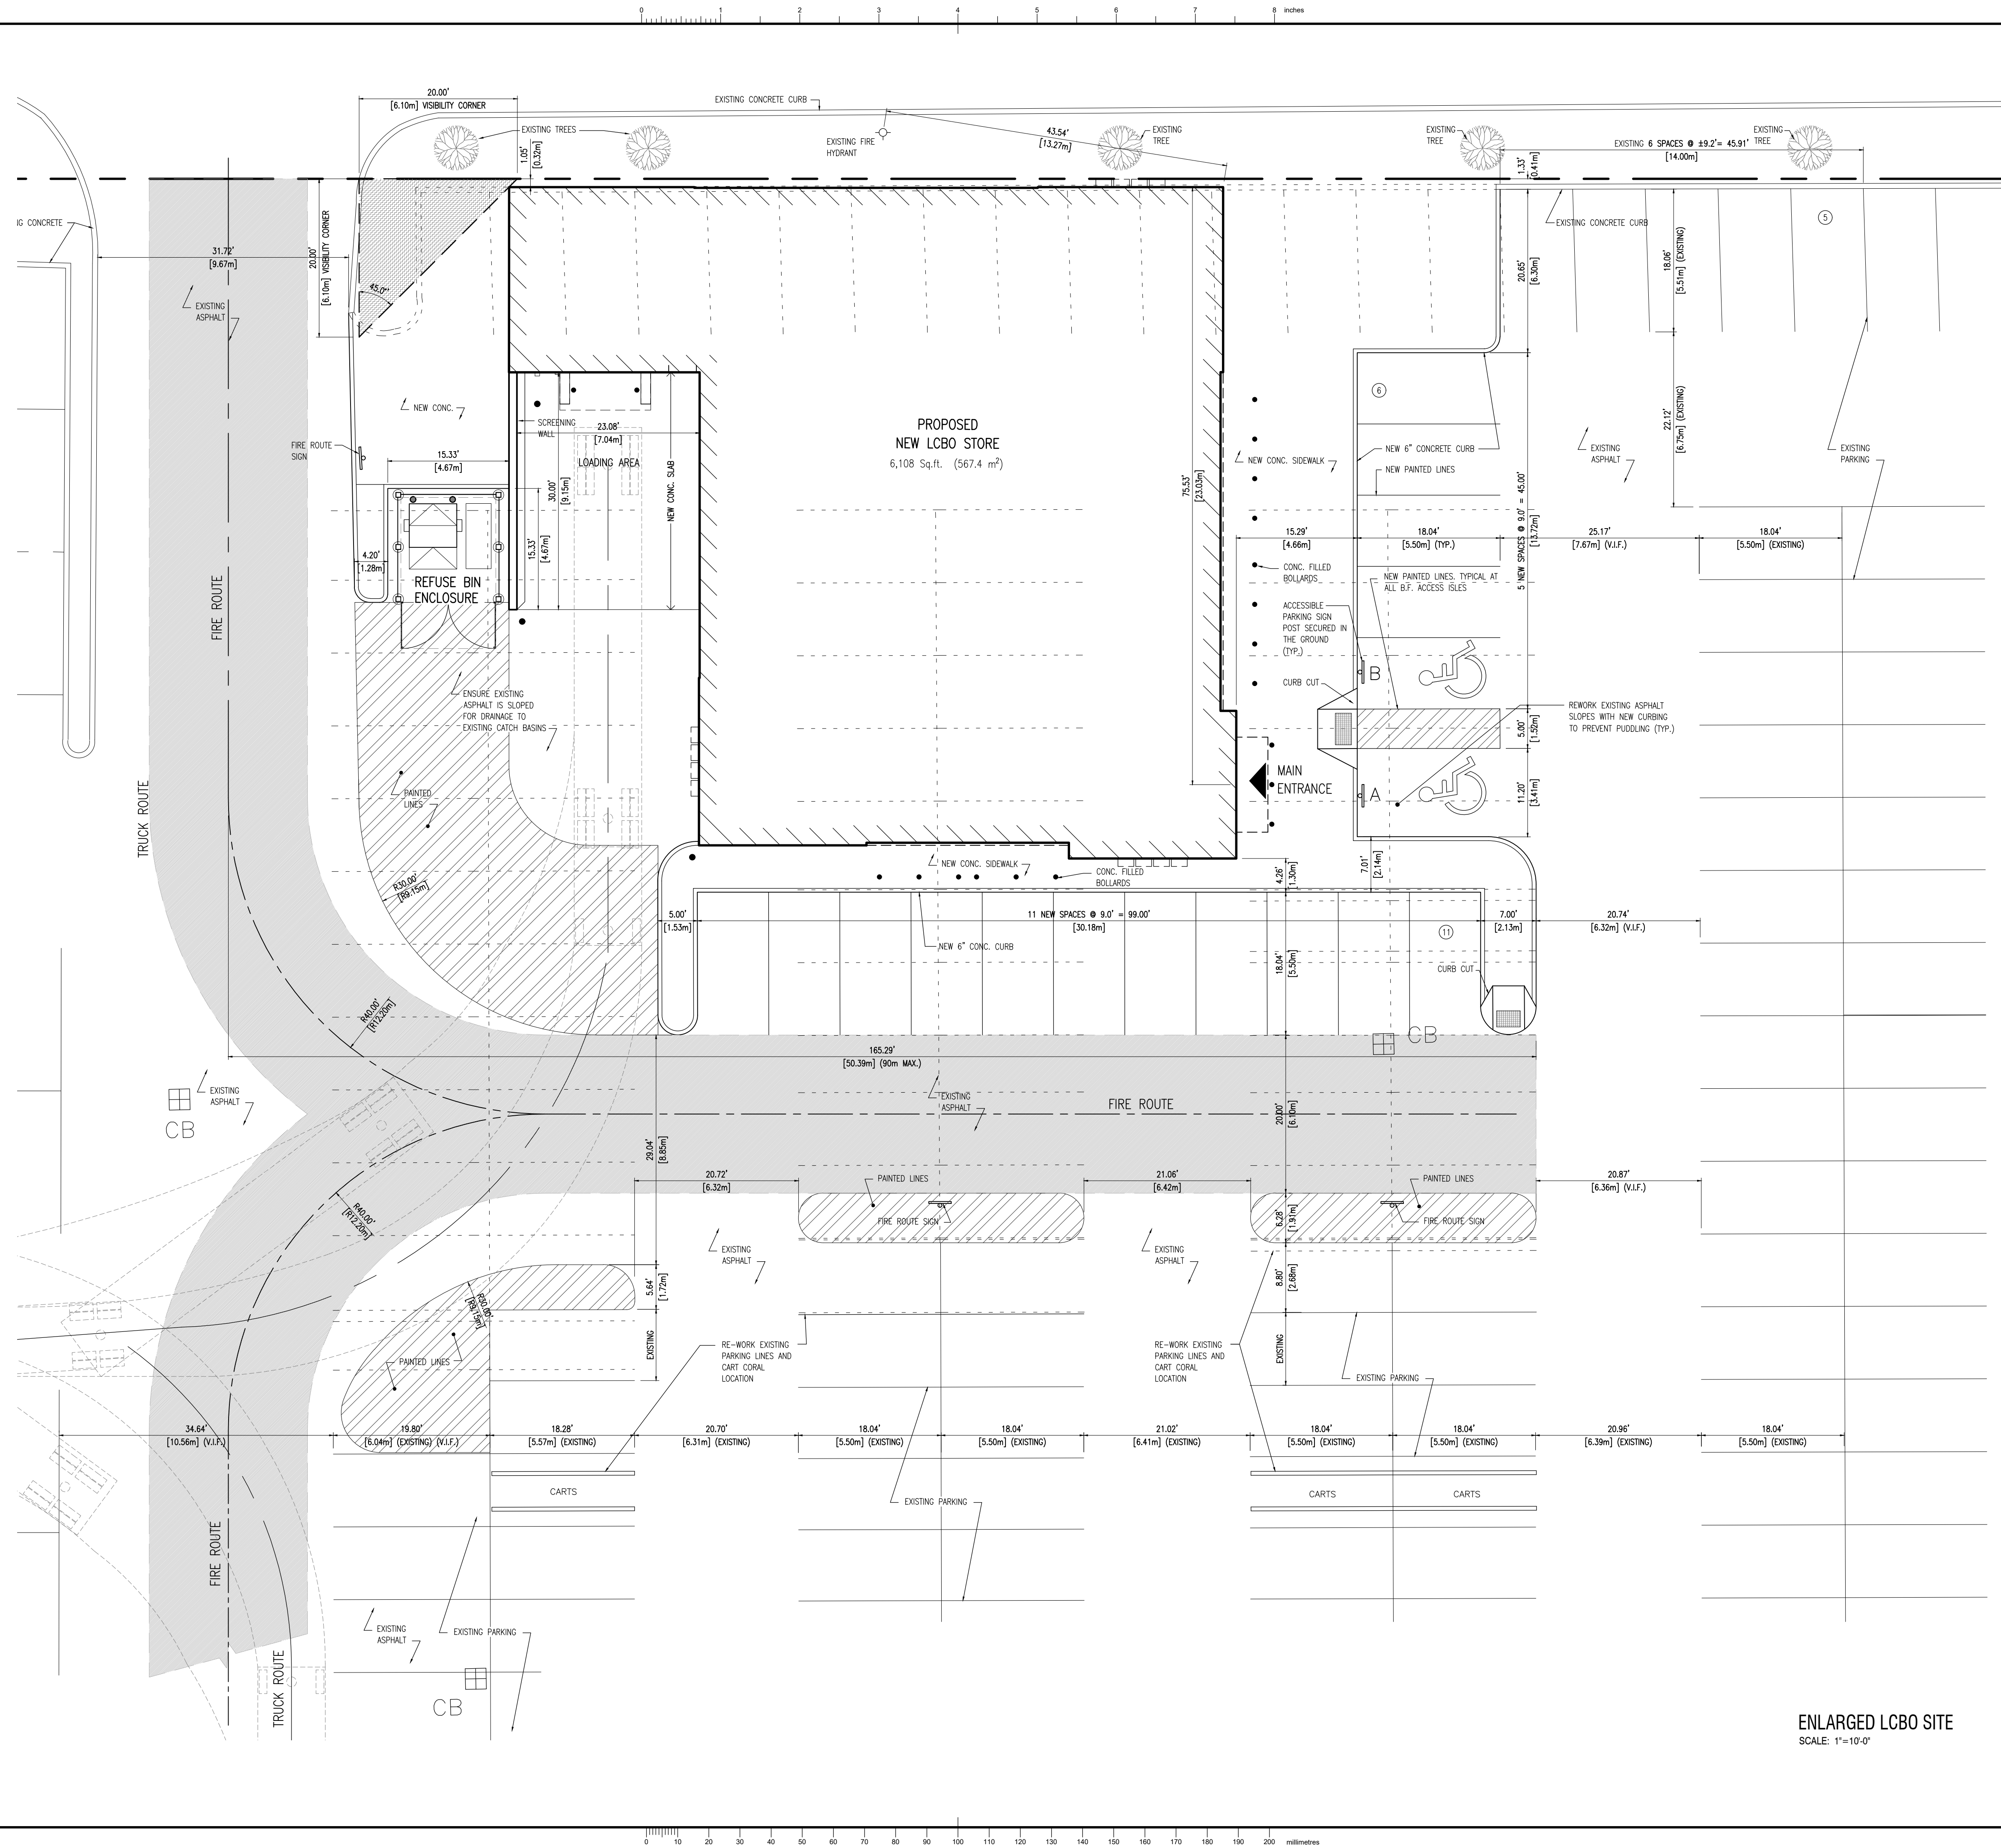

ENLARGED LCBO SITE
SCALE: 1"=10'-0"

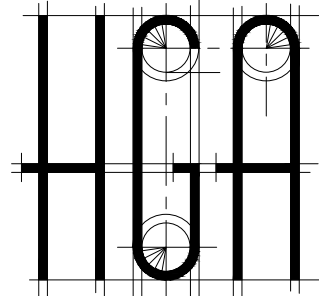

HANNA, GHOBRIAL
AND ASSOCIATES LTD.
engineering
architecture

3100 Temple Drive, Suite 100
Windsor, ON N8W 5J6
(519) 945-7373 FAX: -5636

This drawing shall not be used for construction unless it is countersigned by the CONSULTANT

NOTE:
ENGINEERED SHOP DRAWINGS, FOR ANY "MANUFACTURED COMPONENT" FORMING PART OF THE BUILDING (i.e. ENGINEERED ROOF TRUSSES, ENGINEERED FLOOR JOISTS, TIMBERS, ETC.) MUST BE SUBMITTED TO HANNA GHOBRIAL & ASSOCIATES LTD. FOR REVIEW AND APPROVAL. IF ENGINEERED SHOP DRAWINGS ARE NOT SUBMITTED AND APPROVED, HANNA GHOBRIAL & ASSOCIATES LTD WILL NOT BE RESPONSIBLE FOR ANY ASSOCIATED COSTS OR DAMAGES.

ALL DRAWINGS, SPECIFICATIONS AND OTHER RELATED DOCUMENTS ARE THE COPYRIGHT PROPERTY OF THE CONSULTANT AND SHALL BE RETURNED UPON REQUEST. REPRODUCTION OF DRAWINGS AND RELATED DOCUMENTS, IN WHOLE OR IN PART, IS FORBIDDEN WITHOUT THE WRITTEN PERMISSION OF THE CONSULTANT.

THE CONTRACTOR SHALL CHECK AND VERIFY ALL PERTINENT DIMENSIONS AND REPORT ANY DISCREPANCIES TO THE CONSULTANT BEFORE PROCEEDING WITH THE WORK.

THIS DRAWING IS NOT TO BE USED FOR CONSTRUCTION UNLESS IT IS COUNTERSIGNED BY THE CONSULTANT.

THIS DRAWING IS NOT TO BE SCALED
USE FIGURED DIMENSIONS ONLY.

12	
11	
10	
9	
8	2023/09/26 SPA- REV. TRUCK ROUTE
7	2023/09/12 REVIEW BY WALMART
6	2023/09/06 SITE PLAN APPLICATION
5	2023/08/15 PHOTOMETRIC ANALYSIS
4	2023/08/03 CLIENT REVIEW
3	2023/07/31 PRE-SUBMITTAL APPLIC.
2	2023/07/26 CLIENT REVIEW
1	2023/06/21 SITE PLAN APPLICATION
YY/MM/DD	
No.	Date: Issued For:

Date: JUNE 2023

Drawn By: N.F./H.R.

Checked By: E.B.K.

Client:
Joseph B. Mikhail
Mikhail Holdings Ltd.
100 Ouellette Ave., Suite 700
Windsor, ON, N9A 6T3

Project Title:

LCBO
NEW
LCBO STORE

Address: 400 SANDWICH STREET
AMHERSTBURG, ONTARIO N9W 3L4

Project No.:


22-0445

Sheet Title:

ENLARGED LCBO SITE

Sheet No.:

SP-2

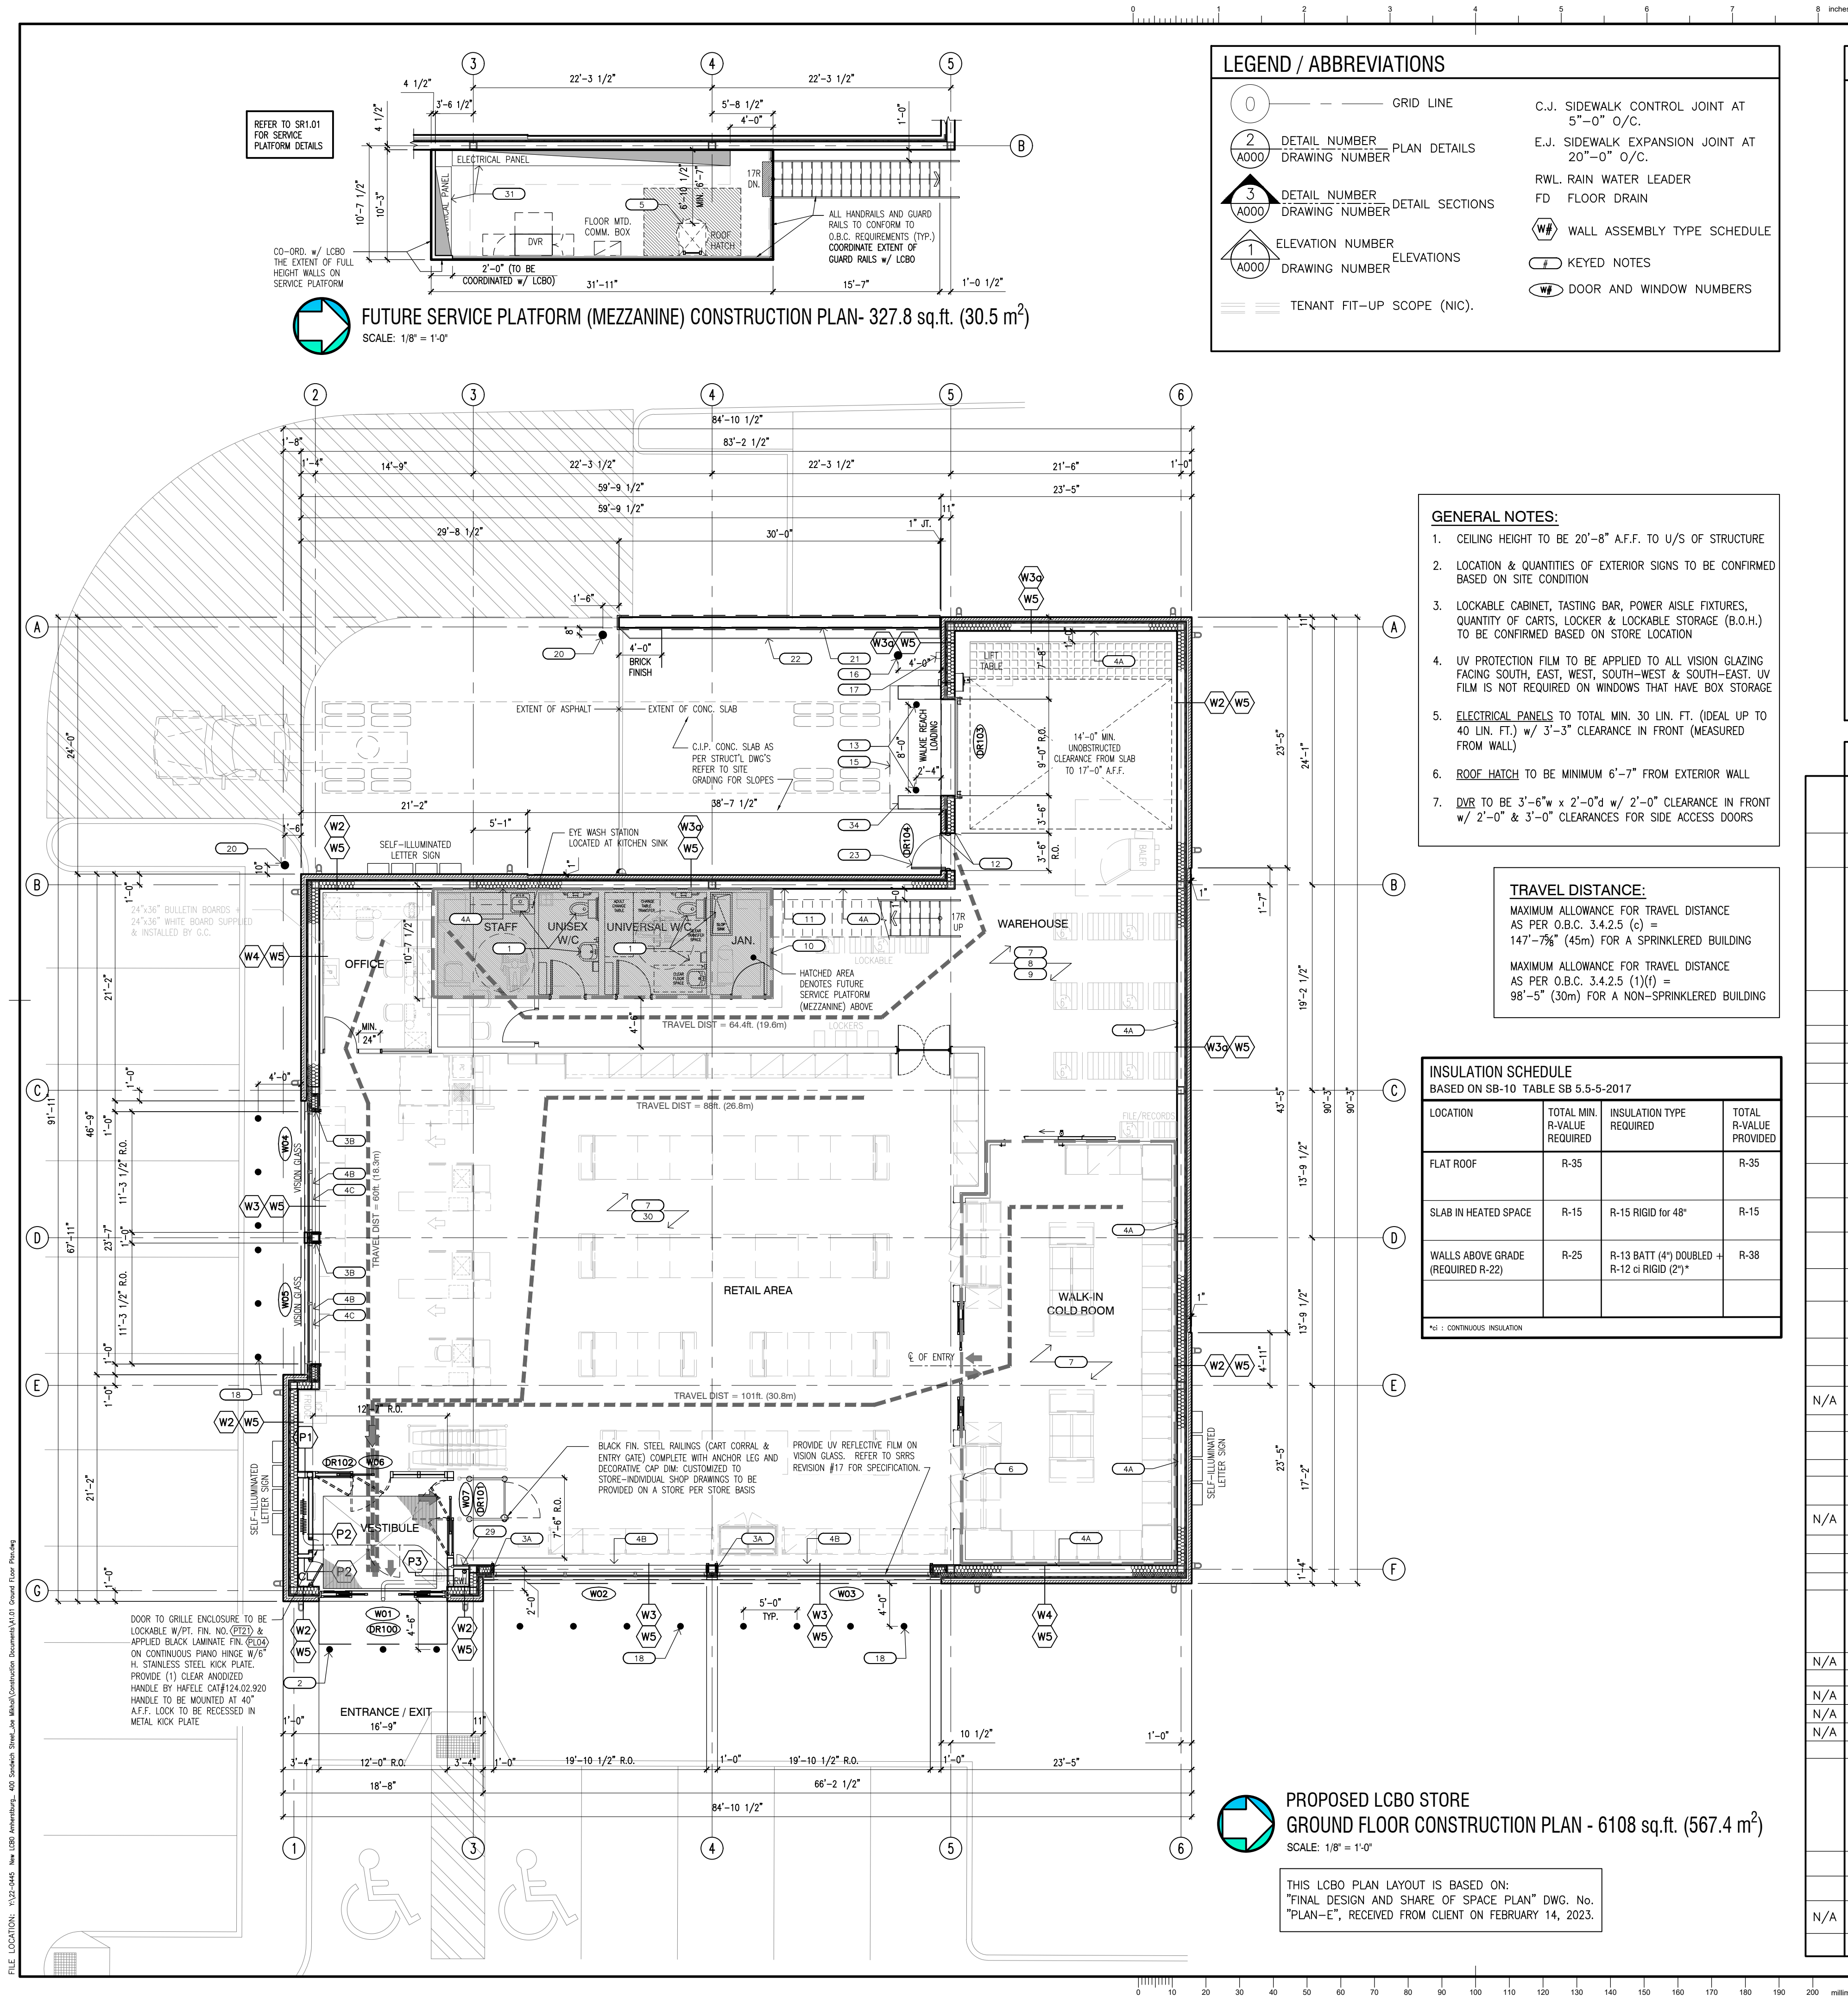


GENERAL CONSTRUCTION NOTES

- REFER TO LBRR SPECIFICATION SECTIONS FOR INFORMATION ON SPECIFIC PRODUCTS.
- DRYWALL SURFACE ON EXTERIOR WALLS TO HAVE VERTICAL CONTROL JOINTS AT INTERVAL OF 9M (29'-6") MAX. AND CONT. HORIZONTAL CONTROL JOINTS 6" BELOW OWSJ.
- OVERALL BUILDING HEIGHTS ON LCBO-PROVIDED ELEVATION SPECIFIC TO THIS SITE WILL SUPERSEDE THE DIMENSIONS NOTED ON THIS PAGE, AND ITS ASSOCIATED WALL SECTIONS AND CROSS SECTIONS.
- A BASE-BUILDING SERVICES COORDINATION DRAWING WILL BE PROVIDED FOR LOCATIONS OF ALL IN FLOOR SERVICES FOR COORDINATION PRIOR TO SLAB-ON-GRADE POUR AND/OR CORING OF SUSPENDED SLABS. (FLOOR DRAINS AND WALKER DUCT ETC.) DRAWINGS WILL ALSO INDICATE THE LOCATION OF DUPLEX RECEPTACLES WHICH ARE TO BE INSTALLED BY THE BASE BUILDING G.C.
- PROVIDE BURGLAR BARS FOR ROOF OPENINGS LARGER THAN 9"x9".
- LCBO TO PROVIDE LOCATION, MANUFACTURER AND DIMENSIONS FOR FOOT GRILLE BEFORE POURING THE SLAB.
- BOLLARDS AT LOADING DOCK LOCATION, RAMPS, BUILDING CORNERS AND GAS METER TO BE PAINTED SAFETY YELLOW AS PER ANSI Z535 AND IN ACCORDANCE WITH SRRS' SPECIFICATION SECTION 10 90 00.
- DEPTH OF FOUNDATIONS, FOOTINGS AND PIERS TO BE CONFIRMED AND APPROVED BY BASE BUILDING STRUCTURAL ENGINEER.
- PROVIDE BARRIER-FREE TACTILE WALKING SURFACE INDICATORS AT ALL BARRIER FREE RAMPS AND SIDEWALK CURBS FOR LCBO LOCATIONS TO CONFORM TO OBC 3.4.6.1 AND 3.8.3.18. REFER TO SPECS.
- ENSURE NO MECHANICAL, ELECTRICAL, OR OTHER ITEMS ARE LOCATED ABOVE THE FUTURE INTERIOR FIT UP PARTITIONS TO AVOID INTERFERENCE WITH FUTURE FIT-OUT.
- ALL DRYWALL PERIMETER WALLS, DEMISING WALLS & PARTITIONS TO BE TAPED, SANDED, AND PRIMED READY TO RECEIVE NEW FINISHES FULL HEIGHT. TYP.
- PROVIDE SLIDING CONNECTION TO U/S OF BEAMS, DECK OR JOIST FOR ROOF DEFLECTION AS REQUIRED.
- FIRE SEAL AT ROOF DECK, FLOOR AND ALL WALL PENETRATIONS TO SUIT RATING OF WALL APPLICATION TO COMPLY WITH MANUFACTURER'S SPECIFICATIONS AND TO SATISFACTION OF ALL AUTHORITIES HAVING JURISDICTION FOR ALL RATED WALLS.
- ALL PERIMETER DRYWALL TO FINISH AT U/S OF ROOF STRUCTURE. CUT DRYWALL TO SUIT STRUCTURE, CAULK AND SEAL ROOF DECK, FLOOR AND ALL WALL PENETRATIONS. CLEAN FINISH FOR EXPOSED CONDITIONS IN FUTURE TENANT RETAIL SPACE, TYP.
- SECURITY MESH FOR ALL SPANDREL GLASS LOCATIONS MUST BE INSTALLED, AFFIXED DIRECTLY TO THE OUTSIDE FACE OF THE METAL STUDS AND ADJACENT GLASS BACK PANS, OR AS SPECIFIED ON DRAWINGS. OVERLAP ALL SECURITY MESH PANELS MIN. 3" ALL AROUND TO ENSURE COMPLETE PERIMETER PROTECTION, AND WELD PANELS AT OVERLAP TO SUIT, TYP.
- ALL STEEL STUDS TO BE INSTALLED WITH FOAM GASKET BELOW BOTTOM TRACK TO SEPARATE FROM SLAB-ON-GRADE.
- EXACT LOCATION OF ALL IN FLOOR DRAINS TO BE CONFIRMED BY LCBO PRIOR TO INSTALLATION. CONTACT LCBO PROJECT COORDINATOR FOR INSPECTION PRIOR TO CONCRETE SLAB, TYP.

KEYED NOTES

- PROVIDE DOMESTIC WATER SUPPLY AND SANITARY DRAINAGE ROUGH-IN FOR TENANT WASHROOMS AND LUNCH ROOM AS SHOWN. PARTITIONS AND FIXTURES NIC. LCBO WILL PROVIDE IN-FLOOR SERVICES PLAN FOR DIMENSIONED LAYOUT. ALL LOCATIONS TO BE VERIFIED WITH LCBO PRIOR TO SLAB POUR. CONFIRM & COORDINATE REQUIREMENTS WITH MECHANICAL CONSULTANT.
- PROVIDE AND INSTALL MINIMUM THREE(3) 6" MAGLIN BOLLARDS AT STOREFRONT ENTRANCE VESTIBULE LOCATIONS. REFER TO SPECS FOR FINISH. (REFER TO DET'L 7/A5.03)
- PROVIDE VERTICAL CONTROL JOINTS AT ALL WINDOW FRAMES/JAMBS ON EXTERIOR WALLS FROM T/O FLOOR SLAB TO U/S OF ROOF DECK. TYP. PROVIDE CONT. HORIZONTAL CONTROL JOINTS ALONG PERIMETER WALLS (INCLUDING VESTIBULE GYP. BOARD WALLS) AT 6" BELOW OWSJ. (REFER TO BUILDING SECTIONS 1/A4.01 & 2/A4.01)
- PROVIDE ROUGH-IN FOR LCBO SECURITY SHUTTER & MOTORIZED SUNSHADE AT VISION GLASS WINDOW LOCATIONS WHERE APPLICABLE. REFER TO DETAILS 3/A5.02, 6/A5.02, 9/A5.02 AND 12/5.02. COORDINATE LOCATIONS WITH LCBO.
- PROVIDE PLYWOOD BLOCKING AT VISION GLASS WINDOW JAMBS AND HEAD FOR LCBO ROLLING SHUTTERS. REFER TO DETAILS 8/A5.01 & 3/A5.02. COORDINATE WITH LCBO.
- SIMILAR TO C3B EXCEPT FOR NOTE 2. G.C. TO PROVIDE ROUGH-IN FOR LCBO SECURITY SHUTTER AT VISION GLASS WINDOW LOCATIONS WHERE APPLICABLE.
- CROSS BRACING - CONFIRM & COORDINATE REQUIREMENTS WITH STRUCTURAL CONSULTANT
- CROSS BRACING - OFFSET BEHIND SPANDRELS. CONFIRM & COORDINATE REQUIREMENTS WITH STRUCTURAL CONSULTANT
- SIMILAR TO C3B. GLAZING TO RECEIVE MANUAL SHADES
- ROOF ACCESS HATCH ABOVE TENANT SERVICE PLATFORM. ACCESS HATCH BY THIS CONTRACTOR. LADDER AND SAFETY POST SUPPLIED AND INSTALLED BY TENANT. REFER TO DETAIL 14/A5.04.
- DASHED LINES DENOTE OUTLINE OF LCBO BEER COLD ROOM. (LANDLORD TO ENSURE MINIMUM OF 6" OVERHEAD CLEARANCE FROM T/O LCBO BEER COLD ROOM TO U/S OF STRUCTURE IS PROVIDED). EXACT LOCATION AND SIZE OF TENANT COLDROOM TO BE CONFIRMED WITH TENANT PROVIDED FIXTURE PLAN AND COORDINATION
- CONCRETE SLAB ON GRADE TYPICAL THROUGHOUT. CONFIRM & COORDINATE REQUIREMENTS WITH STRUCTURAL CONSULTANT
- SAW CUTS IN WAREHOUSE ARE TO BE CLEANED AND FILLED WITH EUCCO QWIKJOINT UVR JOINT FILLER (REFER TO LBRR SPECS)
- CONCRETE SLAB IN WAREHOUSE TO RECEIVE HARDENER AND SEALER (REFER TO LBRR SPECS). EXTENT OF WAREHOUSE TO BE CONFIRMED.
- SLAB THICKENING FOR FUTURE LCBO SERVICE PLATFORM, CONFIRM & COORDINATE REQUIREMENTS WITH STRUCTURAL CONSULTANT. SERVICE PLATFORM ABOVE (BY TENANT) TO BE CONFIRMED
- PROVIDE 3/4" IN-WALL PLYWOOD BLOCKING FOR LCBO SERVICE PLATFORM STAIR WALL MOUNTED HANDRAILS (**WHERE APPLICABLE AND WHEN). LOCATION TO BE CONFIRMED BY LCBO WHERE APPLICABLE. REFER TO DWG. 6/A5.01.
- PROVIDE ROUGH-IN FOR DOOR BUZZER AT 4'-0" A.F.F. ON LATCH SIDE OF DOOR, TYP.
- PROVIDE 6" 4'-0" HIGH CONC. FILLED STEEL BOLLARDS. (REFER TO 8/A5.03, TYP.) SEE TYPICAL NOTE-8 FOR FINISH
- REINFORCED CONC. TRUCK RAMP (CONFIRM & COORDINATE REQUIREMENTS WITH STRUCTURAL CONSULTANT, PER LBRR SPEC SECTION 32 13 13)
- LINE OF SHELTER ABOVE
- PROVIDE 8" CONC. FILLED STEEL BOLLARD. (REFER TO 8/A5.03, TYP.) AT GAS METER LOCATIONS. SEE TYPICAL NOTE-8 FOR FINISH.
- GAS METER LOCATION. GAS METER LINE SHALL RISE UP THE SIDE OF THE BUILDING AND PENETRATE PARAPET
- PROVIDE LCBO SPECIFIED NUMBER OF BOLLARDS, LOCATED IN FRONT OF VISION GLASS AND STORE ENTRANCE VESTIBULE AT LOCATIONS SUBJECT TO VEHICULAR DAMAGE. REFER TO DETAIL 7 & 8/A5.03 FOR SIZES AND FINISH.
- STEEL TUBE BIKE RACKS. SERIES:MBR-500. DIRECT BURIAL FOR NEW SIDEWALKS. REFER TO LBRR SPEC FOR FINISH. INSTALLATION TO SUIT RESPECTIVE MUNICIPALITY GUIDELINES. QUANTITY & FINAL LOCATION TO BE CONFIRMED BY LCBO.
- 8" CONC. FILLED STEEL BOLLARD. SEE TYPICAL NOTE-7 FOR FINISH. (REFER TO 8/A5.03) TYP.
- MASONRY SCREEN WALL (REFER TO A5.04)
- CONC. WHEEL STOP CURB. REFER TO BASE BLDG STRUCT. DWGS
- MAIN DOOR: 1) MAN DOOR TO BE EQUIPPED WITH TEMPORARY PANIC DEVICE BY G.C. (EXIT DEVICES SUPPLIED AND INSTALLED BY THE TENANT) G.C. TO PROVIDE ROUGH-IN FOR DOOR BUZZER (4'-0" A.F.F. ON LATCH SIDE OF THE DOOR). HM DOOR PREPARED TO RECEIVE TENANT'S 4 POINT EXIT DEVICE. PANIC DEVICE AND DOOR VIEWER BY BASE BUILDING G.C.
- CONC. CURB B/S OF RAMP. REFER TO STRUCTURAL DRAWINGS
- BARRIER FREE TACTILE PLATE TO CONFORM TO OBC 3.4.6.1.(iii)
- GALVANIZED METAL RAILING (SEE DETAIL 6/A5.06)
- HEAVY DUTY ASPHALT TRUCK RAMP. CONFIRM & COORDINATE REQUIREMENTS WITH STRUCTURAL CONSULTANT.
- DOCK LEVELER
- PROVIDE RAIN WATER LEADER CLEAN OUT COMPLETE WITH ACCESS PANEL AT LOWER LEVEL, 4" A.F.F.
- CONCRETE SLAB TO HAVE A LEVELED SURFACE AND SMOOTH FINISH C/W CONTROL JOINTS. G.C. TO PROVIDE TEST RESULT FOR FLOOR FLATNESS AT 72 HOURS AFTER POUR AND ONE WEEK PRIOR TO POSSESSION [MINIMUM FLOOR FLATNESS REQUIREMENTS: TESTING AT 72 HOURS (CSA STANDARD): FF=50, FL=40. TESTING AT 1 WEEK BEFORE HANDOVER (CSA STANDARD): FF=45, FL=35] ANY DEFECTS IN THE FLOOR, INCLUDING BUT NOT LIMITED TO CURLING, CRACKING, BREAKING UP, HEAVING, SINKING, ETC. WILL BE THE RESPONSIBILITY OF THE G.C. TO CORRECT IMMEDIATELY AT NO ADDITIONAL COST. REFER TO STRUCTURAL DRAWINGS, TYP.
- SWITCHBOARD, REFER TO ELECTRICAL DRAWINGS. PROVIDE 3/4" FIRE RATED PLYWOOD BEHIND PANELS, TYP.
- PROVIDE FIRE-RATED EXTERIOR WALL ASSEMBLIES WHERE REQUIRED, IN ACCORDANCE WITH OBC
- FOR DEMISING WALLS ABUTTING ADJACENT TENANTS, LANDLORD'S ARCHITECT TO PROVIDE RATED WALL ASSEMBLIES REQUIRED TO SUIT SITE CONDITIONS, C/W SECURITY MESH.
- INFLATABLE TRUCK SHELTER: SERCO MODEL #S1-450, BY SERCO. REFER TO SPECIFICATIONS

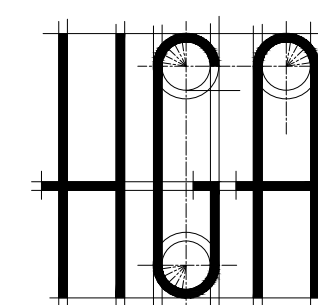

HANNA, GHOBRIAL
AND ASSOCIATES LTD.

engineering
architecture

3100 Temple Drive, Suite 100
Windsor, ON N9W 5J6
(519) 945-7373 FAX.-5636

This drawing shall not be used for construction unless it is countersigned by the CONSULTANT

NOTE: ENGINEERED SHOP DRAWINGS, FOR ANY MANUFACTURED COMPONENT FORMING PART OF THE BUILDING (i.e. ENGINEERED ROOF TRUSSES, ENGINEERED FLOOR JOISTS, TIMBERS, ETC.) MUST BE SUBMITTED TO HANNA GHOBRIAL & ASSOCIATES, LTD. FOR REVIEW AND APPROVAL. IF ENGINEERED SHOP DRAWINGS ARE NOT SUBMITTED AND APPROVED, HANNA GHOBRIAL & ASSOCIATES, LTD. WILL NOT BE RESPONSIBLE FOR ANY ASSOCIATED COSTS OR DAMAGES.

ALL DRAWINGS, SPECIFICATIONS AND OTHER RELATED DOCUMENTS ARE THE COPYRIGHT PROPERTY OF THE CONSULTANT AND SHALL BE RETURNED UPON REQUEST. REPRODUCTION OF DRAWINGS AND RELATED DOCUMENTS, IN WHOLE OR IN PART, IS FORBIDDEN WITHOUT THE WRITTEN PERMISSION OF THE CONSULTANT. THE CONTRACTOR SHALL CHECK AND VERIFY ALL PERTINENT DIMENSIONS AND REPORT ANY DISCREPANCIES TO THE CONSULTANT BEFORE PROCEEDING WITH THE WORK. THIS DRAWING SHALL NOT BE USED FOR CONSTRUCTION UNLESS IT IS COUNTERSIGNED BY THE CONSULTANT. THIS DRAWING IS NOT TO BE SCALED. USE FIGURED DIMENSIONS ONLY.

12		
11		
10		
9		
8		
7	2023/09/26	SPA - REV. TRUCK ROUTE
6	2023/09/06	SITE PLAN APPLICATION
5	2023/08/15	PHOTOMETRIC ANALYSIS
4	2023/08/03	CLIENT REVIEW
3	2023/07/31	PRE-SUBMITTAL APPLIC.
2	2023/07/26	CLIENT REVIEW
1	2023/06/21	SITE PLAN APPLICATION

YY/MM/DD

No Date: Issued For:

Date: JUNE 2023

Drawn By: H.R.

Checked By: E.K.

Client:
Joseph B. Mikhail
Mikhail Holdings Ltd.
100 Ouellette Ave., Suite 700
Windsor, ON, N9A 6T3

Project Title:

LCBO

NEW

LCBO STORE

Address: 400 SANDWICH STREET
AMHERSTBURG, ONTARIO N9V 3L4

Project No.:

22-0445


Sheet Title:

GROUND FLOOR AND
SERVICE PLATFORM
CONSTRUCTION PLANS


Sheet No.:

A1.01


FILE LOCATION: \\037-0445 New LCBO Amherstburg_402_Signage_Schematics_Markup\Construction Documents\A2.01 Elevations.dwg

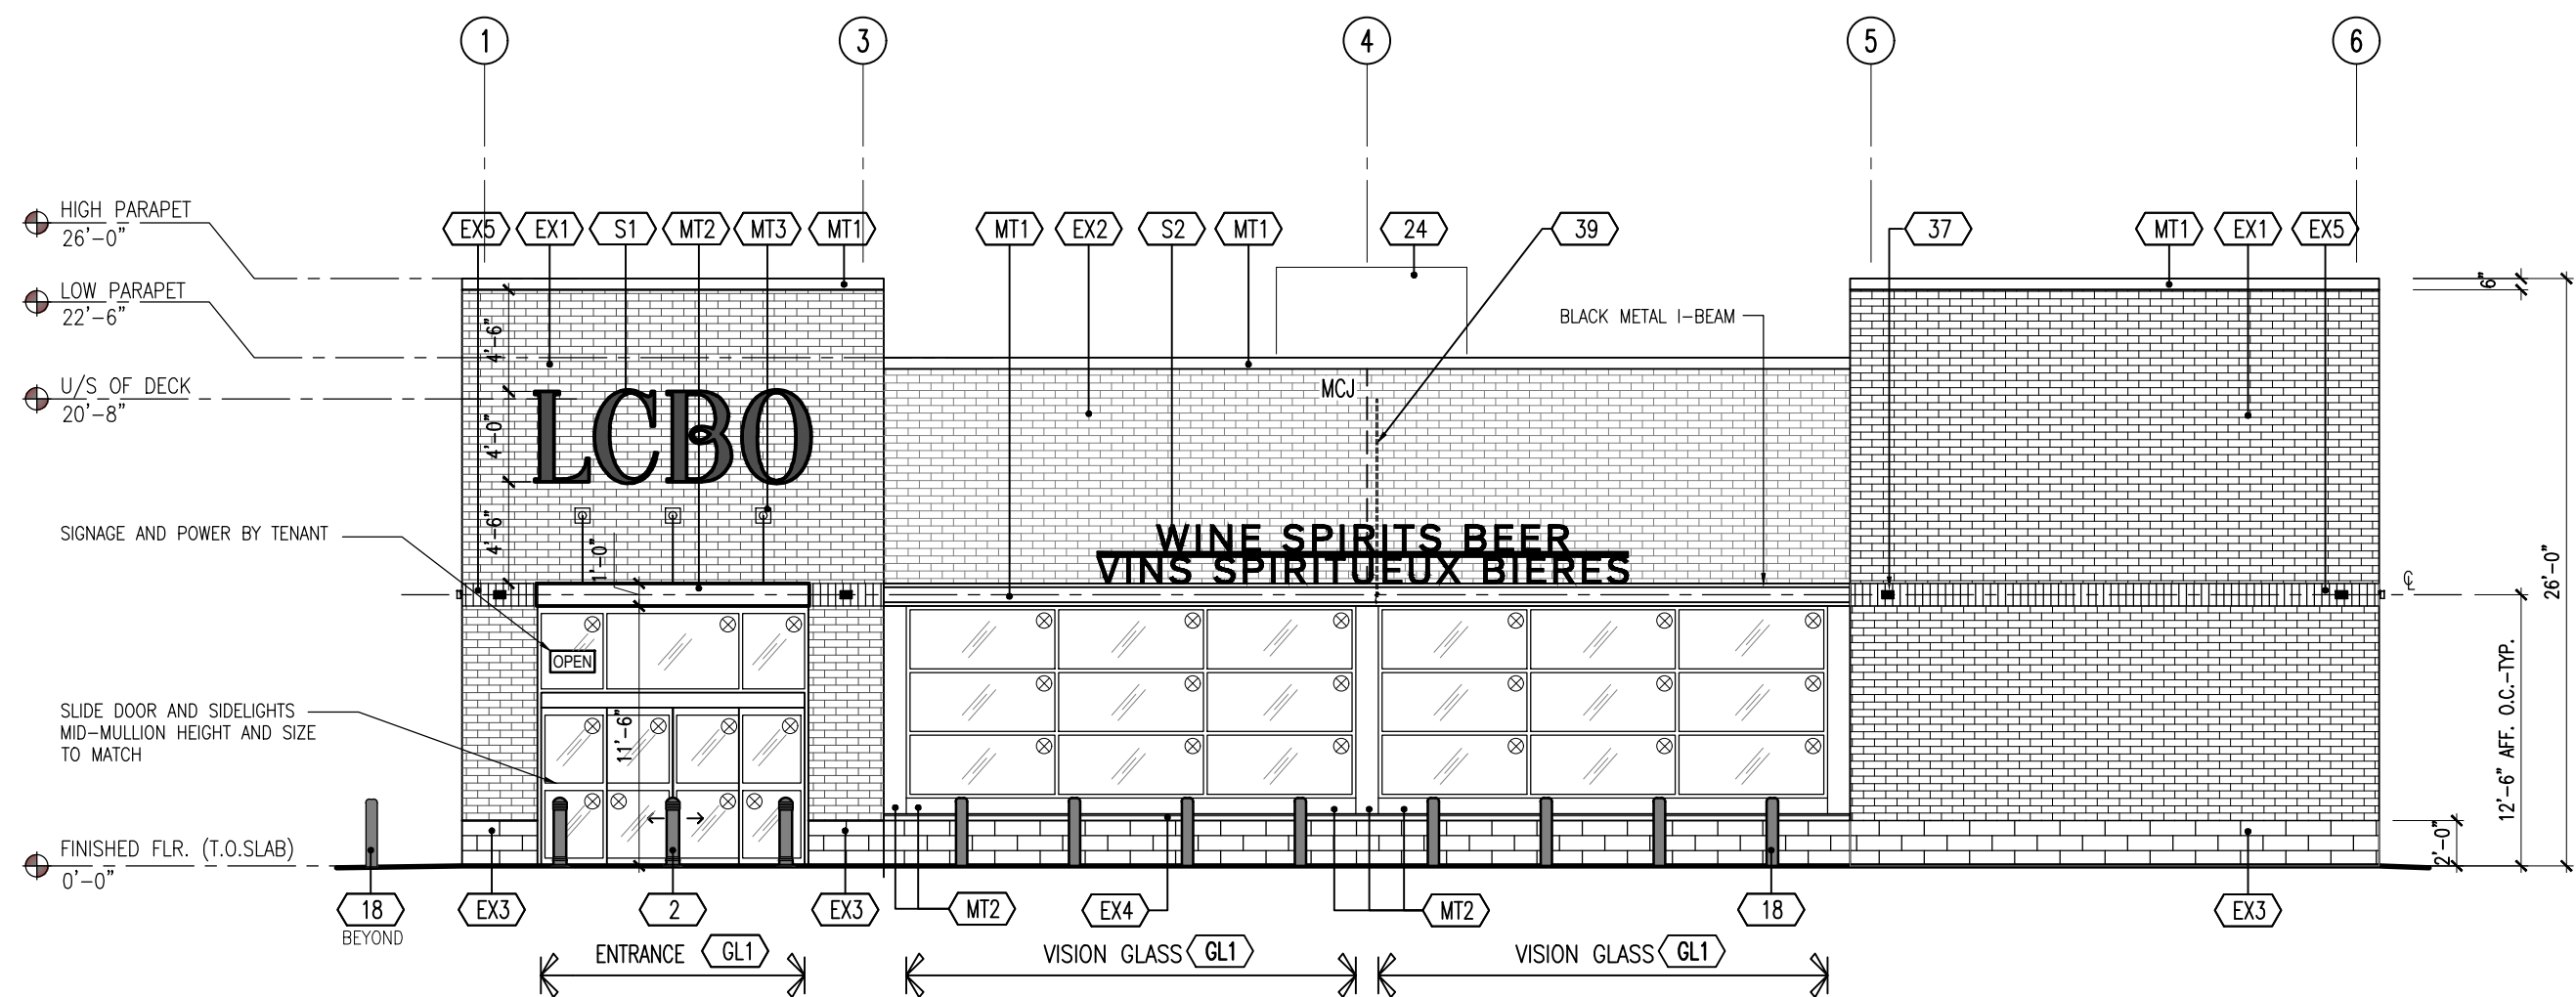


1 EAST ELEVATION (MAIN ENTRANCE)
SCALE: 1/8" = 1'-0"

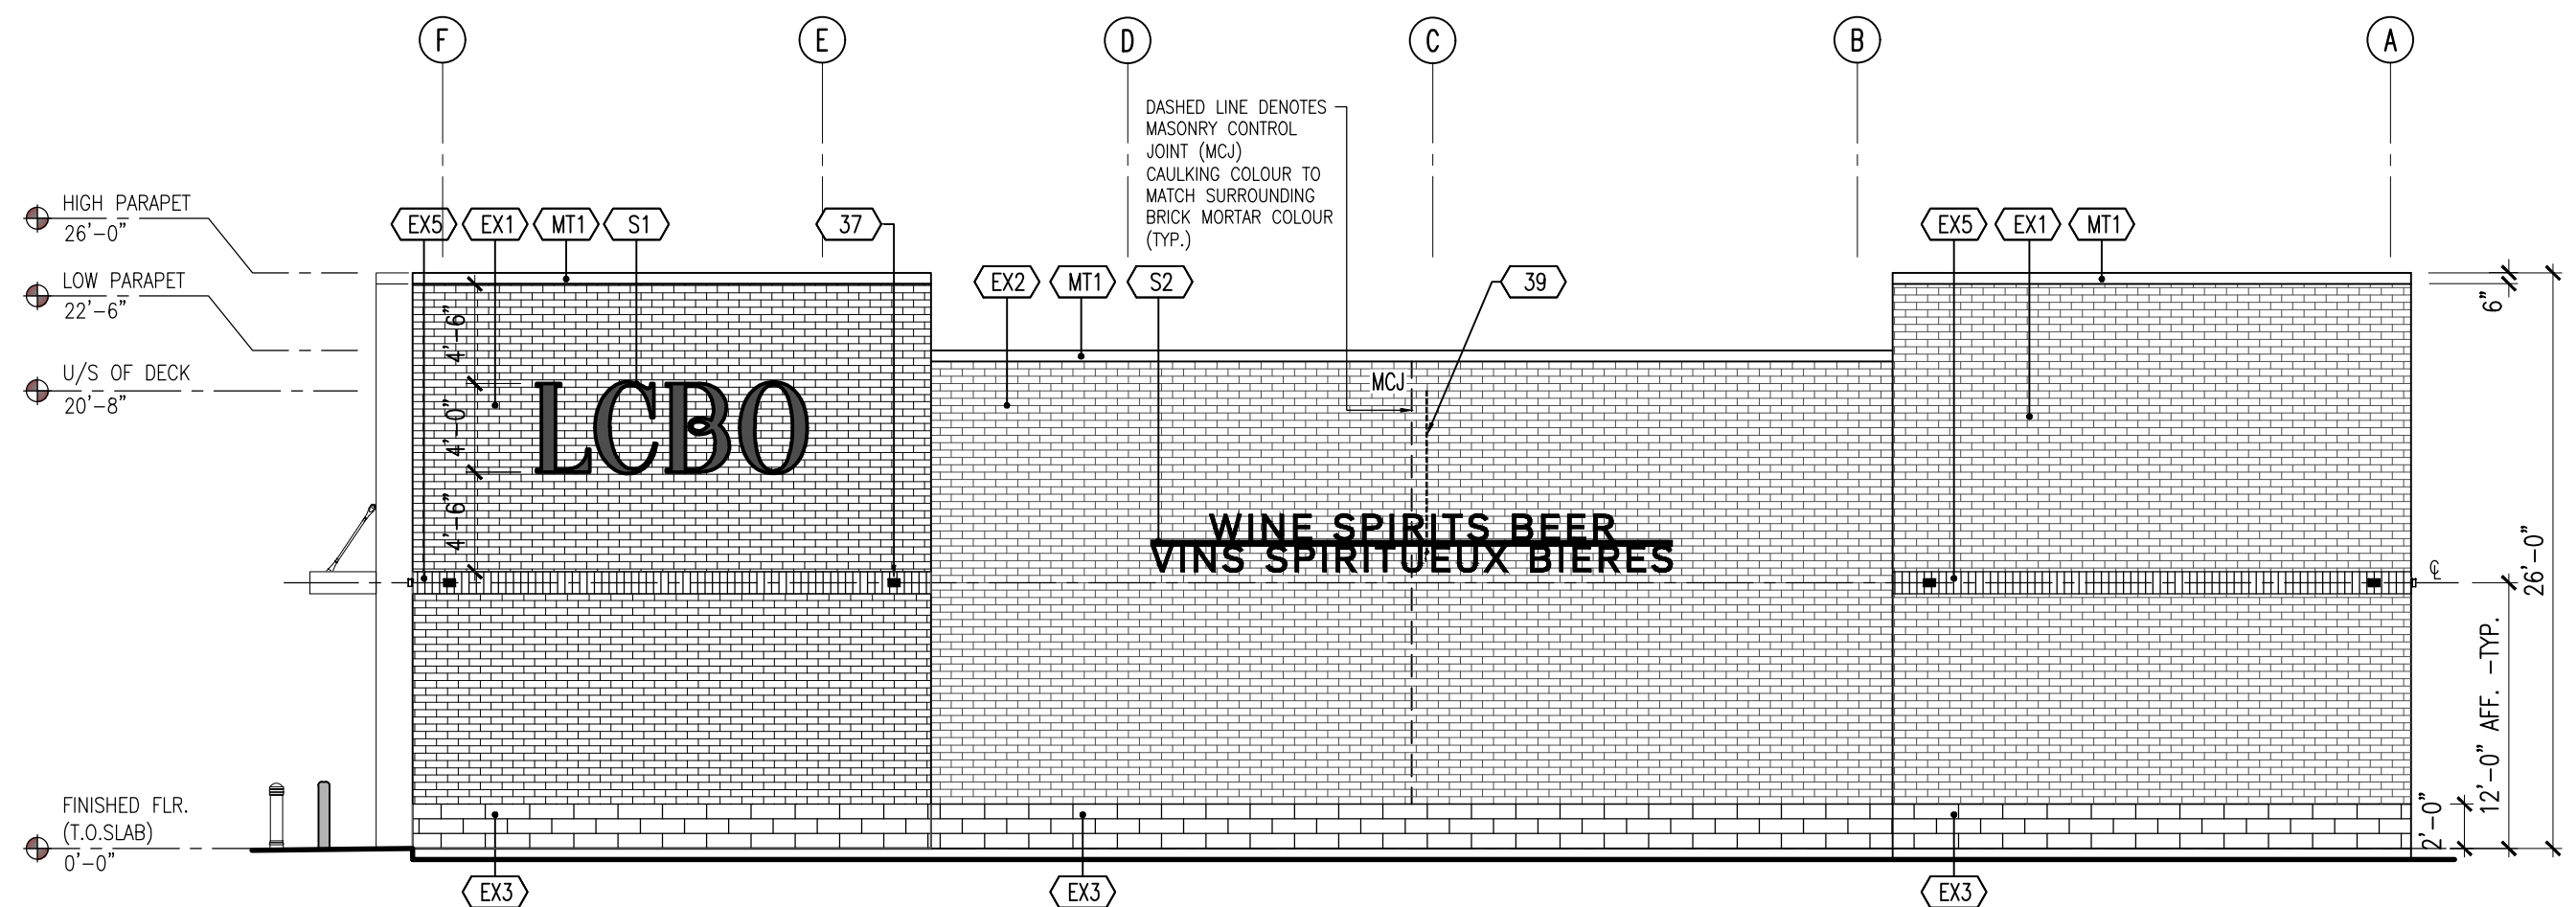


4 NORTH ELEVATION
SCALE: 1/8" = 1'-0"

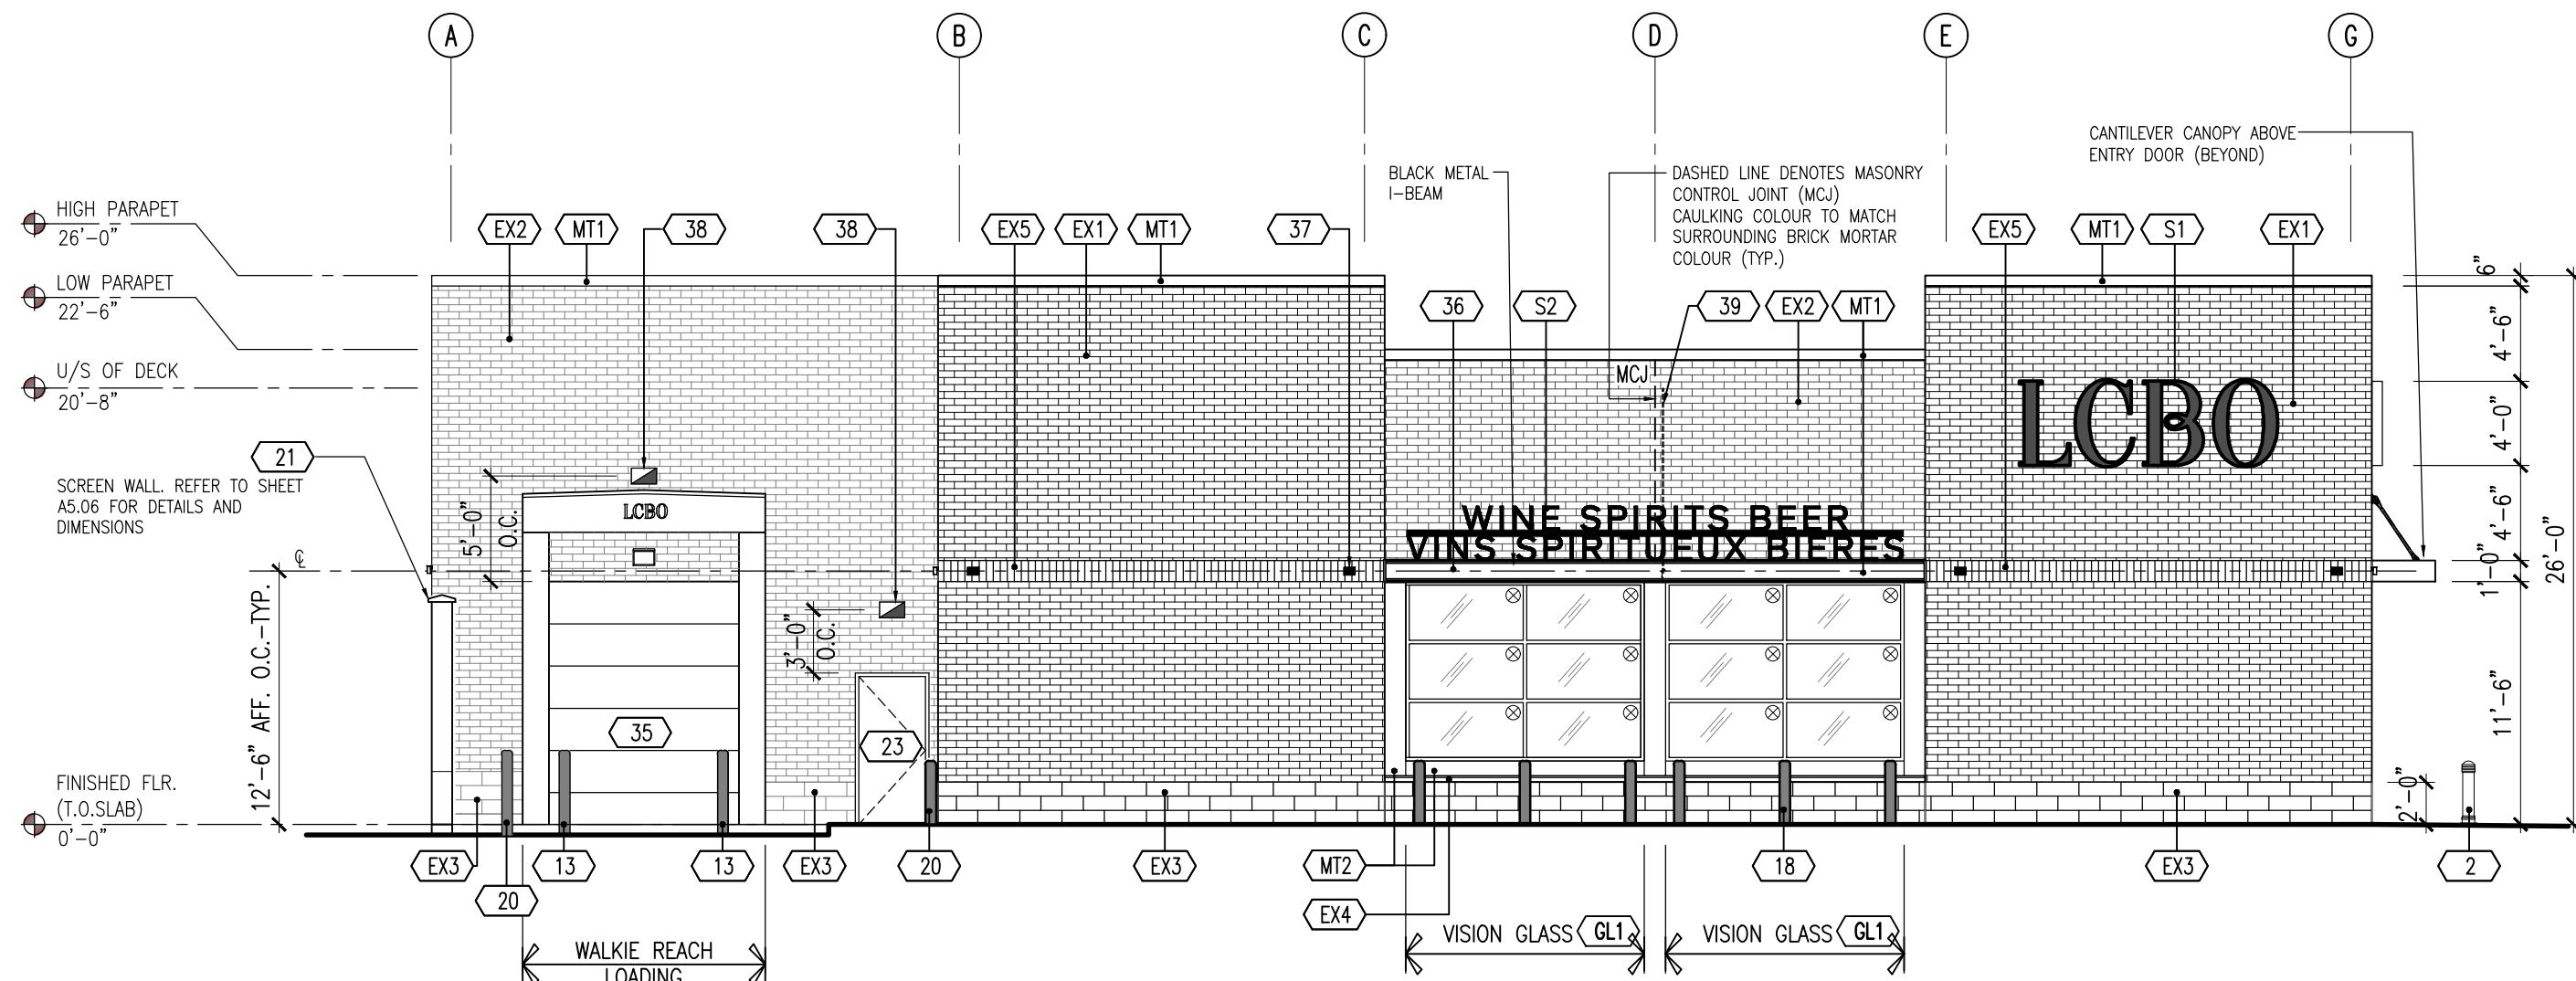

2 SOUTH ELEVATION
SCALE: 1/8" = 1'-0"

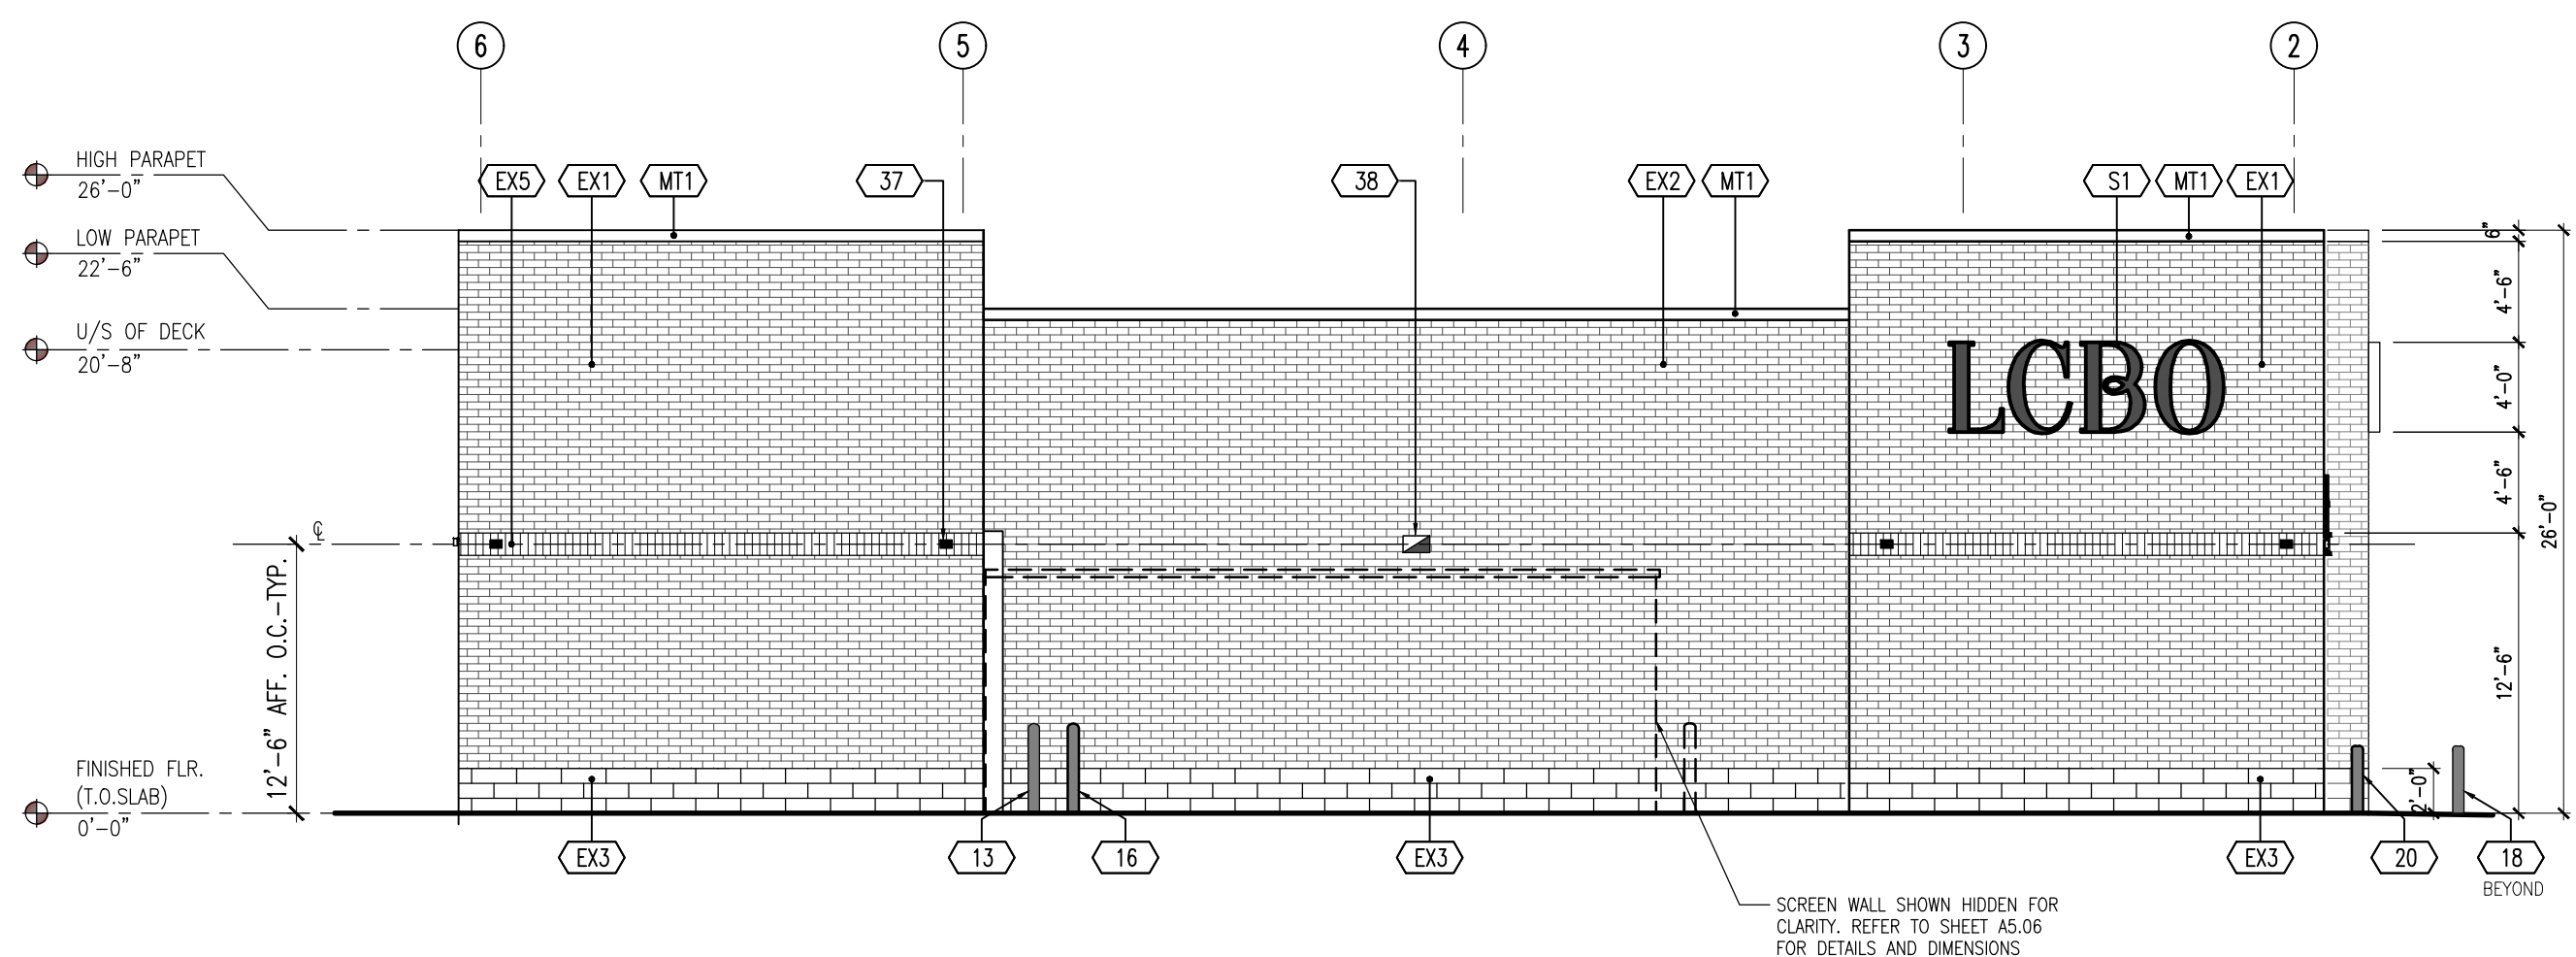


3 WEST ELEVATION
SCALE: 1/8" = 1'-0"

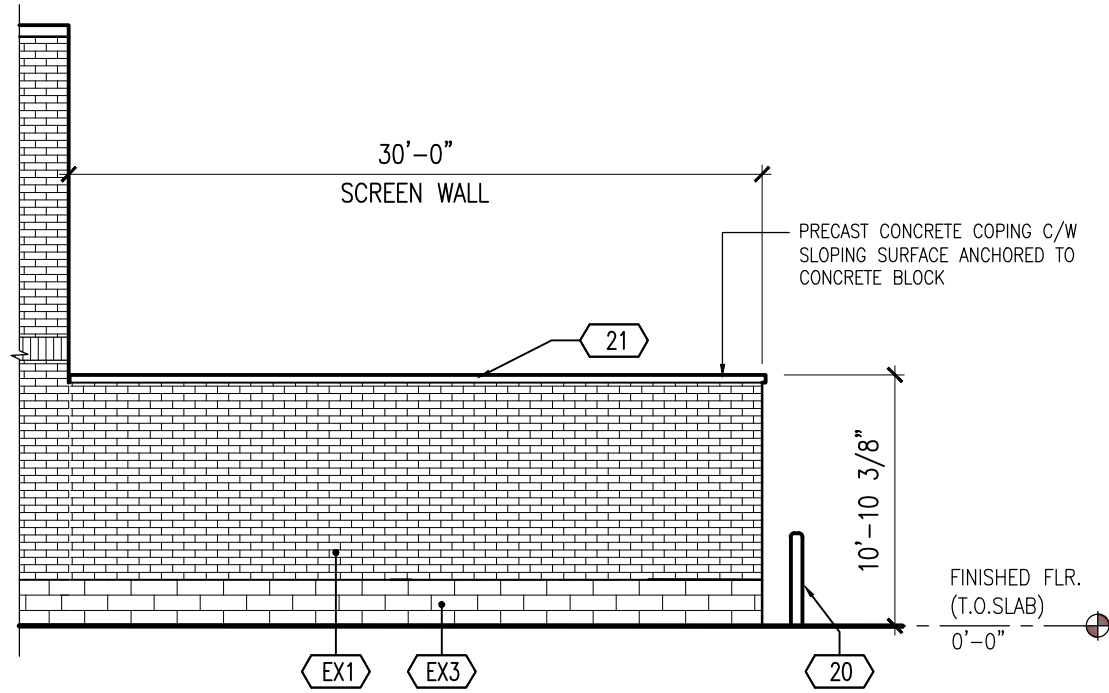

WEST ELEVATION OF SCREEN WALL
SCALE: 1/8" = 1'-0"

LEGEND	
EX1 BRICK WALLS: DARK GREY COLOUR: URBAN BRICK "GALAXY" SIZE: 57MM H. X 90MM D. X 397MM L. MORTAR COLOUR: BETOMIX - EBONY - 15151S30 MANUFACTURER: MERIDIAN BRICK, BURLINGTON, ON, L7R 3Y2 C: 416-801-1638 CONTACT: TERRY KLINGSPHORN	2 BOLLARDS AT MAIN ENTRANCE: PRODUCT: MTB651 MANUFACTURER: MAGLIN FURNITURE SYSTEMS OR APPROVED ALTERNATIVE: COLOUR: BLACK GLOSS FINISH QUANTITY: REFER TO CONSTRUCTION PLAN A1.01 (REFER TO DETAIL 7/A5.03)
EX2 BRICK WALLS: WARM GREY COLOUR: URBAN BRICK SMOOTH "POLAR" SIZE: 57MM H. X 90MM D. X 397MM L. MORTAR COLOUR: BETOMIX - WHITE - 1510S30 MANUFACTURER: MERIDIAN BRICK, BURLINGTON, ON, L7R 3Y2 C: 416-801-1638 CONTACT: TERRY KLINGSPHORN	13 PROVIDE 6"X 4'-0" HIGH CONC. FILLED STEEL BOLLARDS. (REFER TO 8/A5.03, TYP.) SEE TYPICAL NOTE-8 FOR FINISH 18 6"X CONCRETE FILLED STEEL BOLLARD BY LANDLORD. (REFER TO DETAIL 8/A5.03)
EX3 CONCRETE BLOCK BASE: PRODUCT: CAMBRIDGE SERIES COLOUR: DIAMOND BLACK, FINISH: STIPPLED MORTAR COLOUR: BETOMIX - EBONY - 15151S30 DISTRIBUTED BY: RICHVALE YORK BLOCK INC., GORMLEY, ON TEL: 416-213-7444 EXT. 236 CONTACT: LUCIANO TESEO EMAIL: lteeso@richvalenyork.bellnet.ca ORDER DESK: 416-213-7447	20 8"X CONCRETE FILLED STEEL BOLLARD BY LANDLORD. (REFER TO DETAIL 8/A5.03) 21 SCREEN WALL
EX4 CONCRETE SILL: PRODUCT: CAMBRIDGE ARCHITECTURAL SILL R24-225 ANGLED COLOUR: DIAMOND BLACK, FINISH: STIPPLED DISTRIBUTED BY: RICHVALE YORK BLOCK INC., GORMLEY, ON TEL: 416-213-7444 EXT. 236 CONTACT: LUCIANO TESEO EMAIL: lteeso@richvalenyork.bellnet.ca ORDER DESK: 416-213-7447	22 POURED CONCRETE FOUNDATION: SAND-BLAST FINISH, GRIND OFF CLEAN OF ALL FORMWORK LINES, ACCESSORIES AND DEBRIS 23 INSULATED H.M. DOOR & FRAME: PAINT: BENJAMIN MOORE #HC-172 "REVERE PEWTER" PRODUCT: FP29 DTM SEMI-GLOSS, PRIMER: FP04 DTM
EX5 BRICK SOLDER COURSE: DARK GREY COLOUR: AU BRICK SMOOTH - "GALAXY" SIZE: 90MM H. X 90MM D. X 290MM L. MORTAR COLOUR: BETOMIX - EBONY - 15151S30 MANUFACTURER: MERIDIAN BRICK, BURLINGTON, ON, L7R 3Y2 C: 416-801-1638 CONTACT: TERRY KLINGSPHORN	24 PREFINISHED METAL SCREEN FOR RTU: COLOUR: TBS (REFER TO ROOF PLAN DWG. FOR ADDITIONAL INFORMATION) 25 INFLATABLE TUBE SHELTER: SERCO MODEL #S1-450, BY SERCO, C/W LIGHT GREY TRANSLUCENT PANELS. REFER TO SPECIFICATIONS
GL1 DOOR AND WINDOW FRAMES: CATEGORY: BLACK ALUMINUM FINISH COLOUR: BLACK MANUFACTURER: KAWNEER T: 905-673-5400 CONTACT: SUSIE DIAGRACA	35 PREFINISHED INSULATED METAL VERTICAL HIGH LIFT DOOR: COLOUR: WHITE OVERHEAD DOOR BENT STEEL FRAME FINISH: COLOUR: *BENJAMIN MOORE #HC-172 "REVERE PEWTER" (EXTERIOR GRADE). FINISH: ALKYO, LOW LUSTRE.
GL2 SPANDREL GLASS: ICD COATING OPAC COAT 300 COLOUR: #3-0770 "WARM GREY" W/RO CLEAR (6mm) BY: ICD COATINGS, T: 360-546-2286 LANDLORD TO PROVIDE GLASS SAMPLE W/ SPANDREL COLOUR APPLIED FOR LCBO CONSTRUCTION COORDINATOR'S APPROVAL.	36 C-SHAPED ALUM. COMPOSITE PANEL SYSTEM (ACM CHANNEL) AS PER ARCH'L DETAILS. USE MECH'L FASTENERS INTO BRICK (TYP.)
MT1 PREFINISHED METAL FLASHING: (CANOPY, PARAPET & HORIZONTAL BEAM DETAILS): PRODUCT: ALPOUC - ALUMINUM COMPOSITE PANEL COLOUR: TBS BLACK #101220 (MATTE)	37 EXTERIOR 1-WAY LIGHT FIXTURE (DOWN ONLY): (FIXTURE BY LCBO), ROUGH-IN BY BASE BUILDING
MT2 PREFINISHED METAL DAPPING: (CANOPY, TOP, SIDES & BOTTOM OF GLAZING SYSTEM) PRODUCT: ALPOUC - ALUMINUM COMPOSITE PANEL COLOUR: TBS BLACK #101220 (MATTE)	38 EXTERIOR SECURITY LIGHT FIXTURE: FIXTURE BY LCBO - ROUGH-IN BY BASE BUILDING
MT3 DECORATIVE TENSION RODS: 28mmØ DECORATIVE TENSION RODS C/W 8"x8" SQUARE MOUNTING PLATES WALL MOUNTED TO BRICK MASONRY WALL & SECURED TO CANOPY STRUCTURE. MANUFACTURE: OF LAURENCE OR APPROVED ALTERNATE. FINISH: BLACK POWDERCOAT	39 IN-WALL CONDUIT AND PULL STRING TO U/S OF ROOF DECK WITH SUB-OUT ON EXTERIOR FACE OF WALL, C/W PULL STRING AT EXTERIOR SIGNAGE LOCATIONS. REFER TO WALL SECTIONS, COORDINATE WITH LCBO COORDINATOR AND LCBO DESIGN DRAWINGS.
S1 LCBO CHANNEL LETTER SIGNAGE (LED ILLUMINATED): LCBO 48" HIGH ILLUMINATED CHANNEL LETTERS: 1. FABRICATED ALUMINUM LETTERS W/ 3/4" WHITE ACRYLIC FACES COVERED W/ 3M 3735-60 DIFFUSER FILM WHITE. (PROVIDE 1 CONDUIT PER LETTER) 2. 1" MIKAL TRIM CAP W/ FIN. BLACK 3. 3/4"THK. X 5"TOP ALUMINUM CHANNEL CANISTERS W/ BLACK AUTOMOTIVE PAINT. 4. CENTER LOOP OF LETTER "B" TO BE HOLLOW. 5. INTERNAL WHITE LED - ALLANSON STORMTIGHT II LED ACUL-CWZ-100 W/ WATERPROOF TRANSFORMERS 6500K	MCJ 1/2" MASONRY CONTROL JOINT. CAULKING COLOUR TO MATCH SURROUNDING BRICK MORTAR COLOUR (TYP.)
GLAZING LEGEND ⊗ SEALED DOUBLED GLAZED UNITS	
GENERAL NOTES: 1. SIGNAGE MANUFACTURER TO CONFIRM ALL FONTS, ARTWORK, MATERIALS, FINISHES AND CONSTRUCTION OF FIN-ON LETTERS AND CHANNEL LETTERS WITH LCBO CONSTRUCTION COORDINATOR PRIOR TO FABRICATION OF THE ABOVE ITEMS. 2. BASE-BUILDING CONTRACTOR TO PROVIDE BLOCKING AS REQ'D AT ALL CHANNEL LETTERS, LIGHT FIXTURES, FIN-ON LETTERS, ETC. 3. ALL EXTERIOR SIGNAGE (CHANNEL LETTERS, "OPEN/CLOSE" SIGN, ETC.) ARE SUPPLIED AND INSTALLED BY LCBO. G.C. TO COORDINATE W/ RESPECTIVE VENDORS. 4. EXTERIOR 1-WAY LIGHT FIXTURE (DOWNLIGHT) BY SITEMAXLUX WALL MOUNTED USER BLADE MOUNT W/ WIDE FLOOD OPTIC BY IGUZZINI. PRODUCT CODE: E879. FINISH: GRAY/BLACK, IP RATING: 65 1x26WATT LED LAMP W/ RECESSED JUNCTION BOX (TYP.) CONTACT: BOZENA MALANCZAK PH: 416-403-3995 x222 5. ALL DIMENSIONS TAKEN FROM FINISHED FLOOR LEVEL.	

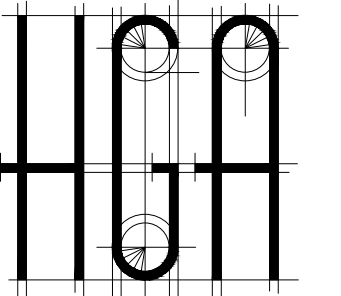

**HANNA, GHOBRIAL
AND ASSOCIATES LTD.**
engineering
architecture
3100 Temple Drive, Suite 100
Windsor, ON N9W 5J6
(519) 945-7373 FAX: -5636

This drawing shall not be used for construction unless it is countersigned by the CONSULTANT

NOTE:
ENGINEERED SHOP DRAWINGS, FOR ANY "MANUFACTURED COMPONENT" FORMING PART OF THE BUILDING (i.e. ENGINEERED ROOF TRUSSES, ENGINEERED FLOOR JOISTS, TIMERS, ETC.) MUST BE SUBMITTED TO HANNA GHOBRIAL & ASSOCIATES, LTD. FOR REVIEW AND APPROVAL. IF ENGINEERED SHOP DRAWINGS ARE NOT SUBMITTED AND APPROVED, HANNA GHOBRIAL & ASSOCIATES, LTD. WILL NOT BE RESPONSIBLE FOR ANY ASSOCIATED COSTS OR DAMAGES.

ALL DRAWINGS, SPECIFICATIONS AND OTHER RELATED DOCUMENTS ARE THE COPYRIGHT PROPERTY OF THE CONSULTANT AND SHALL BE RETURNED UPON REQUEST. REPRODUCTION OF DRAWINGS AND RELATED DOCUMENTS, IN WHOLE OR IN PART, IS FORBIDDEN WITHOUT THE WRITTEN PERMISSION OF THE CONSULTANT.

THE CONTRACTOR SHALL CHECK AND VERIFY ALL PERTINENT DIMENSIONS AND REPORT ANY DISCREPANCIES TO THE CONSULTANT BEFORE PROCEEDING WITH THE WORK. THIS DRAWING IS NOT TO BE USED FOR CONSTRUCTION UNLESS IT IS COUNTERSIGNED BY THE CONSULTANT. USE FIGURED DIMENSIONS ONLY.

12		
11		
10		
9		
8		
7	2023/09/26	SPA - REV. TRUCK ROUTE
6	2023/09/06	SITE PLAN APPLICATION
5	2023/08/15	PHOTOMETRIC ANALYSIS
4	2023/08/03	CLIENT REVIEW
3	2023/07/31	PRE-SUBMITTAL APPLIC.
2	2023/07/26	CLIENT REVIEW
1	2023/06/21	SITE PLAN APPLICATION
No	Date:	Issued For:

Date: JUNE 2023
Drawn By: H.R.
Checked By: E.K.

Client:
Joseph B. Mikhail
Mikhail Holdings Ltd.
100 Ouellette Ave., Suite 700
Windsor, ON, N9A 6T3

Project Title:

LCBO
NEW
LCBO STORE

Address: 400 SANDWICH STREET
AMHERSTBURG, ONTARIO N9W 3L4

Project No.:
22-0445


Sheet Title:

ELEVATIONS


Sheet No.:

A2.01


FILE LOCATION: \\032-0445 New LCBO Amherstburg_405 Sandwich Street_Loc_Mkdw/Construction Documents/A4.01 Building Sections.dwg

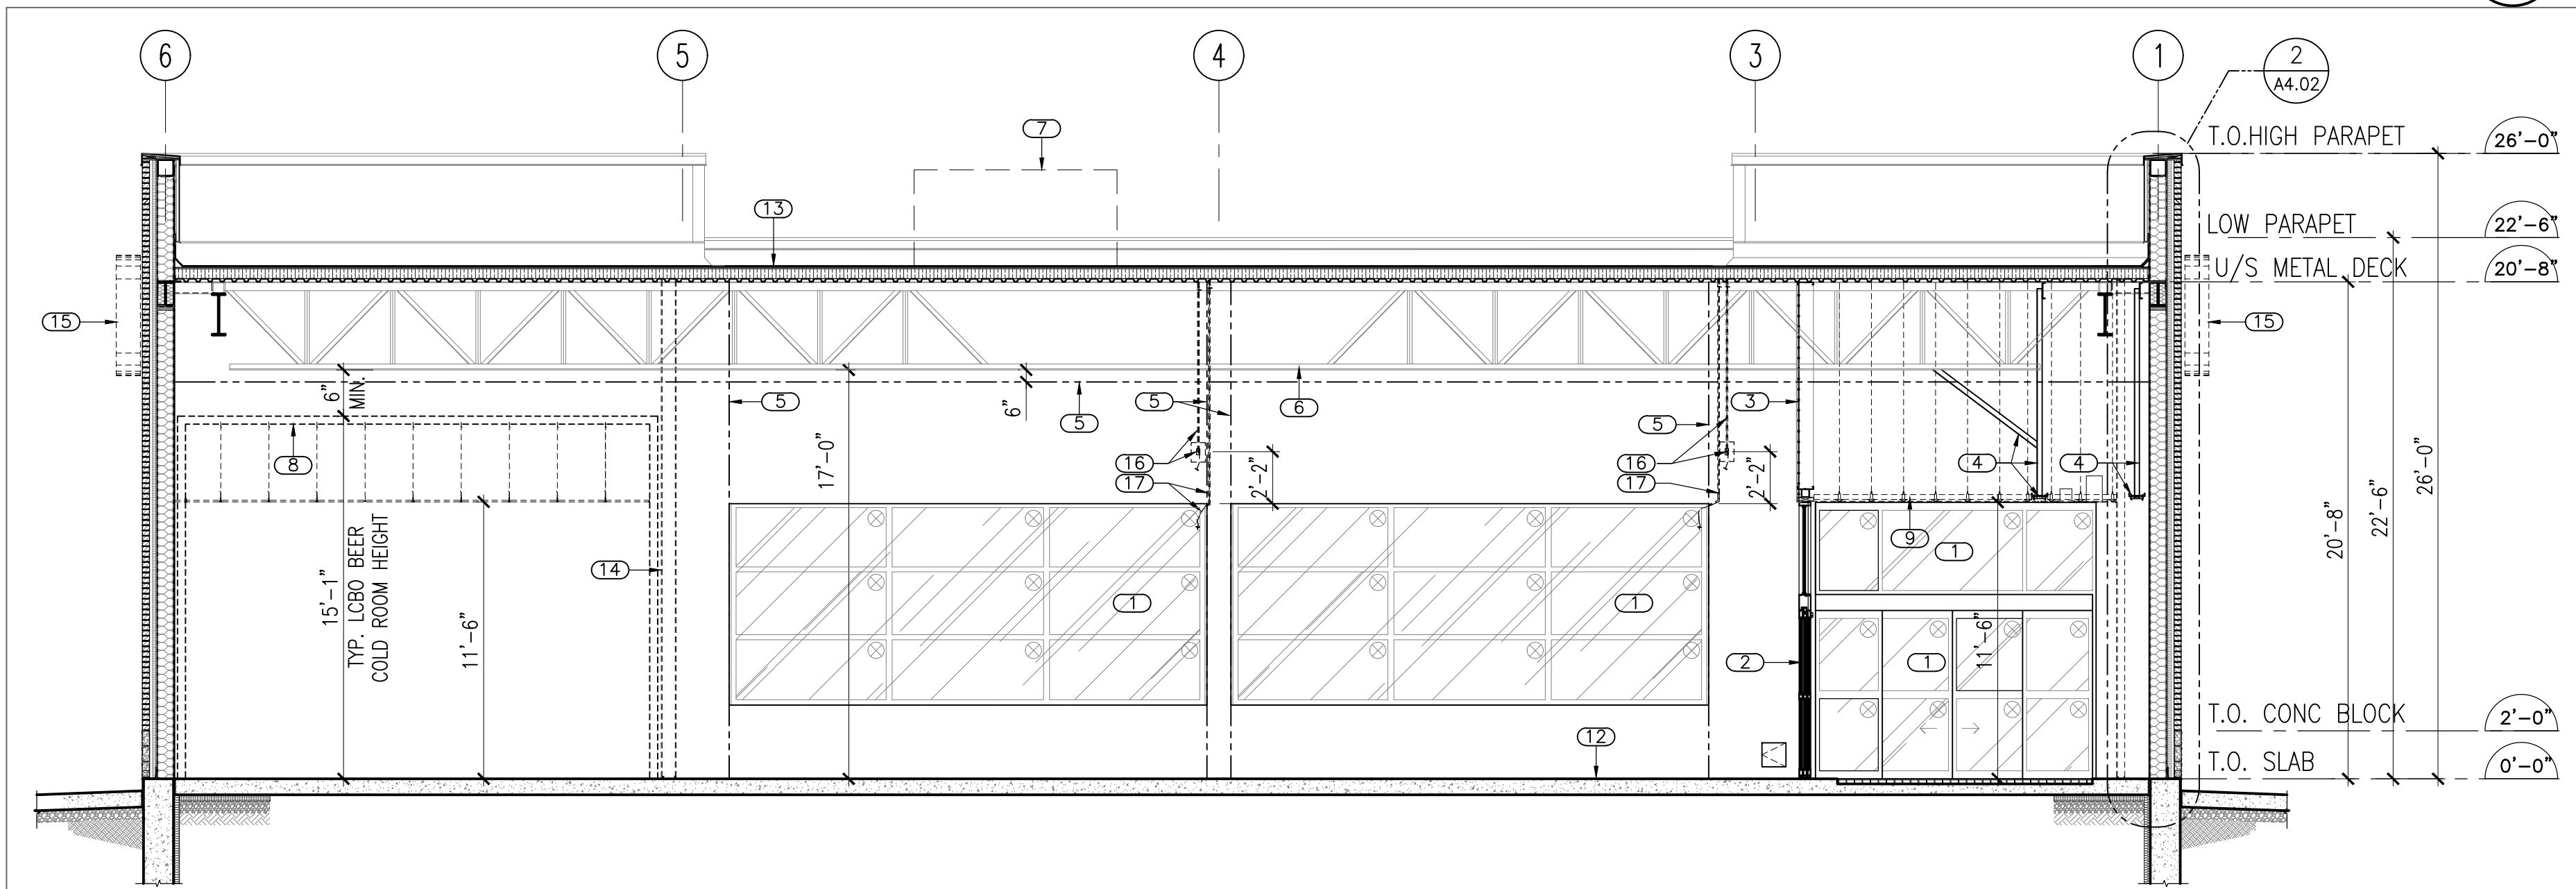

Building Section 1
Scale: 1/8"=1'-0" A4.01

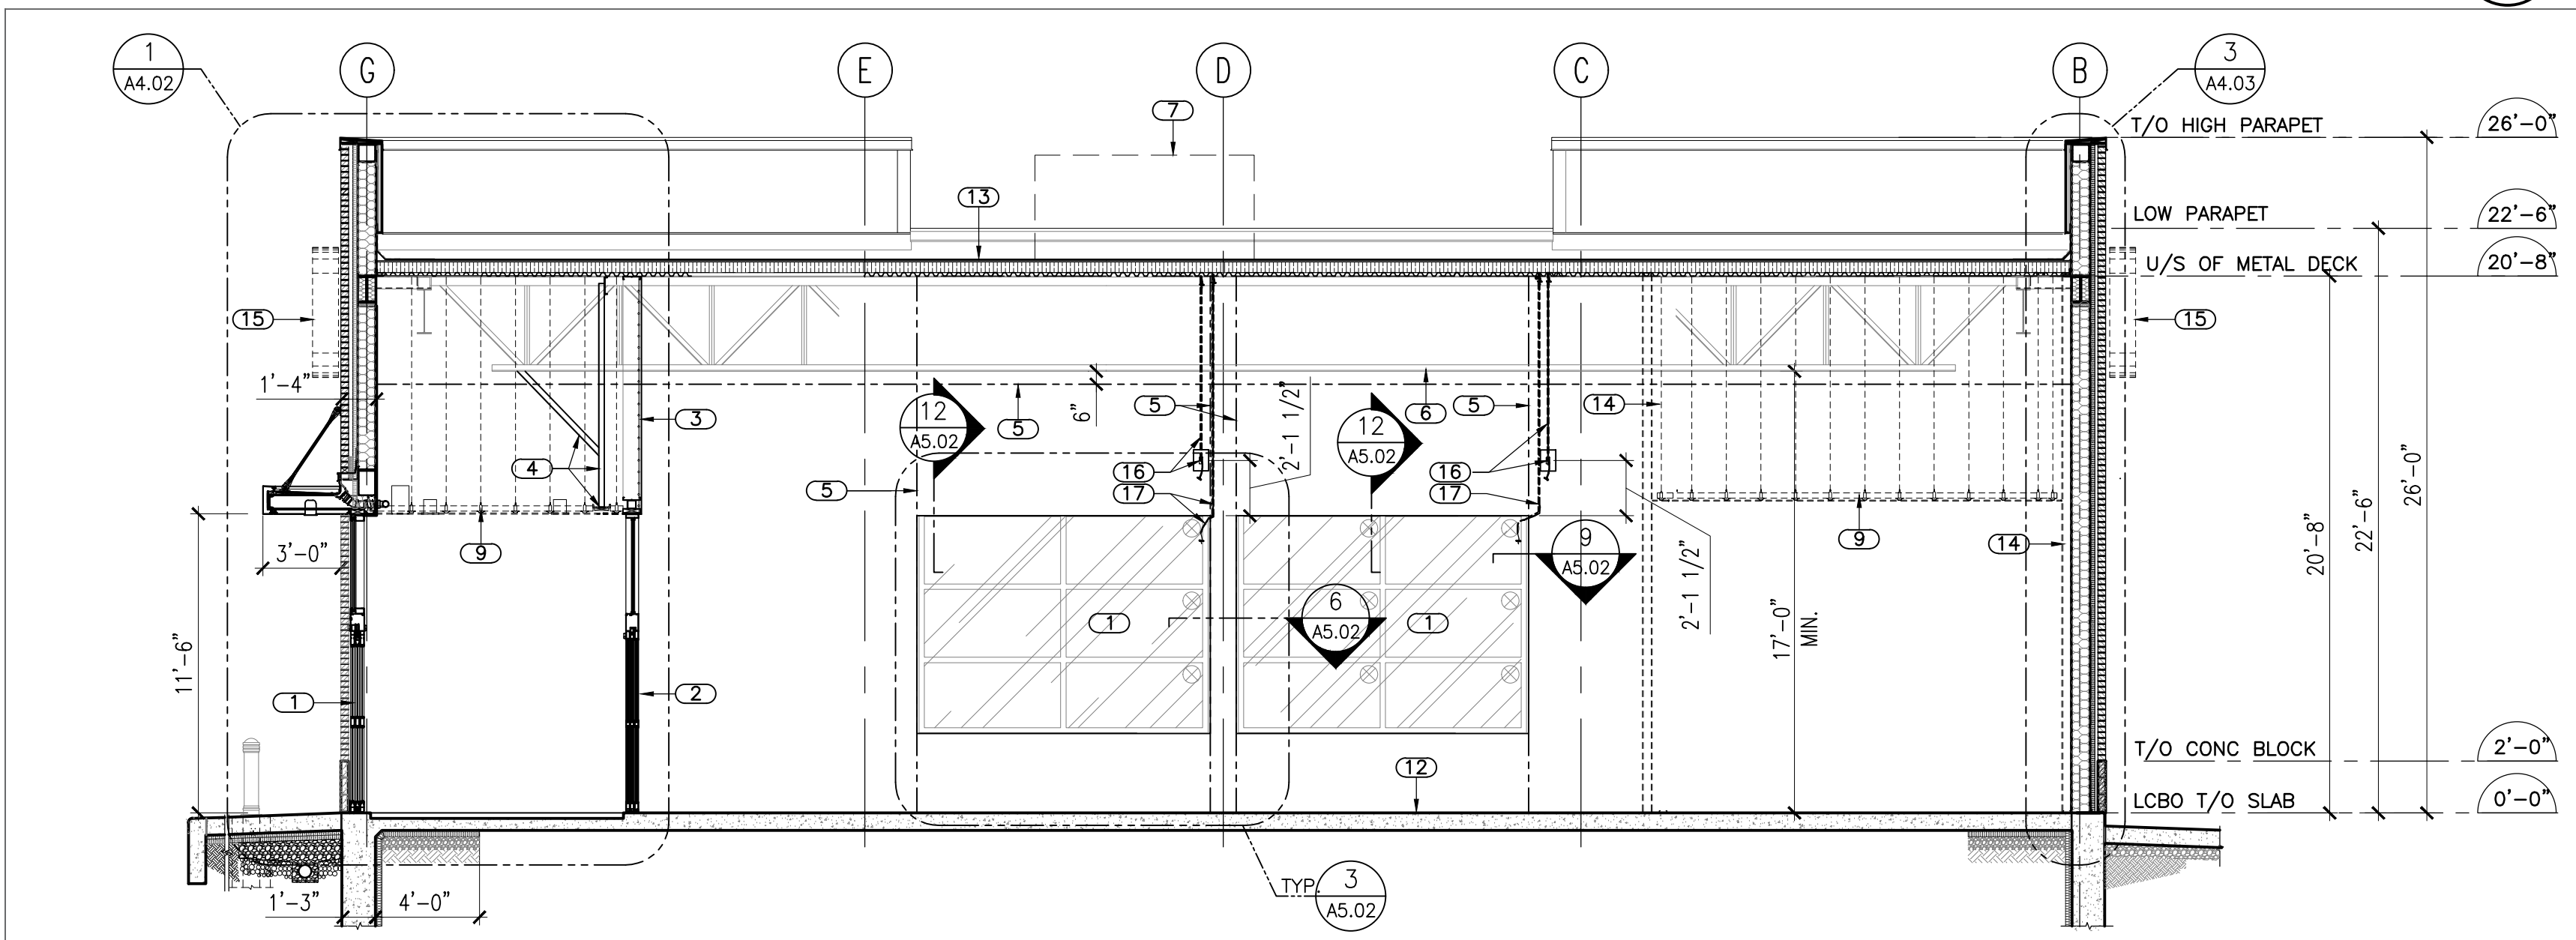


Building Section 2
Scale: 3/16"=1'-0" A4.01

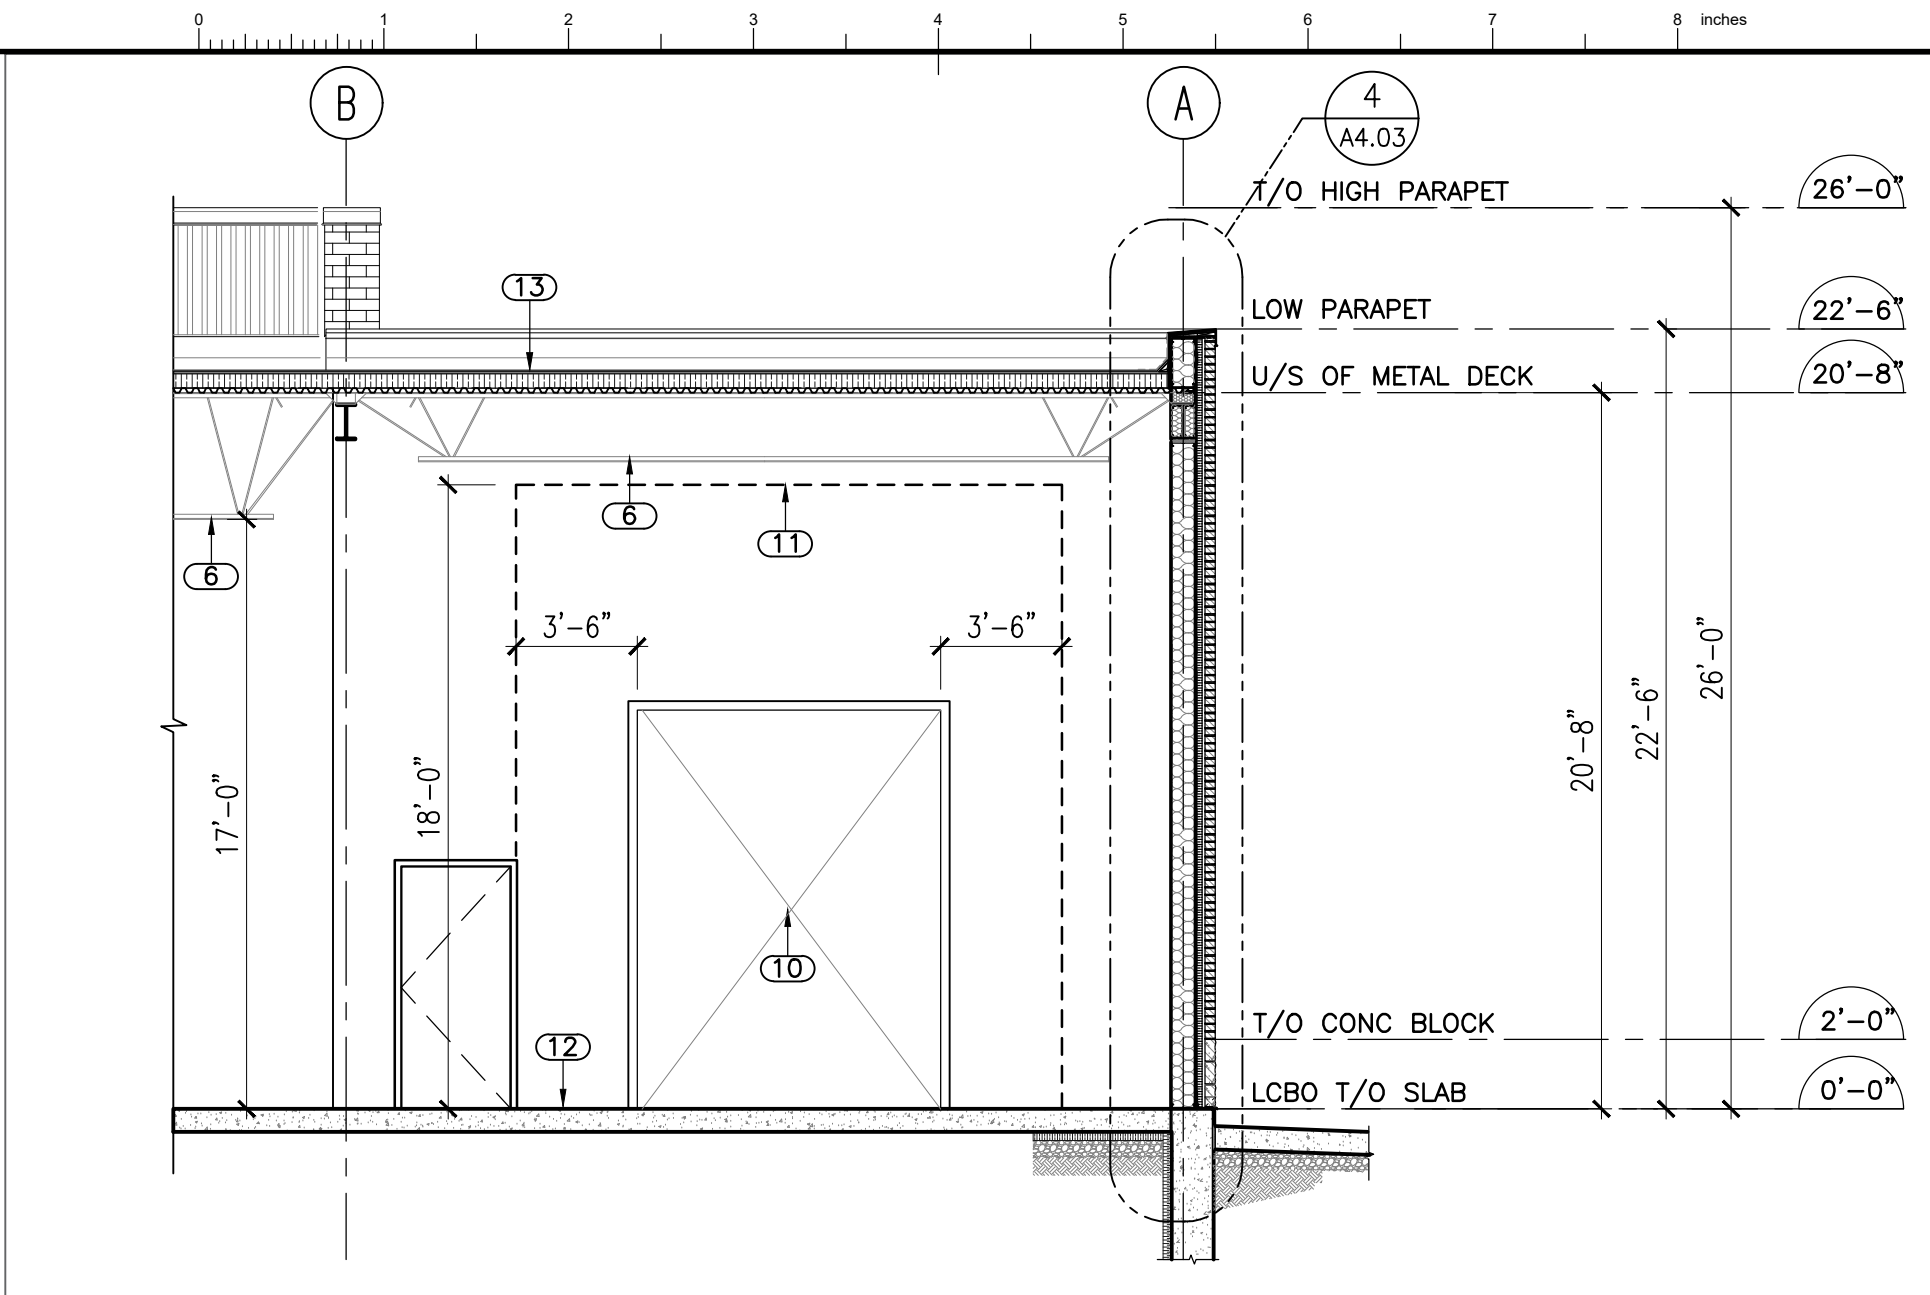

Building Section 3
Scale: 3/16"=1'-0" A4.01

KEY NOTES	
1	ALUMINUM SLIDING DOOR, SIDE-LIGHT, TRANSOM AND WINDOW. REFER TO EXTERIOR ELEVATIONS A2.00. • VISION GLAZING SYSTEM TO BE THERMALLY BROKEN ALUMINUM FRAMES. TYPICAL.
2	ALUMINUM INTERIOR VESTIBULE GLAZING SYSTEM. SINGLE GLAZED LAMINATED GLASS.
3	INNER VESTIBULE GYP. BOARD BULKHEAD C/W SECURITY MESH.
4	SUSPENDED ACCORDION GRILLE 8" STEEL C-CHANNEL C/W STEEL SUPPORTS AND DIAGONAL BRACING. DIAGONAL BRACING TO COMMENCE 2'-0" MIN. ABOVE SUSPENDED C-CHANNEL TO AVOID INTERFERENCE WITH FUTURE TENANT M&E SERVICES. (6" WOOD BLOCKING SECURED TO C-CHANNEL BY TENNAT).
5	CONTROL JOINT (C.J.). REFER TO GENERAL NOTES.
6	OPEN WEB STEEL JOISTS(OWSJ) OR ALTERNATE ROOF FRAMING, MEMBERS SIZES, LAYOUT BY LANDLORD STRUCTURAL CONSULTANT.
7	PREFINISHED METAL SCREEN FOR RTU (WHERE APPLICABLE TO SATISFY CODE AND MUNICIPAL REQUIREMENTS: RTUs REQUIREMENT SHALL BE COORDINATED WITH LCBO LEASE AGREEMENT AND LCBO MECHANICAL REVIEWED DRAWINGS.
8	LCBO BEER COLD ROOM (WHEN APPLICABLE) C/W SUSPENDED LAY-IN-TILE CEILING SYSTEM, LCBO TO CONFIRM. • MINIMUM REQUIRED OVERHEAD CLEARANCE FROM T/O LCBO BEER COLD ROOM TO U/S OF STRUCTURE TO BE 6" MINIMUM.
9	TENANT'S SUSPENDED GYP. BOARD CEILING BRACED TO U/S OF BASE BUILDING STRUCTURE. CEILING HEIGHT TO BE 11'-6" UNLESS NOTED OTHERWISE.
10	RECEIVING AREA: O/H DOOR OPEN. • O/H DOOR FOR TYPICAL LCBO "WALKIE-REACH LOADING CONDITION IS 9'-0" WIDE x 11'-6" HIGH. • O/H DOOR FOR TYPICAL LCBO "DOCK LEVELLER LOADING CONDITION IS 8'-0" WIDE x 8'-6" HIGH.
11	PLYWOOD PANELS IN-LIEU OF DRYWALL. PROVIDE 3/4" PLYWOOD WALL PANELS ABOVE DOOR JAMB AND AT SIDES. PROVIDE 'J' MOULD AT JOINTS BETWEEN DRYWALL AND PLYWOOD FOR SMOOTH TRANSITION. (BY LANDLORD)
12	CONCRETE SLAB-ON-GRADE. REFER TO LANDLORD'S STRUCTURAL CONSULTANT'S DWGS
13	TYPICAL ROOFING ASSEMBLY. REFER TO ROOF PLAN A1.02.
14	FUTURE TENANT STEEL STUD PARTITION TO U/S OF ROOF STRUCTURE.
15	FUTURE TENANT SIGNAGE. REFER TO EXTERIOR ELEVATION A2.01.
16	TYPICAL ROUGH-IN LOCATIONS FOR LCBO MOTORIZED SECURITY SHUTTERS AT VISION GLASS WINDOW LOCATIONS. • CONDUITS TO BE ROUGHED IN AT RIGHT SIDE OF VISION GLASS WINDOWS UNLESS NOTED OTHERWISE. • WHERE RIGHT HAND SIDE ROUGH-IN IS NOT POSSIBLE DUE TO INTERFERENCES, PROVIDE ROUGH-IN ABOVE WINDOW LOCATIONS AS INDICATED. • REFER TO CONSTRUCTION PLAN A1.01. • REFER TO DETAILS 3, 6, 9 & 12/A5.02. **NOTE: ROUGH-INS INDICATED ARE FOR REFERENCE ONLY. ACTUAL REQUIRED MOTORIZED ROUGH-INS AND LOCATIONS WILL BE CONFIRMED BY LCBO ON THE LCBO PROVIDED COORDINATION PLAN.
17	TYPICAL ROUGH-IN LOCATIONS FOR LCBO MOTORIZED SUNSHADE (WHERE APPLICABLE) AT VISION GLASS WINDOW LOCATIONS. • CONDUITS TO BE ROUGHED IN AT RIGHT SIDE OF VISION GLASS WINDOWS UNLESS NOTED OTHERWISE. • REFER TO CONSTRUCTION PLAN A1.01. • ROUGH-INS/REQUIREMENTS FOR MOTORIZED SUNSHADES TO BE CONFIRMED BY LCBO. • REFER TO DETAILS 3, 6, 9 & 12/A5.02. **NOTE: ROUGH-INS INDICATED ARE FOR REFERENCE ONLY. ACTUAL REQUIRED MOTORIZED ROUGH-INS AND LOCATIONS WILL BE CONFIRMED BY LCBO ON THE LCBO PROVIDED COORDINATION PLAN.
GENERAL NOTES	
A	PROVIDE VERTICAL CONTROL JOINT AT ALL WINDOW JAMBS ON EXTERIOR WALLS FROM T/O FLOOR SLAB TO U/S OF ROOF DECK. TYPICAL. PROVIDE HORIZONTAL CONTROL JOINTS ON ALL EXTERIOR WALLS (INCLUDE THE VESTIBULE GYPSUM BOARD WALLS) AT 6" BELOW ROOF JOIST. TYPICAL. LANDLORD TO PROVIDE HORIZONTAL AND VERTICAL CONTROL JOINTS ON ALL EXTERIOR WALLS (INCLUDE THE VESTIBULE GYPSUM BOARD WALLS), WHERE A WALL OR PARTITION RUNS IN AN UNINTERRUPTED STRAIGHT PLANE EXCEEDING 30 LINEAR FEET. VERTICAL JOINTS AT WINDOWS TO BE BEHIND SECURITY SHUTTER GUIDES. WHERE A CONTROL JOINT OCCURS IN AN ACOUSTICAL OR FIRE RATED SYSTEM, BLOCKING SHALL BE PROVIDED BEHIND THE CONTROL JOINT BY USING A BACKING MATERIAL SUCH 5/8"(15.9mm) TYPES X GYPSUM BOARD, MINERAL FIBER OR OTHER TESTED EQUIVALENT MATERIALS.

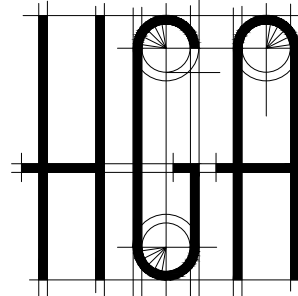

HANNA, GHOBRIAL
AND ASSOCIATES LTD.

engineering
architecture

3100 Temple Drive, Suite 100
Windsor, ON N8W 5J6
(519) 945-7373 FAX.-5636

This drawing shall not be used for construction unless it is countersigned by the CONSULTANT

NOTE:
ENGINEERED SHOP DRAWINGS FOR ANY "MANUFACTURED COMPONENT" FORMING PART OF THE BUILDING (i.e. ENGINEERED ROOF TRUSSES, ENGINEERED FLOOR JOISTS, TIMERS, ETC.) MUST BE SUBMITTED TO HANNA GHOBRIAL & ASSOCIATES LTD. FOR REVIEW AND APPROVAL. IF ENGINEERED SHOP DRAWINGS ARE NOT SUBMITTED AND APPROVED, HANNA GHOBRIAL & ASSOCIATES LTD WILL NOT BE RESPONSIBLE FOR ANY ASSOCIATED COSTS OR DAMAGES.

ALL DRAWINGS, SPECIFICATIONS AND OTHER RELATED DOCUMENTS ARE THE COPYRIGHT PROPERTY OF THE CONSULTANT AND SHALL BE RETURNED UPON REQUEST.
REPRODUCTION OF DRAWINGS AND RELATED DOCUMENTS, IN WHOLE OR IN PART, IS FORBIDDEN WITHOUT THE WRITTEN PERMISSION OF THE CONSULTANT.

THE CONTRACTOR SHALL CHECK AND VERIFY ALL PERTINENT DIMENSIONS AND REPORT ANY DISCREPANCIES TO THE CONSULTANT BEFORE PROCEEDING WITH THE WORK.
THIS DRAWING SHALL NOT BE USED FOR CONSTRUCTION UNLESS IT IS COUNTERSIGNED BY THE CONSULTANT.

THIS DRAWING IS NOT TO BE SCALED
USE FIGURED DIMENSIONS ONLY.

12		
11		
10		
9		
8		
7		

6	2023/09/26	SPA- REV. TRUCK ROUTE
5	2023/08/15	PHOTOMETRIC ANALYSIS
4	2023/08/03	CLIENT REVIEW
3	2023/07/31	PRE-SUBMITTAL APPLIC.
2	2023/07/26	CLIENT REVIEW
1	2023/06/21	SITE PLAN APPLICATION
YY/MM/DD		
No.	Date:	Issued For:

Date: JUNE 2023

Drawn By: H.R.

Checked By: E.K.

Client:
Joseph B. Mikhail
Mikhail Holdings Ltd.
100 Ouellette Ave., Suite 700
Windsor, ON, N9A 6T3

Project Title:

LCBO
NEW
LCBO STORE

Address: 400 SANDWICH STREET
AMHERSTBURG, ONTARIO N9V 3L4

Project No.:

22-0445

Sheet Title:

BUILDING CROSS
SECTIONS

Sheet No.:

A4.01